# MAISON UNIFAMILIALE

DOSSIER 1
125, rue des Érables
Ville fictive (Québec)

**Conçu par Jeremy, enseignant**

Maison unifamiliale contemporaine de deux étages avec sous-sol aménagé : deux toits monopentes décalés à grands débords (900 mm) séparés par une bande vitrée, pierre naturelle à l'entrée, zinc prépatiné et cèdre brûlé, grandes fenêtres au sud. Rez-de-chaussée à aire ouverte, quatre chambres, trois salles de bain ou salles d'eau. Chauffage par air pulsé (fournaise électrique et thermopompe), ventilation par VRC.

**LISTE DES FEUILLES**

| Feuille | Titre |
|---|---|
| 000 | Page de garde et liste des feuilles |
| A-100 | Plan d'implantation et de site |
| A-101 | Plan du sous-sol |
| A-102 | Plan du rez-de-chaussée |
| A-103 | Plan de l'étage |
| A-201 | Élévations |
| A-301 | Coupe transversale et nomenclatures |
| A-302 | Coupe longitudinale, coupe de mur et matériaux |
| S-101 | Plan des fondations et détail type |
| P-101 | Plomberie sous-sol |
| P-102 | Plomberie rez-de-chaussée |
| P-103 | Plomberie étage |
| P-104 | Schéma isométrique et nomenclature des appareils |
| E-101 | Électricité sous-sol |
| E-102 | Électricité rez-de-chaussée |
| E-103 | Électricité étage |
| M-101 | Chauffage et ventilation sous-sol |
| M-102 | Chauffage et ventilation rez-de-chaussée |
| M-103 | Chauffage et ventilation étage |

**DONNÉES DU BÂTIMENT**

| Élément | Valeur |
|---|---|
| Usage | Habitation unifamiliale |
| Étages | 2 + sous-sol aménagé |
| Emprise au sol | 93,5 m² |
| Superficie habitable | 246 m² (3 niveaux) |
| Structure | Ossature de bois, solives en I, fondation de béton |
| Toiture | Deux monopentes décalés, membrane élastomère, débords 900 |
| Chauffage | Air pulsé + thermopompe, VRC |
| Eau et égout | Réseaux municipaux |
| Lot | 18 000 × 33 000 |

Pavillon de L'AVENIR
Centre de formation professionnelle

PLAN D'EXERCICE
LECTURE DE PLANS

PROJET

**MAISON UNIFAMILIALE**
**DOSSIER 1**

125, rue des Érables
Ville fictive (Québec)

**UTILISATION EN CLASSE**

Ce dossier sert à apprendre à lire des plans : repérer les feuilles, les échelles, les symboles, les cotes et les liens entre les disciplines.

Une maison à trois niveaux : chaque niveau a son plan (A), sa plomberie (P), son électricité (E) et son chauffage (M).

Les renvois (bulles de coupe, types de fenêtres, numéros de portes) relient les feuilles entre elles.

Bâtiment fictif. Les valeurs sont plausibles mais non vérifiées pour la construction.

TITRE DE LA FEUILLE

**PAGE DE GARDE**
**ET LISTE DES FEUILLES**

CONÇU PAR
**Jeremy, enseignant**


**DESSIN À DES FINS D'ENSEIGNEMENT — NE PAS UTILISER POUR LA CONSTRUCTION**

ÉCHELLE
—

FEUILLE
**000**
Dossier D1

DATE
Octobre 2026

**LOT 4 123 456 · SUPERFICIE 594,0 m²**

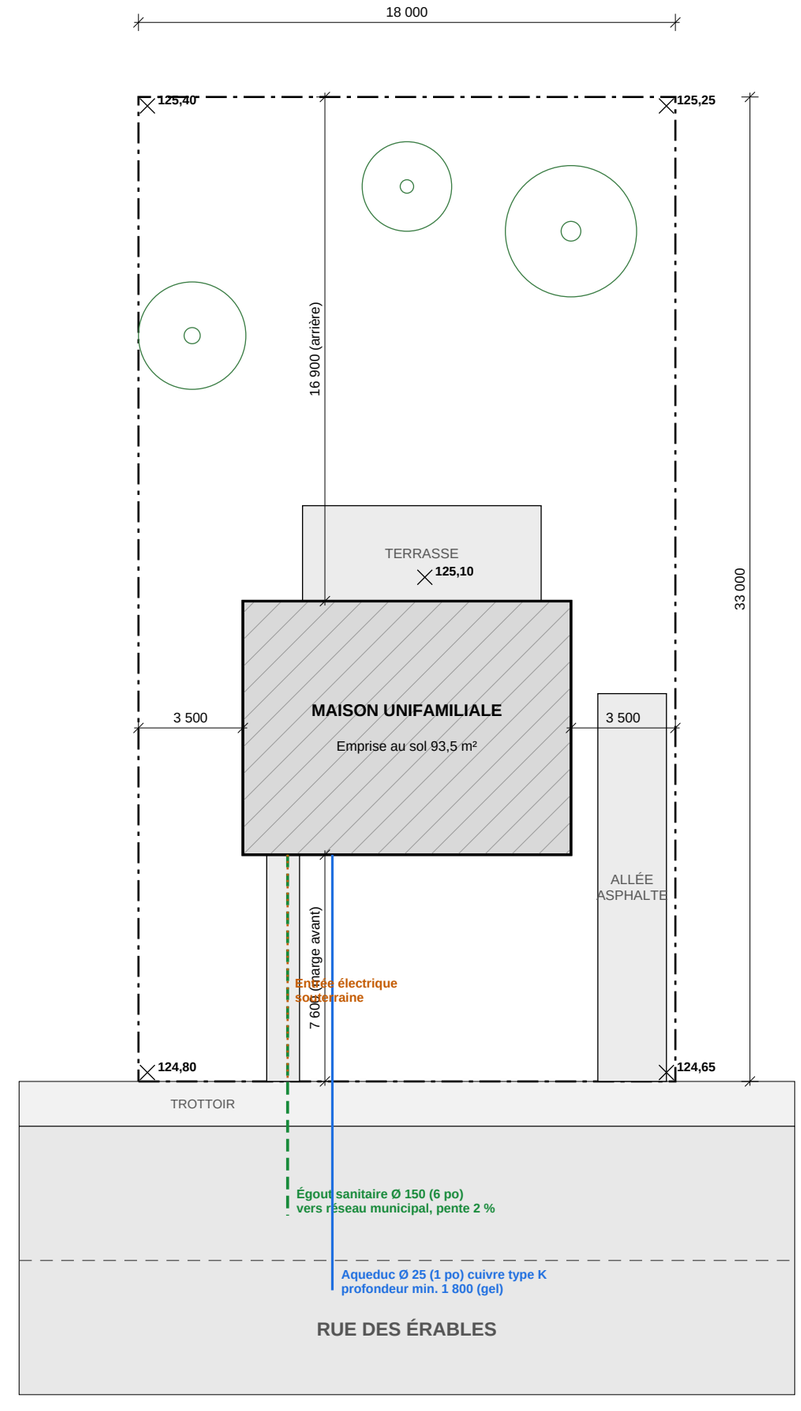


N

0 2 4 6 8 10 m

**1 PLAN D'IMPLANTATION**
Échelle 1:200

Pavillon de L'AVENIR
Centre de formation professionnelle

**PLAN D'EXERCICE**
**LECTURE DE PLANS**

PROJET

## MAISON UNIFAMILIALE
## DOSSIER 1

125, rue des Érables
Ville fictive (Québec)

### NOTES D'IMPLANTATION

Implantation à confirmer par un arpenteur-géomètre.

Marge avant minimale : 7,5 m. Marges latérales : 2,0 m.

Niveaux du terrain en mètres (altitude géodésique).

Pente du terrain fini : 2 % minimum en s'éloignant du bâtiment.

### LÉGENDE

— · — Limite de lot

Hachures : emprise du bâtiment

Croix : niveau du terrain (m, géodésique)

Bleu : aqueduc · Vert pointillé : égout sanitaire

Orange pointillé : entrée électrique

TITRE DE LA FEUILLE


**PLAN D'IMPLANTATION ET DE SITE**

CONÇU PAR
**Jeremy, enseignant**
DESSIN À DES FINS D'ENSEIGNEMENT — NE PAS UTILISER POUR LA CONSTRUCTION

ÉCHELLE
**1:200**

DATE
Octobre 2026

FEUILLE
**A-100**
Dossier D1

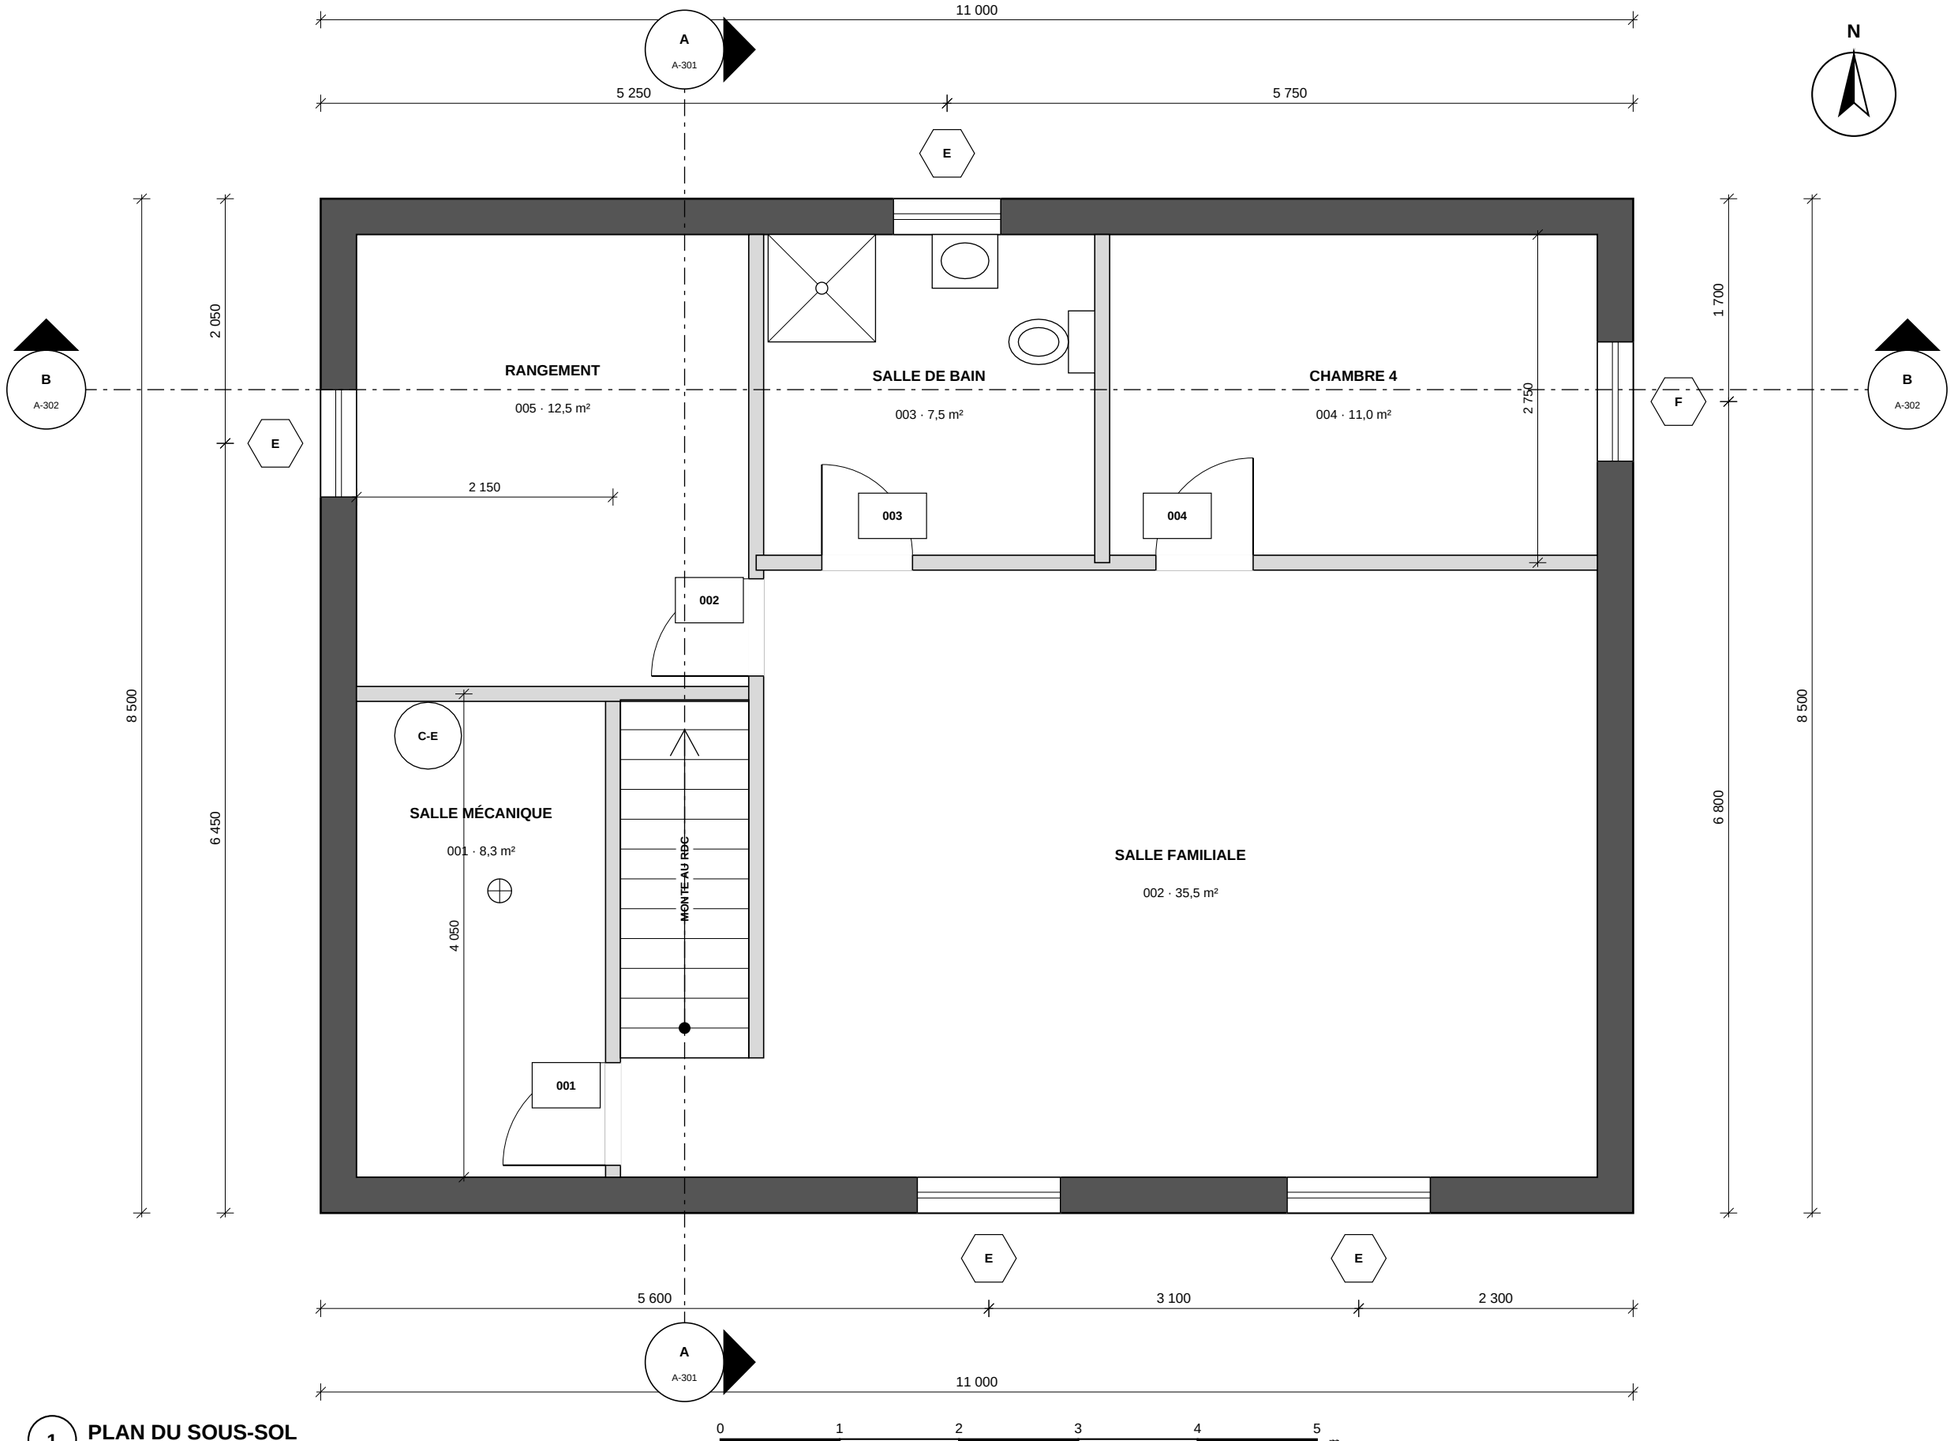


**1 PLAN DU SOUS-SOL**
Échelle 1:50

Pavillon de L'AVENIR
Centre de formation professionnelle

**PLAN D'EXERCICE**
**LECTURE DE PLANS**

PROJET

## MAISON UNIFAMILIALE
## DOSSIER 1

125, rue des Érables
Ville fictive (Québec)

### NOTES GÉNÉRALES

Toutes les cotes sont en millimètres.

Hauteur libre sous les solives : 2 380 mm.

Mur de fondation : béton 250 isolé à l'extérieur (voir A-302).

Fenêtre F : issue de secours de la chambre, margelle de 1 000 de profondeur.

Poutre d'acier et poteaux : voir S-101.

### LÉGENDE

Mur extérieur (poché foncé) : voir composition M1, feuille A-301

Mur intérieur (poché pâle) : voir composition M2

Hexagone : type de fenêtre (voir nomenclature, A-301)

Rectangle : numéro de porte (voir nomenclature, A-301)

Cotes en millimètres, aux faces extérieures du revêtement intermédiaire et aux axes des ouvertures

TITRE DE LA FEUILLE

**PLAN DU SOUS-SOL**

CONÇU PAR

**Jeremy, enseignant**

**DESSIN À DES FINS D'ENSEIGNEMENT — NE PAS UTILISER POUR LA CONSTRUCTION**

ÉCHELLE

**1:50**


DATE

Octobre 2026

FEUILLE

**A-101**

Dossier D1

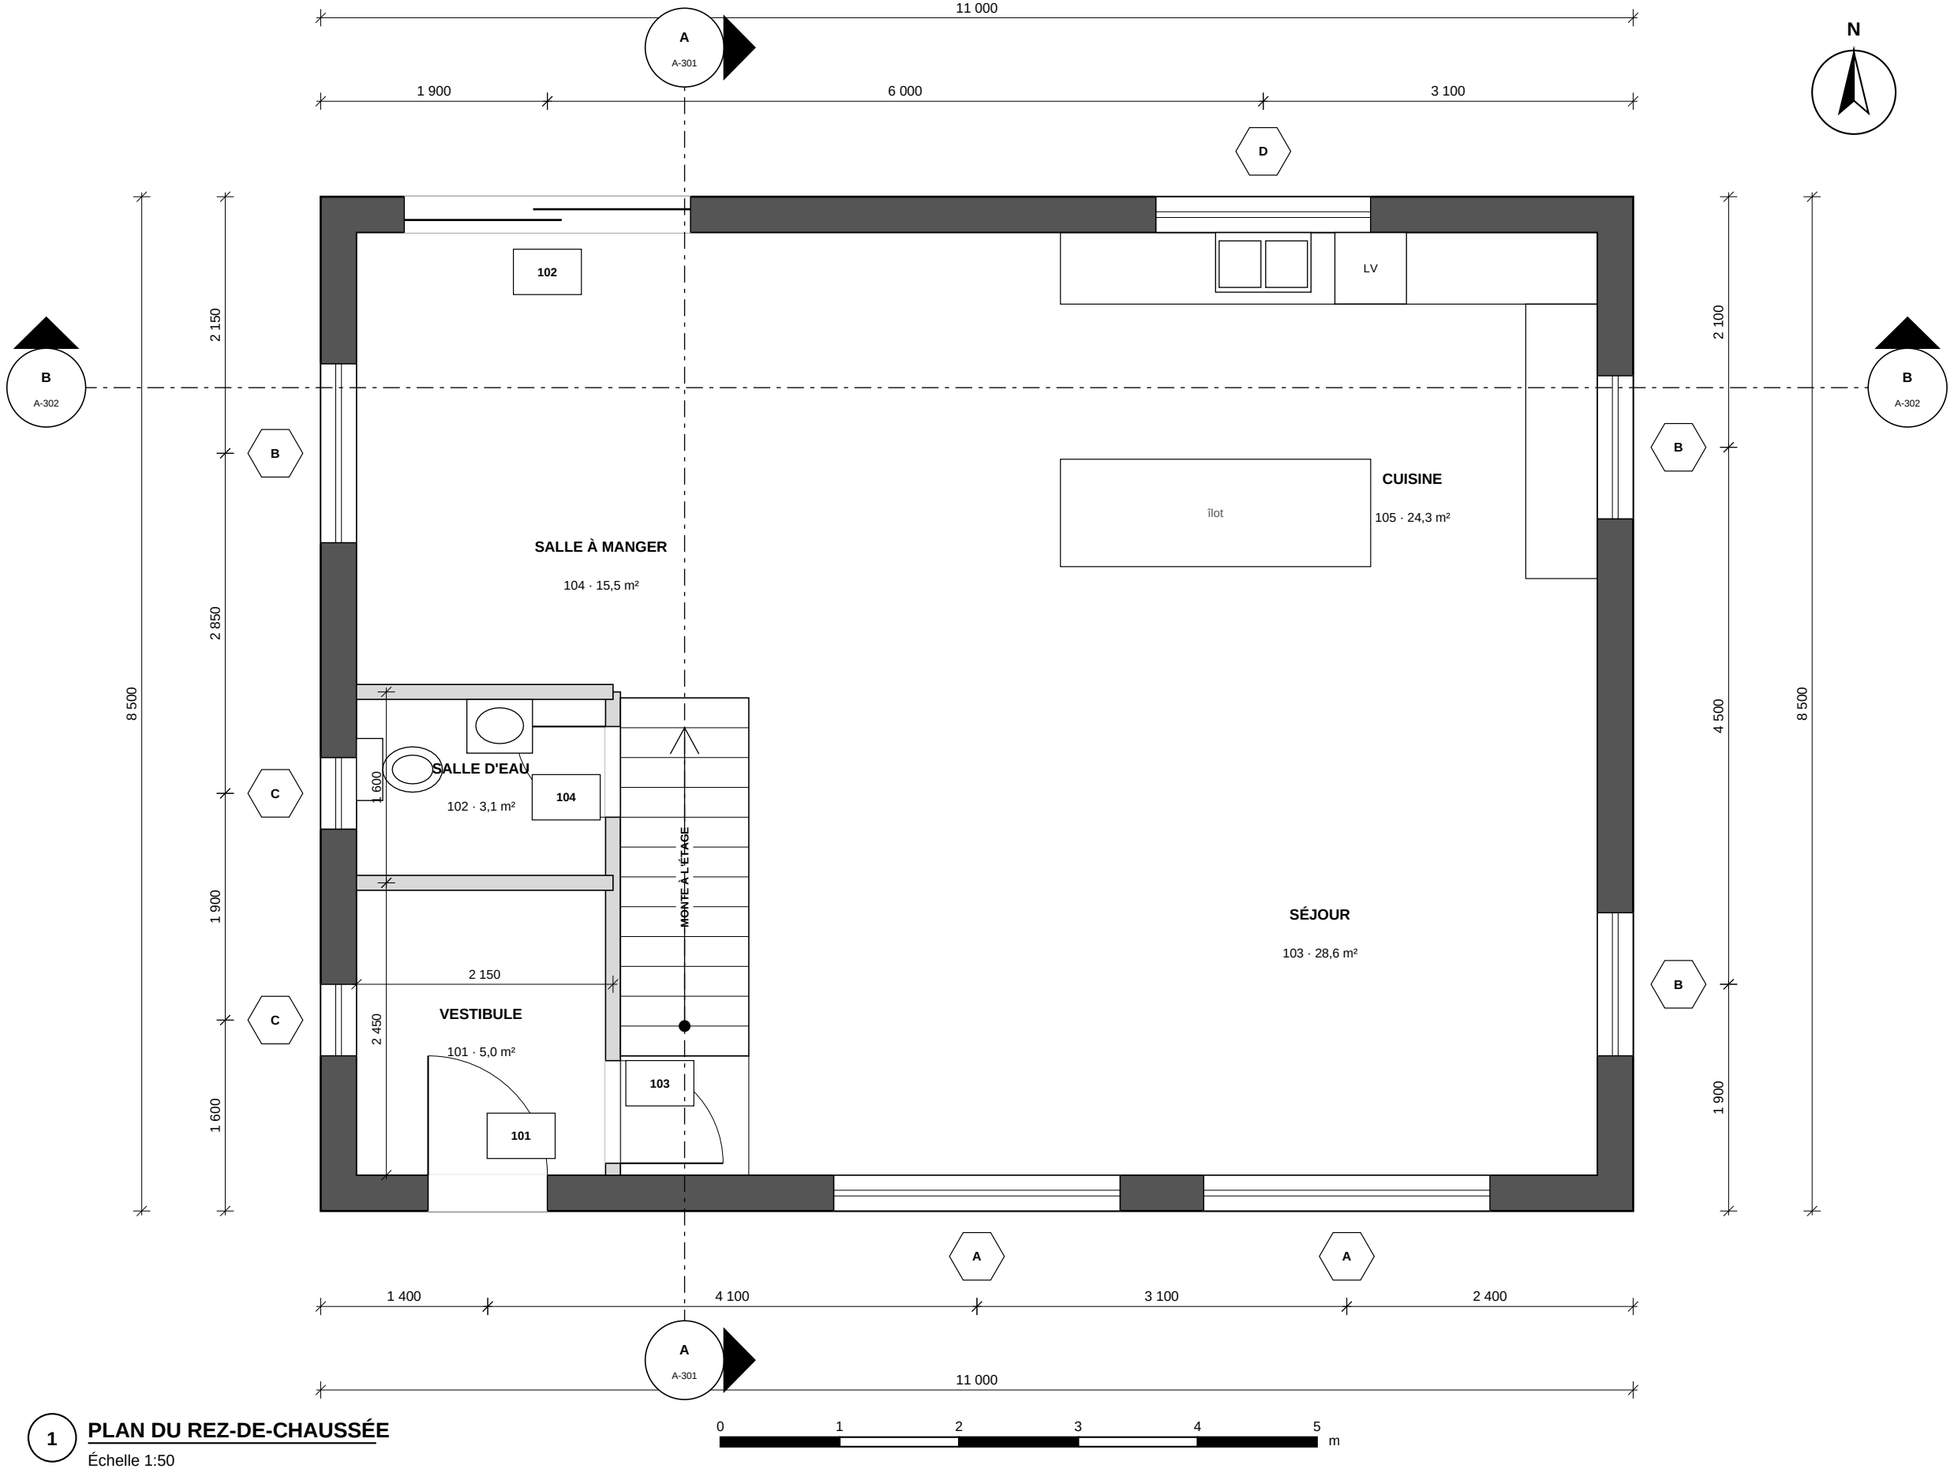


**1** **PLAN DU REZ-DE-CHAUSSÉE**
Échelle 1:50

Pavillon de L'AVENIR
Centre de formation professionnelle

**PLAN D'EXERCICE**
**LECTURE DE PLANS**

PROJET

## MAISON UNIFAMILIALE
## DOSSIER 1

125, rue des Érables
Ville fictive (Québec)

### NOTES GÉNÉRALES

Toutes les cotes sont en millimètres.

Cotes extérieures prises à la face extérieure du panneau OSB.

Hauteur libre sous plafond : 2 740 mm.

Escalier : volée de 12 contremarches, palier au sud. L'escalier du sous-sol est juste en dessous (même sens).

Garde-corps de verre de 900 le long de la cage, côté séjour.

Comptoirs : profondeur 600, hauteur 915; îlot de 900.

### LÉGENDE

Mur extérieur (poché foncé) : voir composition M1, feuille A-301

Mur intérieur (poché pâle) : voir composition M2

Hexagone : type de fenêtre (voir nomenclature, A-301)

Rectangle : numéro de porte (voir nomenclature, A-301)

Cotes en millimètres, aux faces extérieures du revêtement intermédiaire et aux axes des ouvertures

TITRE DE LA FEUILLE


**PLAN DU REZ-DE-CHAUSSÉE**

CONÇU PAR
**Jeremy, enseignant**
**DESSIN À DES FINS D'ENSEIGNEMENT — NE PAS UTILISER POUR LA CONSTRUCTION**

ÉCHELLE
**1:50**

DATE
Octobre 2026

FEUILLE
**A-102**
Dossier D1

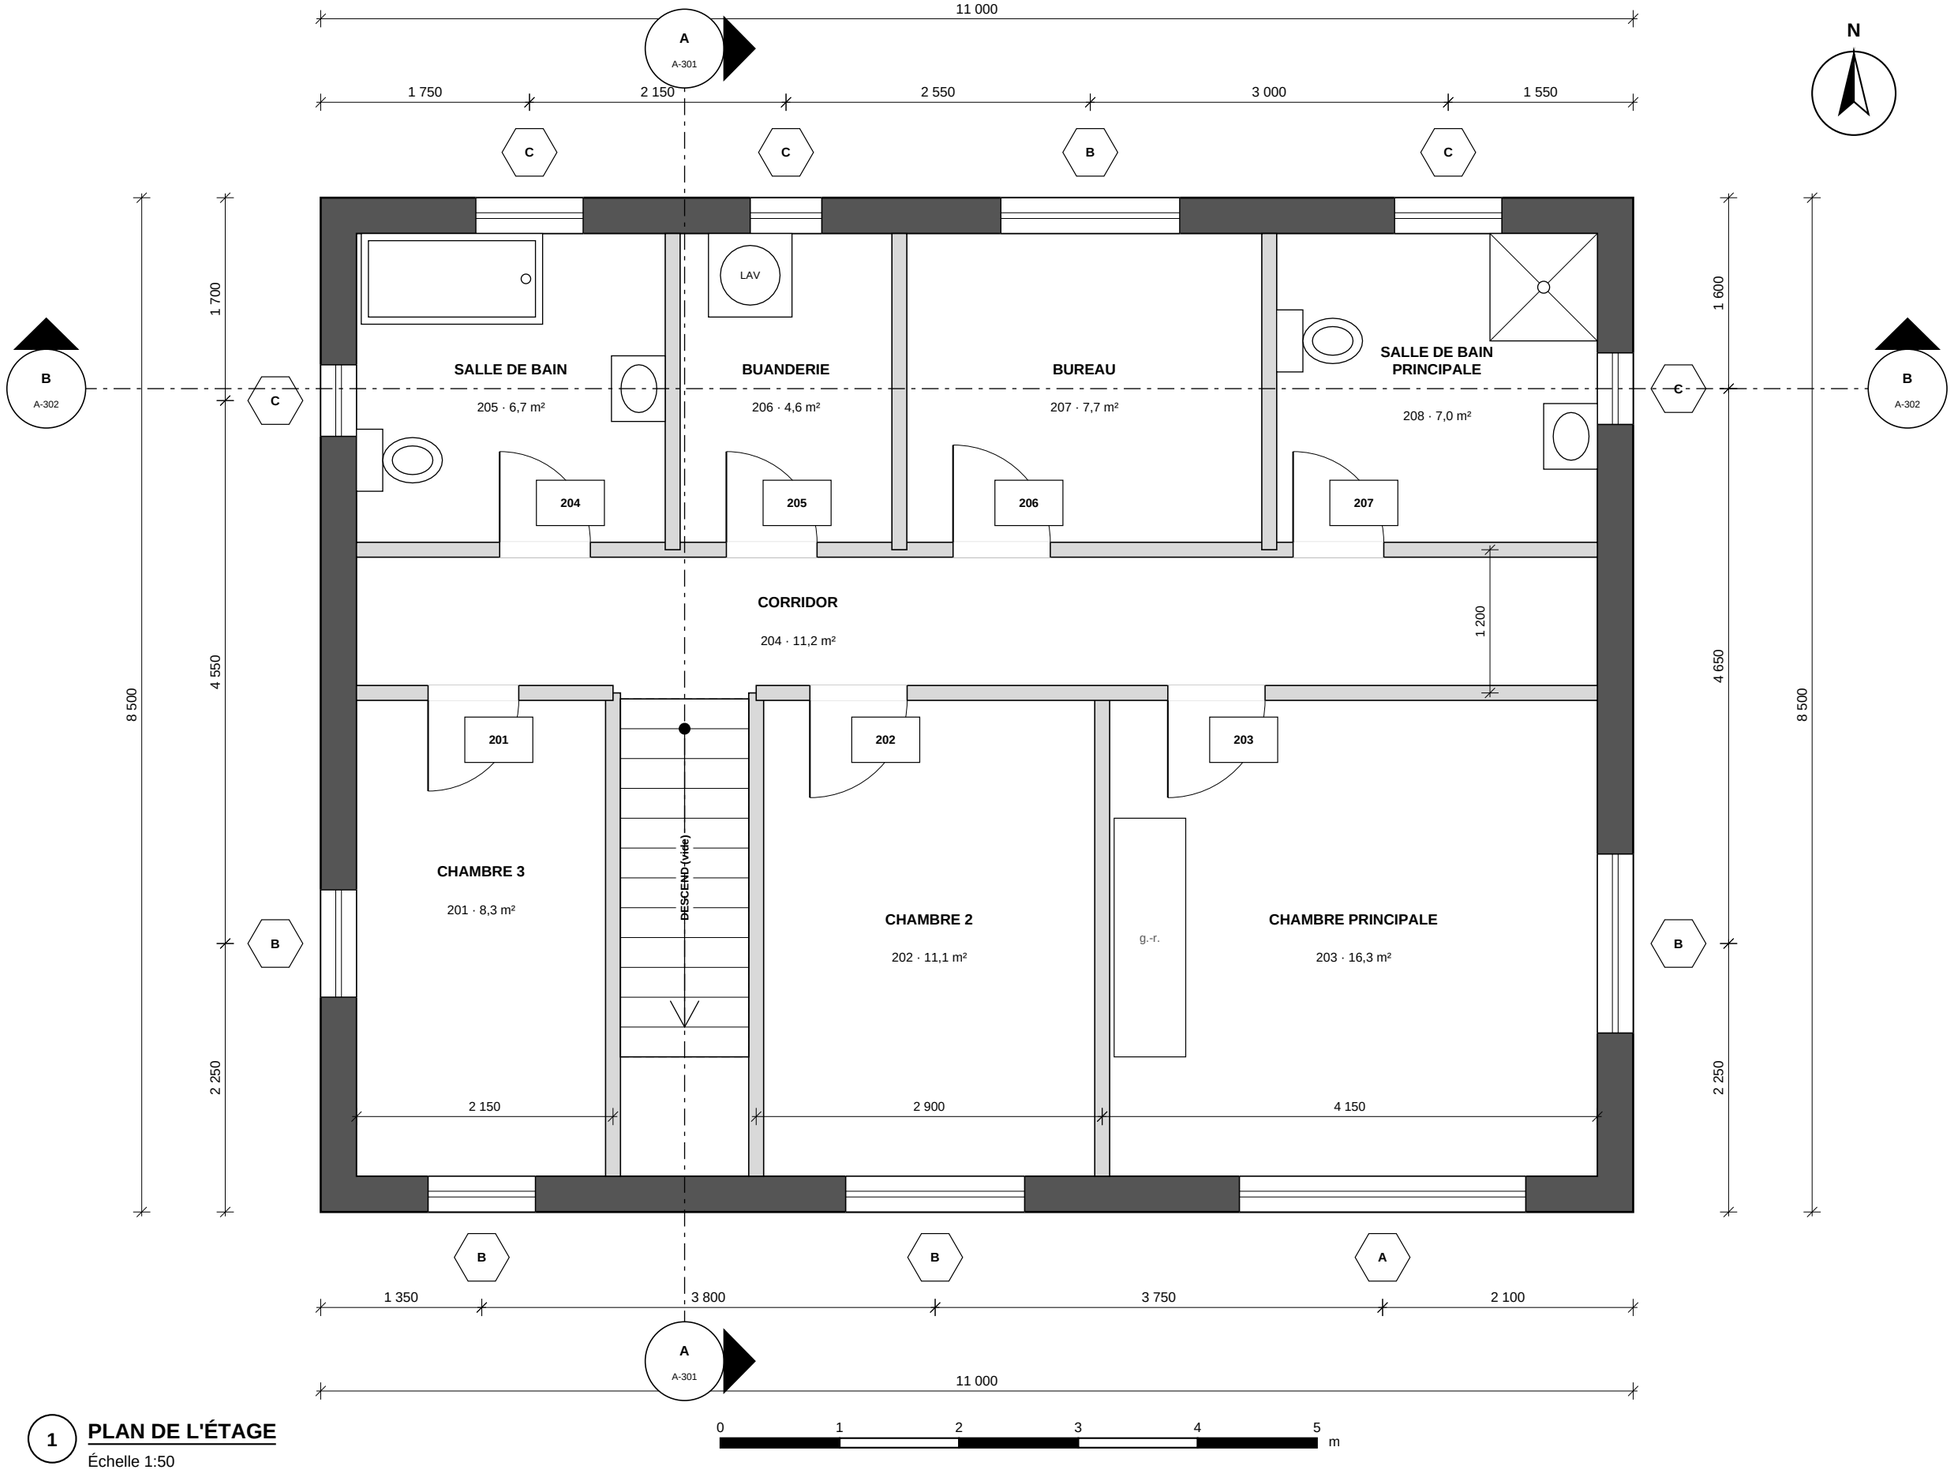


**1 PLAN DE L'ÉTAGE**
Échelle 1:50

Pavillon de L'AVENIR
Centre de formation professionnelle

**PLAN D'EXERCICE**
**LECTURE DE PLANS**

PROJET

## MAISON UNIFAMILIALE
## DOSSIER 1

125, rue des Érables
Ville fictive (Québec)

### NOTES GÉNÉRALES

Toutes les cotes sont en millimètres.

Hauteur libre sous plafond : 2 610 mm.

Cage d'escalier ouverte : garde-corps de 900 au pourtour du vide.

Buanderie : drain de plancher et bac de récupération sous la laveuse.

### LÉGENDE

Mur extérieur (poché foncé) : voir composition M1, feuille A-301

Mur intérieur (poché pâle) : voir composition M2

Hexagone : type de fenêtre (voir nomenclature, A-301)

Rectangle : numéro de porte (voir nomenclature, A-301)

Cotes en millimètres, aux faces extérieures du revêtement intermédiaire et aux axes des ouvertures

TITRE DE LA FEUILLE

**PLAN DE L'ÉTAGE**

CONÇU PAR

**Jeremy, enseignant**

**DESSIN À DES FINS D'ENSEIGNEMENT — NE PAS UTILISER POUR LA CONSTRUCTION**

ÉCHELLE

**1:50**


DATE

Octobre 2026

FEUILLE


**A-103**

Dossier D1

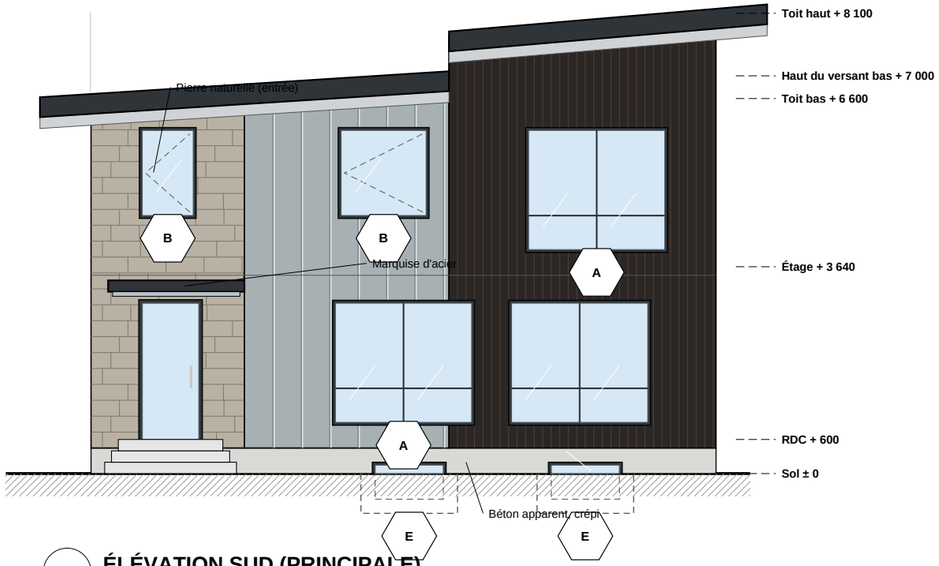



1 **ÉLÉVATION SUD (PRINCIPALE)**

Échelle 1:105

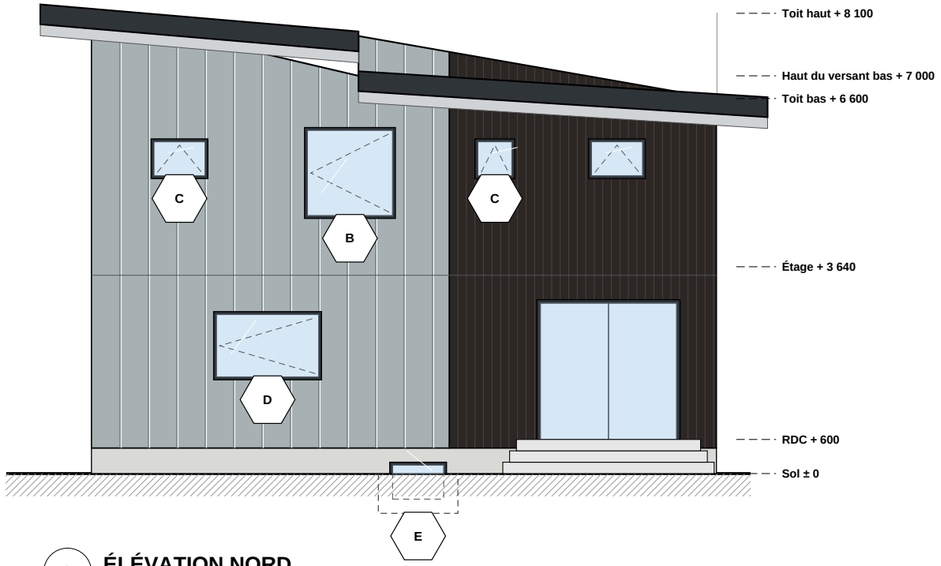



2 **ÉLÉVATION NORD**

Échelle 1:105

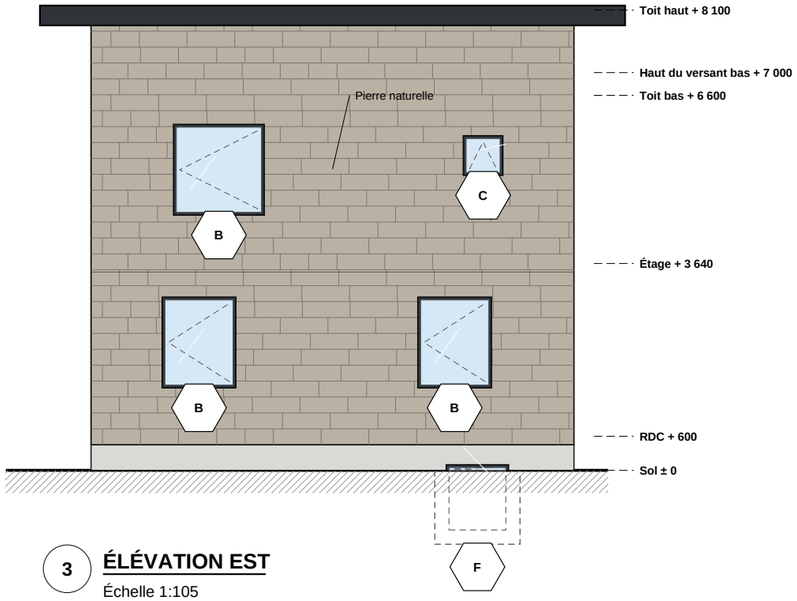


3 **ÉLÉVATION EST**

Échelle 1:105

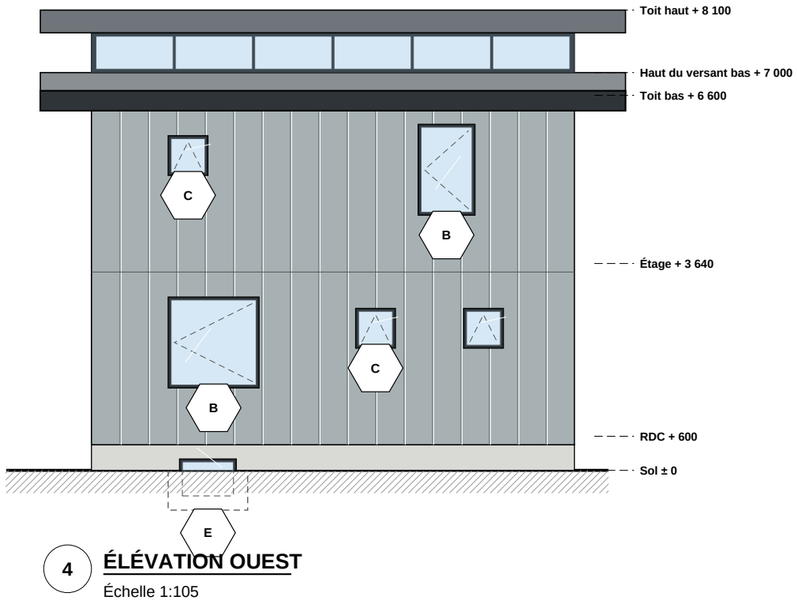


4 **ÉLÉVATION OUEST**

Échelle 1:105

Pavillon de L'AVENIR
Centre de formation professionnelle

**PLAN D'EXERCICE**
**LECTURE DE PLANS**

PROJET

## MAISON UNIFAMILIALE
## DOSSIER 1

125, rue des Érables
Ville fictive (Québec)

### NOTES D'ÉLÉVATION

Revêtements : pierre naturelle (entrée et mur est), zinc prépatiné à joints debout (versant bas), cèdre brûlé (volume haut).

Marquise d'acier en porte-à-faux au-dessus de l'entrée.

Deux toits monopentes décalés (pente d'environ 4 %) : débords de 900, bandeau d'aluminium noir; bande vitrée haute entre les deux versants (vue sur l'élévation ouest).

Fenêtres à cadre noir, verre triple. Hexagones : types de fenêtres, voir A-301.

Fenêtres du sous-sol : margelles galvanisées (en tirets).

### NIVEAUX

Sol : ± 0

Sous-sol : – 2 100

RDC : + 600

Étage : + 3 640

Toit bas : + 6 600

Haut du versant bas : + 7 000

Toit haut : + 8 100

TITRE DE LA FEUILLE

**ÉLÉVATIONS**

CONÇU PAR

**Jeremy, enseignant**

**DESSIN À DES FINS D'ENSEIGNEMENT — NE PAS UTILISER POUR LA CONSTRUCTION**

ÉCHELLE

**1:105**


DATE

Octobre 2026

FEUILLE

**A-201**

Dossier D1

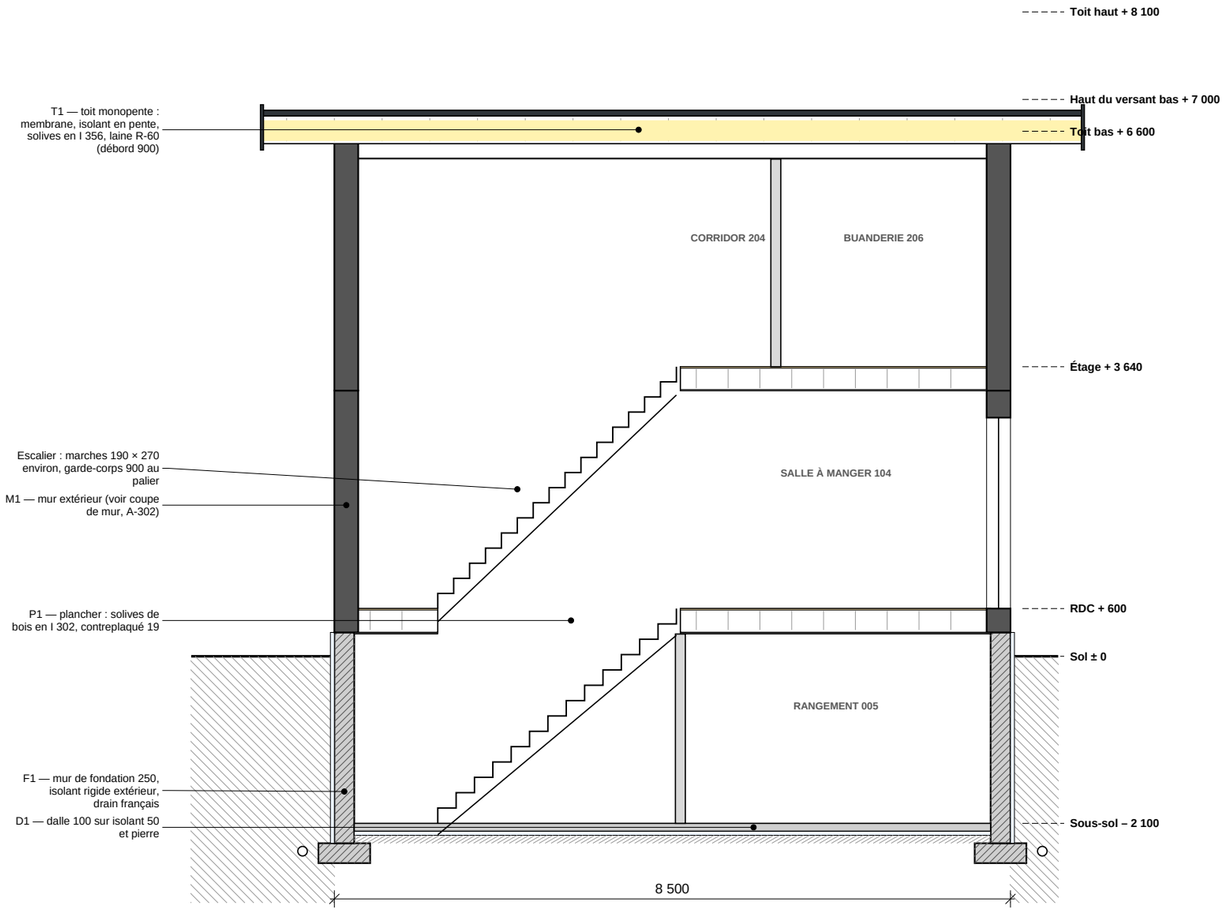


## A — COUPE A — TRANSVERSALE (vers l'est)

Échelle 1:75

### NOMENCLATURE DES PORTES

| No | Dimensions (mm) | Type | Matériau | Quincaillerie |
|---|---|---|---|---|
| 001 | 860 × 2 030 | Battante | Âme pleine, MDF peint | Passage |
| 002 | 815 × 2 030 | Battante | Âme pleine, MDF peint | Passage |
| 003 | 760 × 2 030 | Battante | Âme pleine, MDF peint | Intimité (verrou) |
| 004 | 815 × 2 030 | Battante | Âme pleine, MDF peint | Passage |
| 101 | 1 000 × 2 400 | Battante | Acier isolé, vitrage pleine hauteur | Serrure + pêne dormant |
| 102 | 2 400 × 2 400 | Coulissante | PVC, vitrage triple | Loquet + barre de sécurité |
| 103 | 860 × 2 030 | Battante | Âme pleine, MDF peint | Passage |
| 104 | 760 × 2 030 | Battante | Âme pleine, MDF peint | Intimité (verrou) |
| 201 | 760 × 2 030 | Battante | Âme pleine, MDF peint | Passage |
| 202 | 815 × 2 030 | Battante | Âme pleine, MDF peint | Passage |
| 203 | 815 × 2 030 | Battante | Âme pleine, MDF peint | Passage |
| 204 | 760 × 2 030 | Battante | Âme pleine, MDF peint | Intimité (verrou) |
| 205 | 760 × 2 030 | Battante | Âme pleine, MDF peint | Passage |
| 206 | 815 × 2 030 | Battante | Âme pleine, MDF peint | Passage |
| 207 | 760 × 2 030 | Battante | Âme pleine, MDF peint | Intimité (verrou) |

### NOMENCLATURE DES FENÊTRES

| Type | Qté | Larg. × haut. (mm) | Allège | Ouverture | Vitrage |
|---|---|---|---|---|---|
| A | 3 | 2 400 × 2 100 | 300 | Fixe et battant (pleine hauteur) | Triple, faible émissivité, argon |
| B | 8 | 900 / 1 200 / 1 500 × 1 500 | 900 | Battant, à manivelle | Triple, faible émissivité, argon |
| C | 7 | 600 / 900 × 600 | 1 600 | Auvent | Triple, givré |
| D | 1 | 1 800 × 1 100 | 1 100 | Battant, à manivelle | Triple, faible émissivité |
| E | 4 | 900 / 1 200 × 600 | 1 650 | Coulissante (sous-sol) | Double, faible émissivité |
| F | 1 | 1 000 × 1 100 | 1 050 | Battant — issue (margelle) | Double, faible émissivité |

Pavillon de L'AVENIR
Centre de formation professionnelle

**PLAN D'EXERCICE**
**LECTURE DE PLANS**

PROJET

## MAISON UNIFAMILIALE
## DOSSIER 1

125, rue des Érables
Ville fictive (Québec)

### COMPOSITIONS

T1 — Toit monopente (débord 900) : membrane élastomère 2 plis, isolant rigide en pente, contreplaqué 19, solives en I 356, laine soufflée R-60, pare-vapeur, gypse 12,7.

M1 — Mur extérieur : zinc à joints debout (ou pierre, ou cèdre brûlé), fourrures 19, isolant rigide 50, OSB 11, montants 38 × 140 à 400 c/c, laine R-24, pare-vapeur, gypse 12,7.

M2 — Cloison : gypse 12,7 deux faces, montants 38 × 89 à 400 c/c (laine insonorisante autour des salles de bain).

P1 — Plancher : contreplaqué 19 collé-vissé, solives en I 302 à 400 c/c.

D1 — Dalle du sous-sol : béton 100, isolant rigide 50, pierre 200.

F1 — Fondation : mur de béton 250, isolant rigide 50 extérieur, semelle 650 × 250, drain français.

### À OBSERVER

L'allège se mesure à partir du plancher du niveau où se trouve la fenêtre.

Fenêtres E et F : sous-sol (voir les margelles sur A-201).

TITRE DE LA FEUILLE

**COUPE TRANSVERSALE ET NOMENCLATURES**

CONÇU PAR

**Jeremy, enseignant**

**DESSIN À DES FINS D'ENSEIGNEMENT — NE PAS UTILISER POUR LA CONSTRUCTION**

ÉCHELLE

**1:75**


DATE

Octobre 2026

FEUILLE

**A-301**

Dossier D1

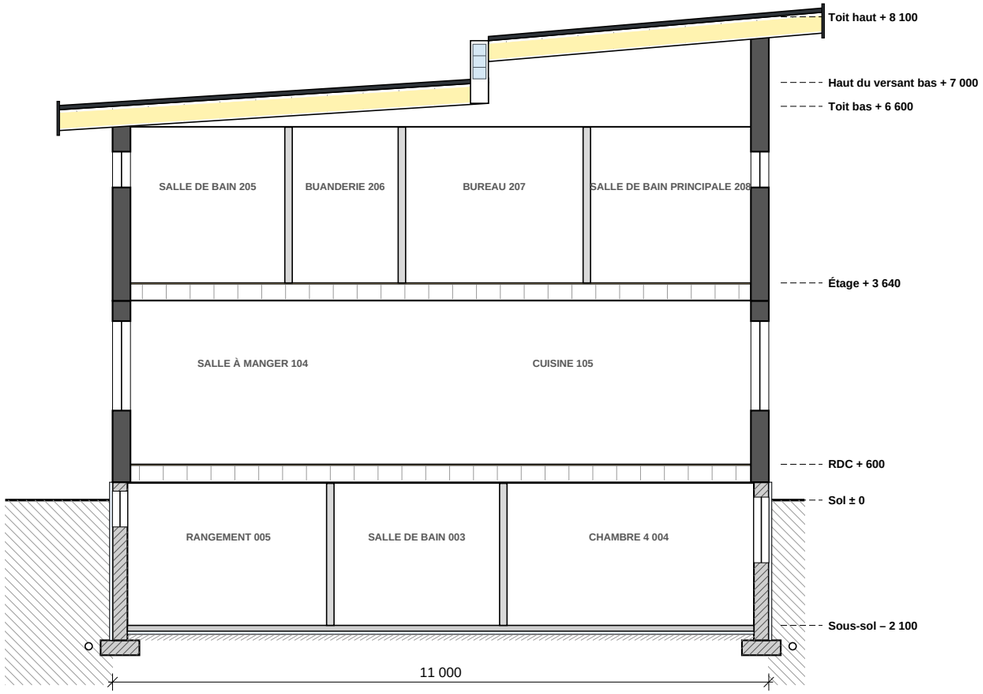



## B — COUPE B — LONGITUDINALE (vers le nord)

Échelle 1:100

### LÉGENDE DES MATÉRIAUX EN COUPE

- Béton coulé
- Sol naturel (terre)
- Pierre concassée, pierre nette
- Brique d'argile
- Bloc de béton
- Isolant rigide (panneau)
- Isolant en natte (laine)
- Bois de charpente coupé
- Contreplaqué ou OSB
- Plaque de plâtre (gypse)
- Acier
- Lame d'air, vide

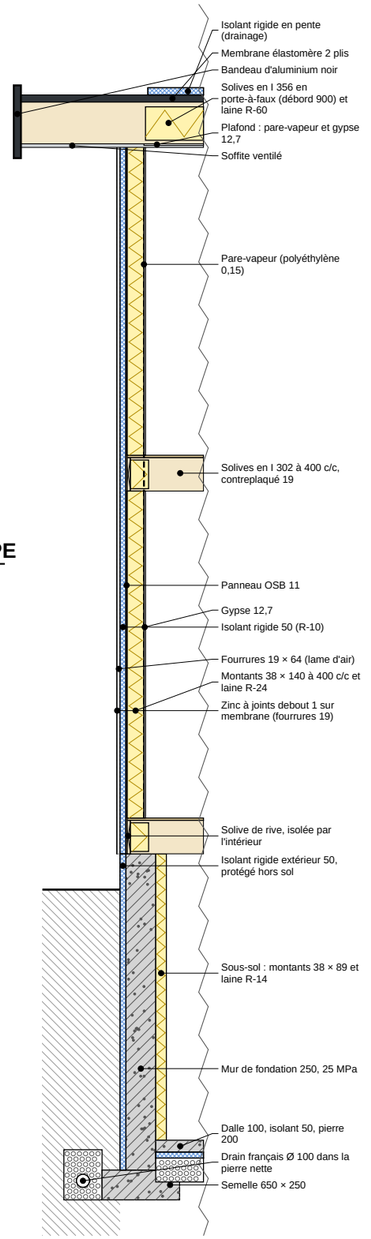


## 2 — COUPE DE MUR TYPE

Échelle 1:50

Pavillon de L'AVENIR
Centre de formation professionnelle

**PLAN D'EXERCICE**
**LECTURE DE PLANS**

PROJET

# MAISON UNIFAMILIALE
# DOSSIER 1

125, rue des Érables
Ville fictive (Québec)

### À OBSERVER

La coupe B est prise sur la ligne B des plans A-101 à A-103, en regardant vers le nord.

Repérer les trois niveaux : sous-sol, rez-de-chaussée, étage. Comparer avec A-201 et A-301.

Coupe de mur : de la semelle jusqu'au parapet, de l'extérieur vers l'intérieur.

### COMPOSITIONS

T1 — Toit monopente (débord 900) : membrane élastomère 2 plis, isolant rigide en pente, contreplaqué 19, solives en I 356, laine soufflée R-60, pare-vapeur, gypse 12,7.

M1 — Mur extérieur : zinc à joints debout (ou pierre, ou cèdre brûlé), fourrures 19, isolant rigide 50, OSB 11, montants 38 × 140 à 400 c/c, laine R-24, pare-vapeur, gypse 12,7.

M2 — Cloison : gypse 12,7 deux faces, montants 38 × 89 à 400 c/c (laine insonorisante autour des salles de bain).

P1 — Plancher : contreplaqué 19 collé-vissé, solives en I 302 à 400 c/c.

D1 — Dalle du sous-sol : béton 100, isolant rigide 50, pierre 200.

F1 — Fondation : mur de béton 250, isolant rigide 50 extérieur, semelle 650 × 250, drain français.

TITRE DE LA FEUILLE

**COUPE LONGITUDINALE, COUPE DE MUR ET MATÉRIAUX**

CONÇU PAR

**Jeremy, enseignant**

**DESSIN À DES FINS D'ENSEIGNEMENT — NE PAS UTILISER POUR LA CONSTRUCTION**

ÉCHELLE

**1:100 et 1:50**


DATE

Octobre 2026


FEUILLE

**A-302**

Dossier D1

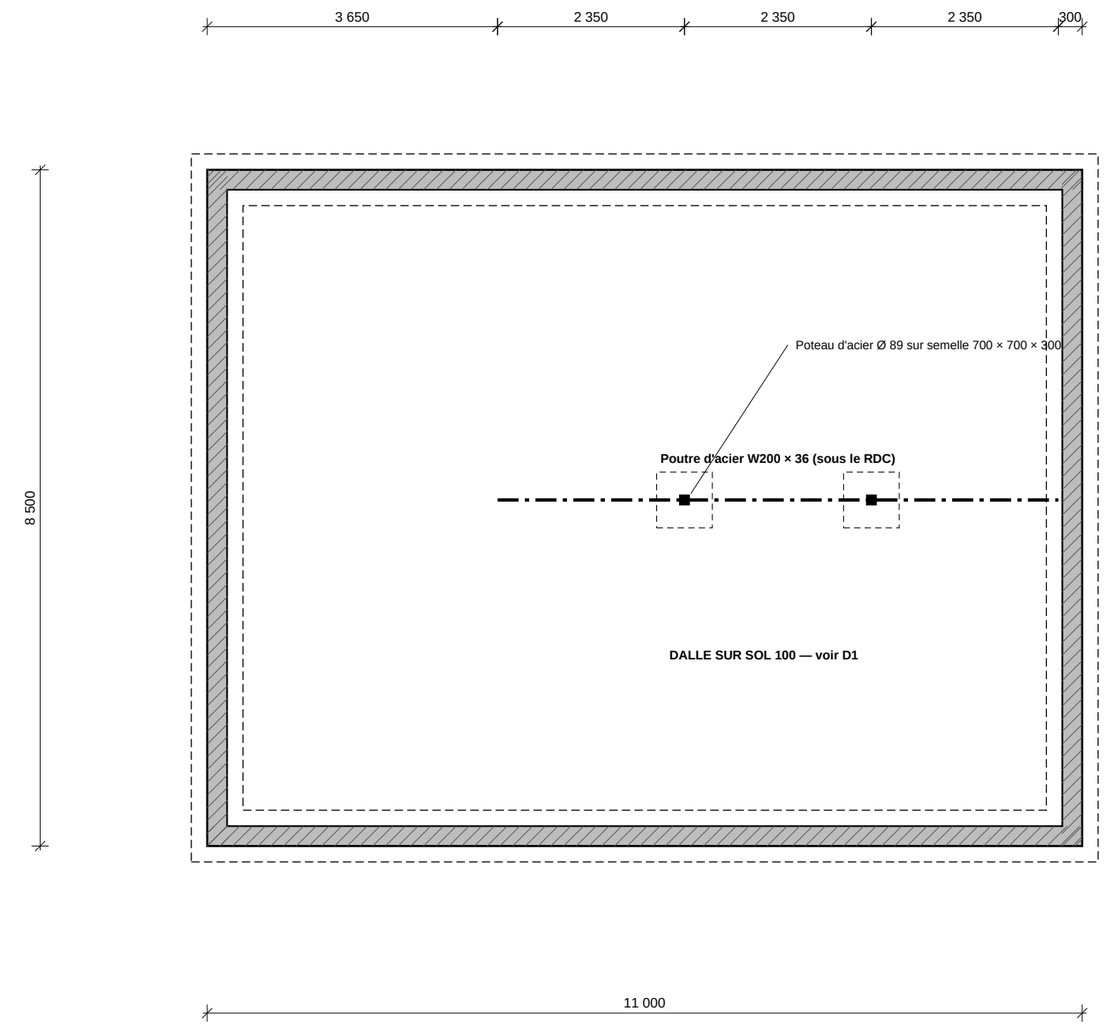


1 **PLAN DES FONDATIONS**
Échelle 1:75

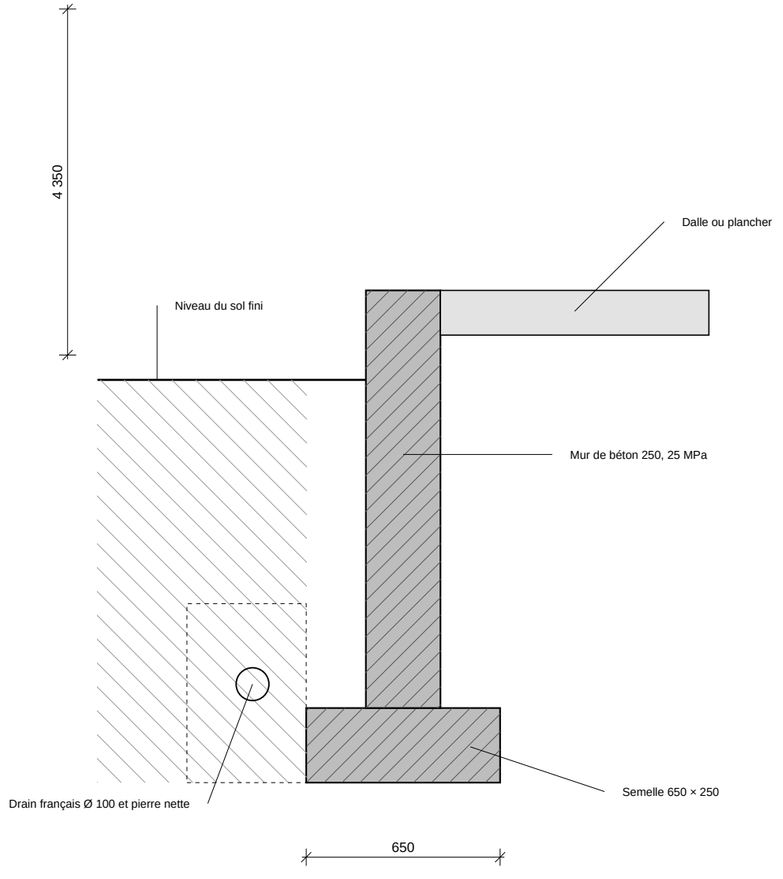


2 **DÉTAIL TYPE — SEMELLE ET MUR**
Échelle 1:20

Pavillon de L'AVENIR
Centre de formation professionnelle

**PLAN D'EXERCICE**
**LECTURE DE PLANS**

PROJET

## MAISON UNIFAMILIALE
## DOSSIER 1

125, rue des Érables
Ville fictive (Québec)

### NOTES DE STRUCTURE

Béton : 25 MPa à 28 jours, air entraîné 5 à 8 %.

Semelles à 1 600 mm minimum sous le sol fini (gel); ici le dessous est à 2 600.

Murs de fondation 250 armés, isolant rigide 50 à l'extérieur, membrane d'étanchéité, drain français.

Capacité portante présumée : 75 kPa. Faire valider par un ingénieur.

Solives du RDC appuyées sur la poutre d'acier.

### LÉGENDE

Poché hachuré : mur de fondation en béton coulé

Tirets : semelle (sous le niveau du plancher)

Carré plein : poteau · carré en tirets : semelle isolée

— · — Poutre porteuse

TITRE DE LA FEUILLE


**PLAN DES FONDATIONS ET DÉTAIL TYPE**

CONÇU PAR
**Jeremy, enseignant**
**DESSIN À DES FINS D'ENSEIGNEMENT — NE PAS UTILISER POUR LA CONSTRUCTION**

ÉCHELLE
**1:75 et 1:20**

DATE
Octobre 2026

FEUILLE
**S-101**
Dossier D1

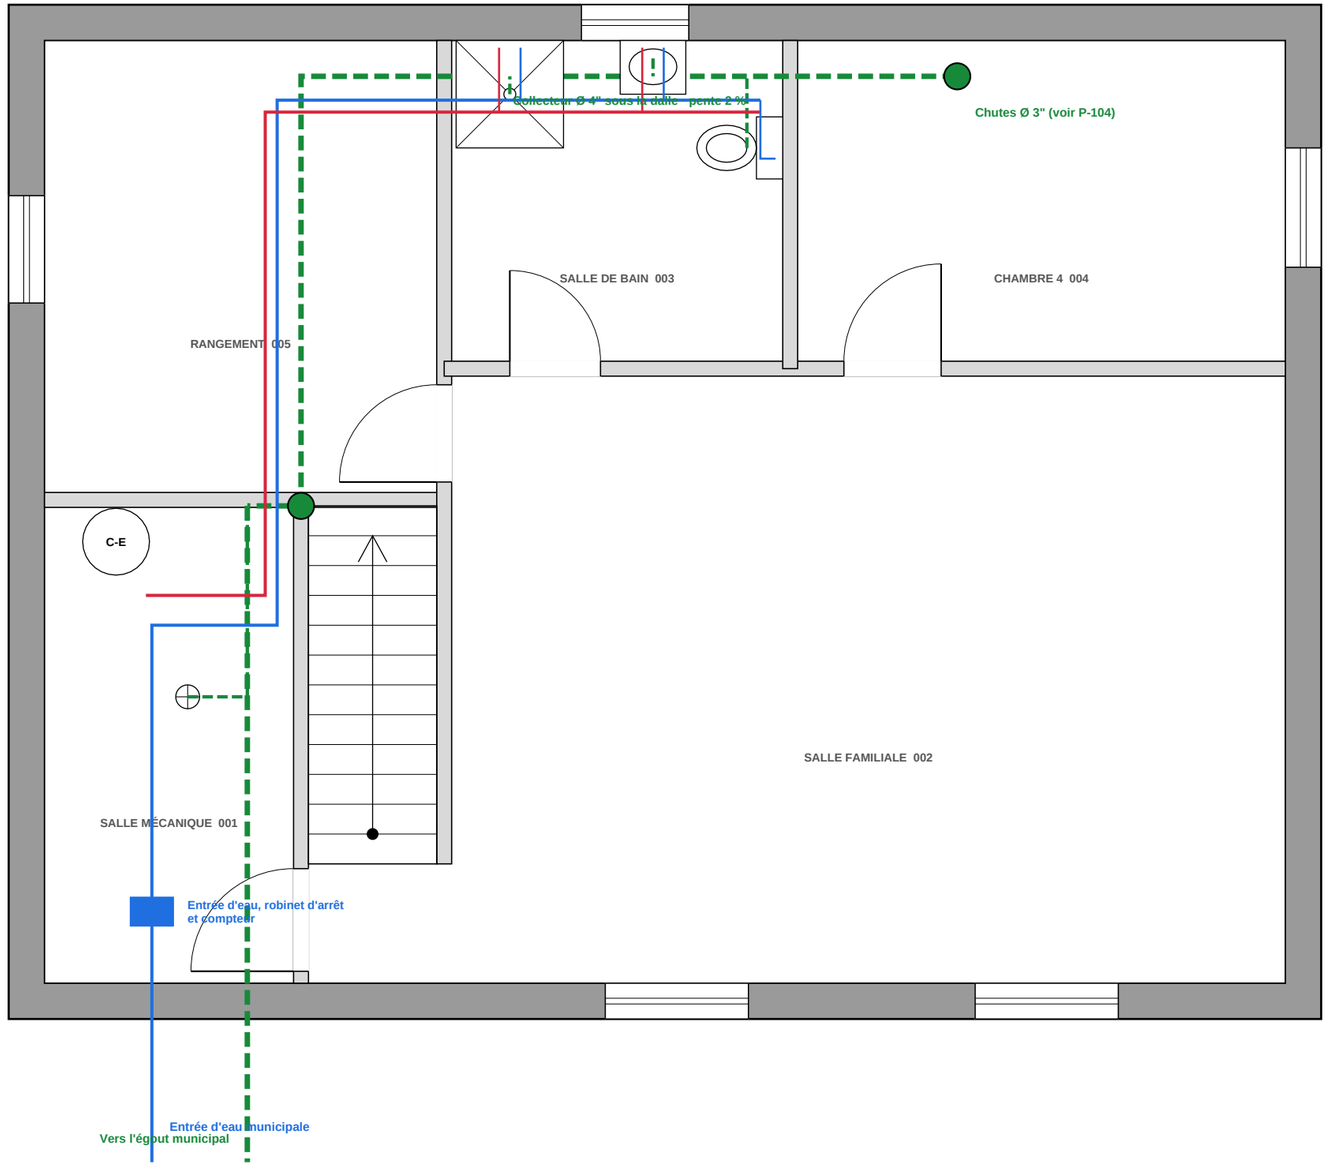


N

0 1 2 3 4 5 m

**1 PLAN DE PLOMBERIE**
Échelle 1:50

Pavillon de L'AVENIR
Centre de formation professionnelle

**PLAN D'EXERCICE**
**LECTURE DE PLANS**

PROJET

## MAISON UNIFAMILIALE
## DOSSIER 1

125, rue des Érables
Ville fictive (Québec)

### NOTES DE PLOMBERIE

Collecteur principal sous la dalle : ABS cédule 40, pente 2 %.

Clapet antiretour sur le collecteur, accessible (regard).

Chauffe-eau électrique 270 L : soupape T et P raccordée à 150 mm du sol.

Drain de plancher de la salle mécanique avec amorceur de siphon.

Les colonnes de chute montent jusqu'au toit (voir P-104).

### LÉGENDE

- Eau froide (EF)
- Eau chaude (EC)
- Drainage sanitaire
- Ventilation (évent)
- Colonne de chute

TITRE DE LA FEUILLE

**PLOMBERIE**
**SOUS-SOL**


CONÇU PAR
**Jeremy, enseignant**

**DESSIN À DES FINS D'ENSEIGNEMENT — NE PAS UTILISER POUR LA CONSTRUCTION**

ÉCHELLE
**1:50**

DATE
Octobre 2026

FEUILLE
**P-101**
Dossier D1

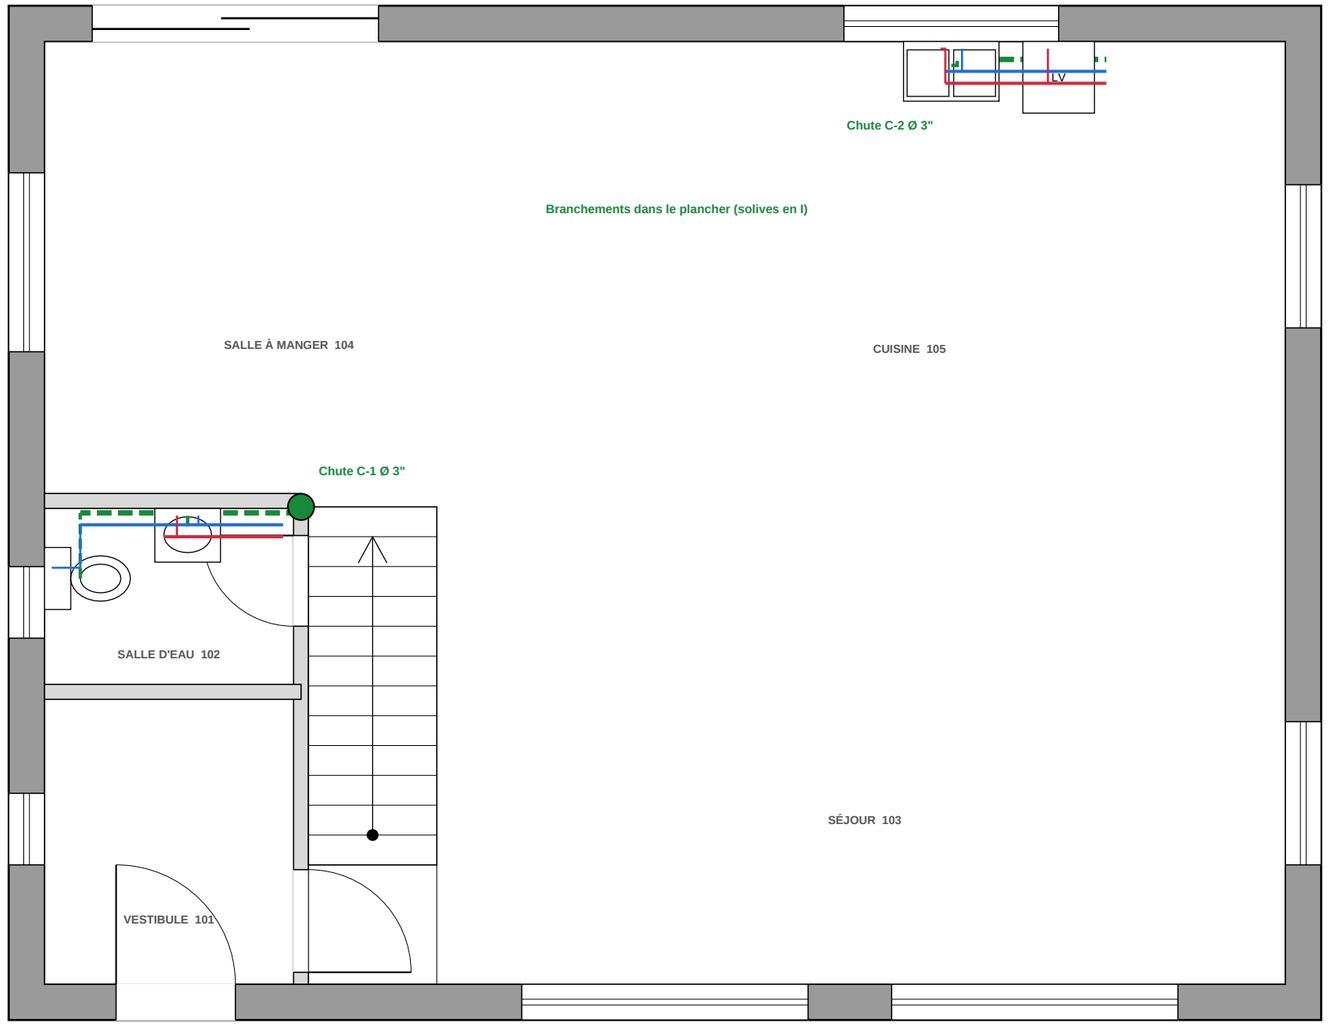


N

1 **PLAN DE PLOMBERIE**
Échelle 1:50

0 1 2 3 4 5 m

Pavillon de L'AVENIR
Centre de formation professionnelle

**PLAN D'EXERCICE**
**LECTURE DE PLANS**

PROJET

## MAISON UNIFAMILIALE
## DOSSIER 1

125, rue des Érables
Ville fictive (Québec)

### NOTES DE PLOMBERIE

Branchements dans l'épaisseur du plancher, vers les chutes C-1 et C-2.

Lave-vaisselle raccordé au siphon de l'évier (boucle anti-retour).

Eau : PEX, robinet d'arrêt sur chaque alimentation d'appareil.

### LÉGENDE

- Eau froide (EF)
- Eau chaude (EC)
- Drainage sanitaire
- Ventilation (évent)
- Colonne de chute

TITRE DE LA FEUILLE

**PLOMBERIE**
**REZ-DE-CHAUSSÉE**


CONÇU PAR
**Jeremy, enseignant**
**DESSIN À DES FINS D'ENSEIGNEMENT — NE PAS UTILISER POUR LA CONSTRUCTION**

ÉCHELLE
**1:50**

DATE
Octobre 2026

FEUILLE
**P-102**
Dossier D1

N

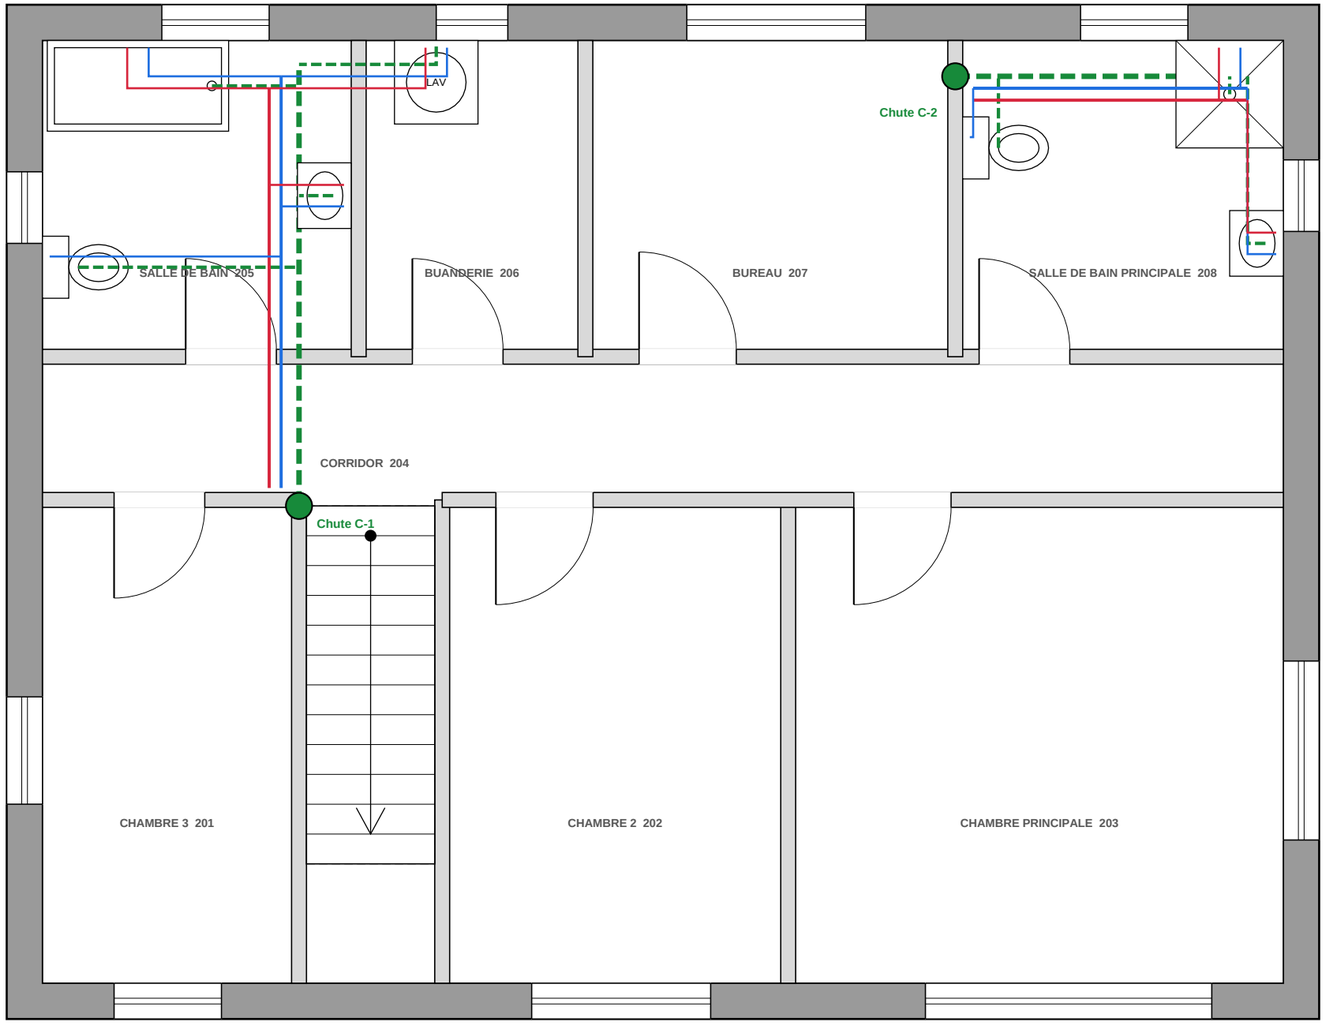


1 **PLAN DE PLOMBERIE**
Échelle 1:50

0 1 2 3 4 5 m

Pavillon de L'AVENIR
Centre de formation professionnelle

**PLAN D'EXERCICE**
**LECTURE DE PLANS**

PROJET

## MAISON UNIFAMILIALE
## DOSSIER 1

125, rue des Érables
Ville fictive (Québec)

### NOTES DE PLOMBERIE

Branchements dans le plancher de l'étage (solives en I percées selon le fabricant).

Laveuse : boîte de raccordement encastrée et bac de récupération.

Douche : drain linéaire, membrane d'étanchéité sous la céramique.

### LÉGENDE

- Eau froide (EF)
- Eau chaude (EC)
- Drainage sanitaire
- Ventilation (évent)
- Colonne de chute

TITRE DE LA FEUILLE

**PLOMBERIE**
**ÉTAGE**


CONÇU PAR
**Jeremy, enseignant**

**DESSIN À DES FINS D'ENSEIGNEMENT — NE PAS UTILISER POUR LA CONSTRUCTION**

ÉCHELLE
**1:50**

DATE
Octobre 2026

FEUILLE
**P-103**
Dossier D1

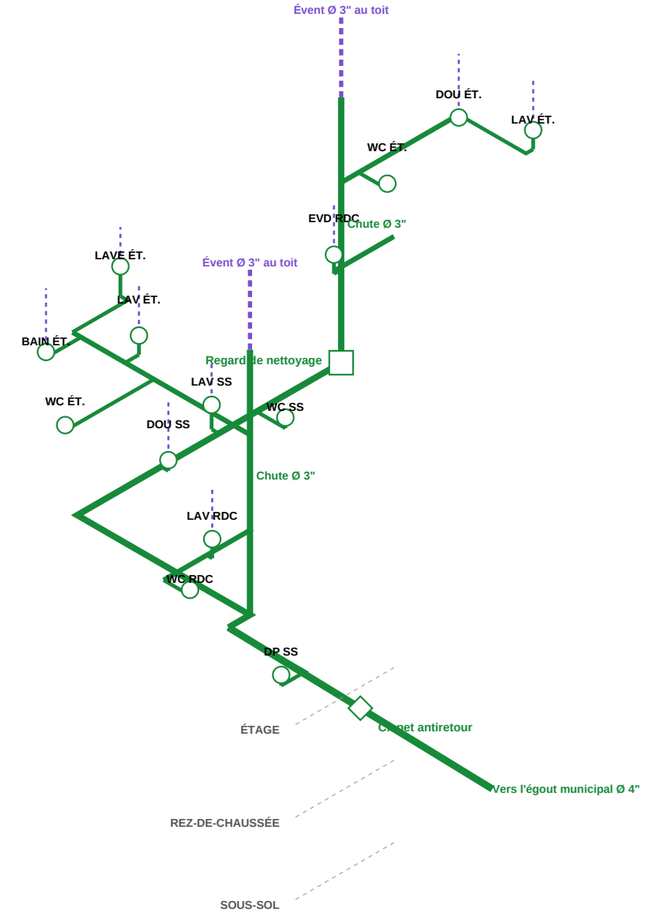


## 1 SCHÉMA ISOMÉTRIQUE — DRAINAGE ET VENTILATION (3 NIVEAUX)

Échelle sans échelle

### NOMENCLATURE DES APPAREILS SANITAIRES

| Code | Appareil | Qté | EF | EC | Drain | Évent | Unités |
|---|---|---|---|---|---|---|---|
| CE | Chauffe-eau électrique 270 L | 1 | 3/4" | 3/4" | — | — | 0 |
| DP | Drain de plancher | 1 | — | — | 3" | — | 2 |
| DOU | Douche | 2 | 1/2" | 1/2" | 2" | 1 1/2" | 3,0 |
| WC | Toilette (réservoir 6 L) | 4 | 1/2" | — | 3" | 2" | 16 |
| LAV | Lavabo | 4 | 1/2" | 1/2" | 1 1/4" | 1 1/4" | 4 |
| EVD | Évier de cuisine double | 1 | 1/2" | 1/2" | 1 1/2" | 1 1/4" | 1,5 |
| LV | Lave-vaisselle | 1 | — | 1/2" | (évier) | — | 1 |
| BAIN | Baignoire | 1 | 1/2" | 1/2" | 1 1/2" | 1 1/4" | 1,5 |
| LAVE | Laveuse (tuyau de rejet) | 1 | 1/2" | 1/2" | 2" | 1 1/2" | 1,5 |
| | TOTAL DES UNITÉS (charge hydraulique) | | | | | | 30,5 |

Pavillon de L'AVENIR
Centre de formation professionnelle

**PLAN D'EXERCICE**
**LECTURE DE PLANS**

PROJET

**MAISON UNIFAMILIALE**
**DOSSIER 1**

125, rue des Érables
Ville fictive (Québec)

### À OBSERVER

- Les deux colonnes de chute traversent les trois niveaux et se prolongent en évent au-dessus du toit.
- Aux étages, les branchements passent dans l'épaisseur du plancher (solives en I).
- Au sous-sol, le collecteur est sous la dalle; il sort vers la rue sous la semelle.
- Chaque appareil a son siphon et son évent. Pente minimale 1 : 50 (2 %).

TITRE DE LA FEUILLE

**SCHÉMA ISOMÉTRIQUE ET NOMENCLATURE DES APPAREILS**

CONÇU PAR

**Jeremy, enseignant**

**DESSIN À DES FINS D'ENSEIGNEMENT — NE PAS UTILISER POUR LA CONSTRUCTION**

ÉCHELLE

**Sans échelle**


DATE

Octobre 2026

FEUILLE

**P-104**

Dossier D1

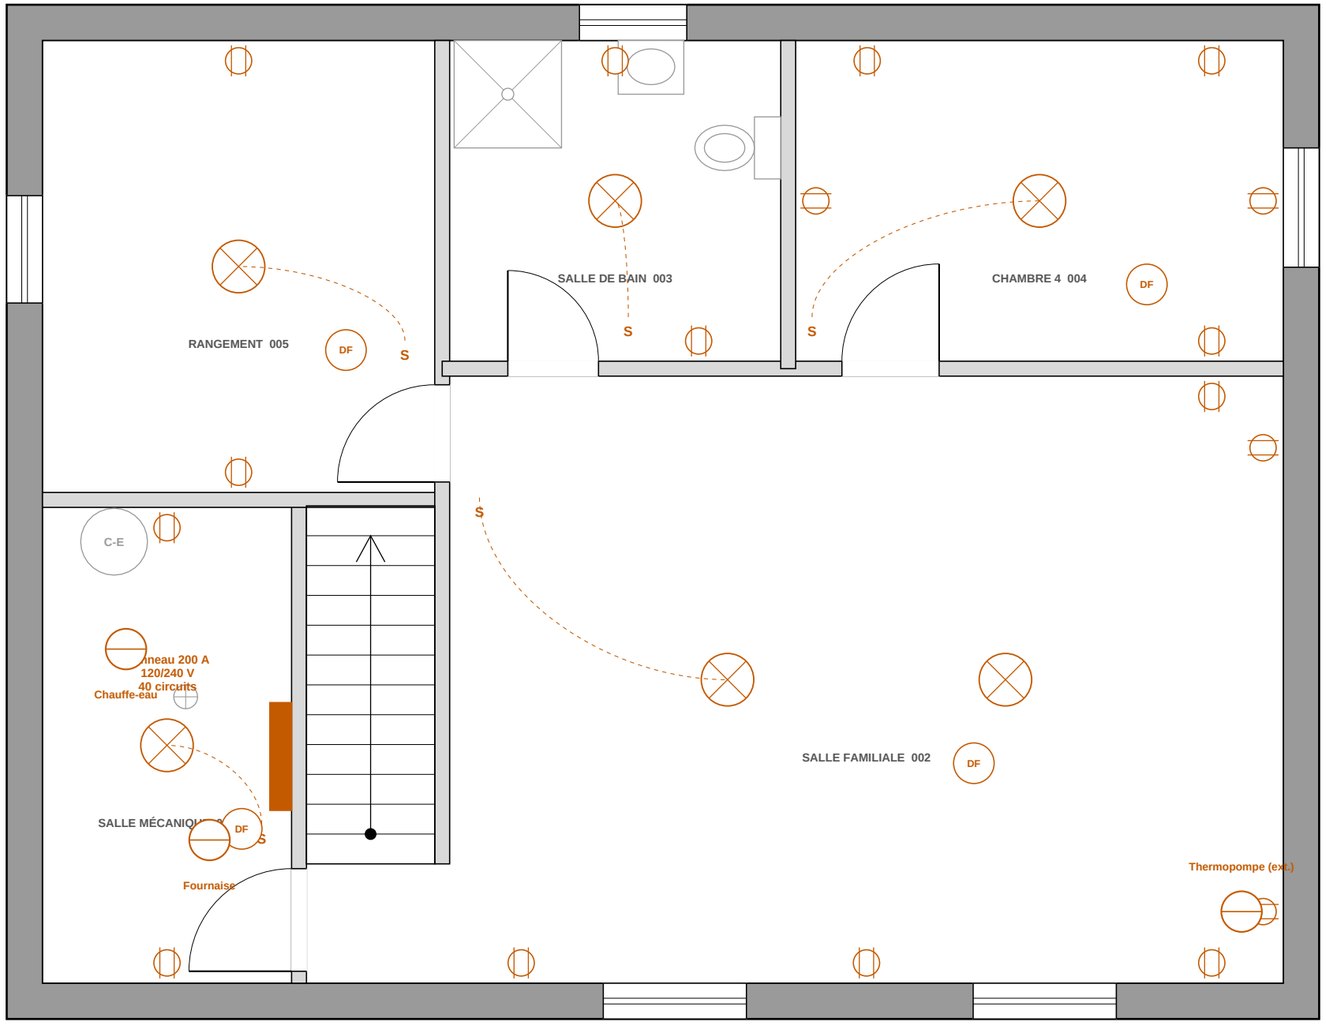


**1 PLAN D'ÉLECTRICITÉ**
Échelle 1:50

Pavillon de L'AVENIR
Centre de formation professionnelle

**PLAN D'EXERCICE**
**LECTURE DE PLANS**

PROJET

## MAISON UNIFAMILIALE
## DOSSIER 1

125, rue des Érables
Ville fictive (Québec)

### NOTES D'ÉLECTRICITÉ

Installation selon le Code de construction du Québec, chapitre V — Électricité.

Entrée électrique souterraine jusqu'au panneau de la salle mécanique.

Avertisseurs de fumée et de CO reliés entre eux à chaque niveau.

Prises de la salle de bain : protection DDFT.

### LÉGENDE

- Prise de courant double 15 A
- Luminaire au plafond
- S — Interrupteur unipolaire
- DF — Avertisseur de fumée relié
- Prise 240 V ou appareil dédié
- Panneau de distribution

### CIRCUITS (EXTRAIT)

| No | Usage | Charge | Disj. |
|---|---|---|---|
| 1 | Prises et éclairage — Salle mécani | 15 A | 1 × 15 A |
| 2 | Prises et éclairage — Salle famili | 15 A | 1 × 15 A |
| 3 | Prises et éclairage — Salle de bai | 15 A | 1 × 15 A |
| 4 | Prises et éclairage — Chambre 4 | 15 A | 1 × 15 A |
| 5 | Prises et éclairage — Rangement | 15 A | 1 × 15 A |
| 6 | Chauffe-eau | 30 A 240 V | 2 × 30 A |
| 7 | Fournaise | 100 A 240 V | 2 × 100 A |
| 8 | Thermopompe (ext.) | 30 A 240 V | 2 × 30 A |

TITRE DE LA FEUILLE

**ÉLECTRICITÉ**
**SOUS-SOL**


CONÇU PAR
**Jeremy, enseignant**

**DESSIN À DES FINS D'ENSEIGNEMENT —**
**NE PAS UTILISER POUR LA CONSTRUCTION**

ÉCHELLE
**1:50**

DATE
Octobre 2026

FEUILLE
**E-101**
Dossier D1

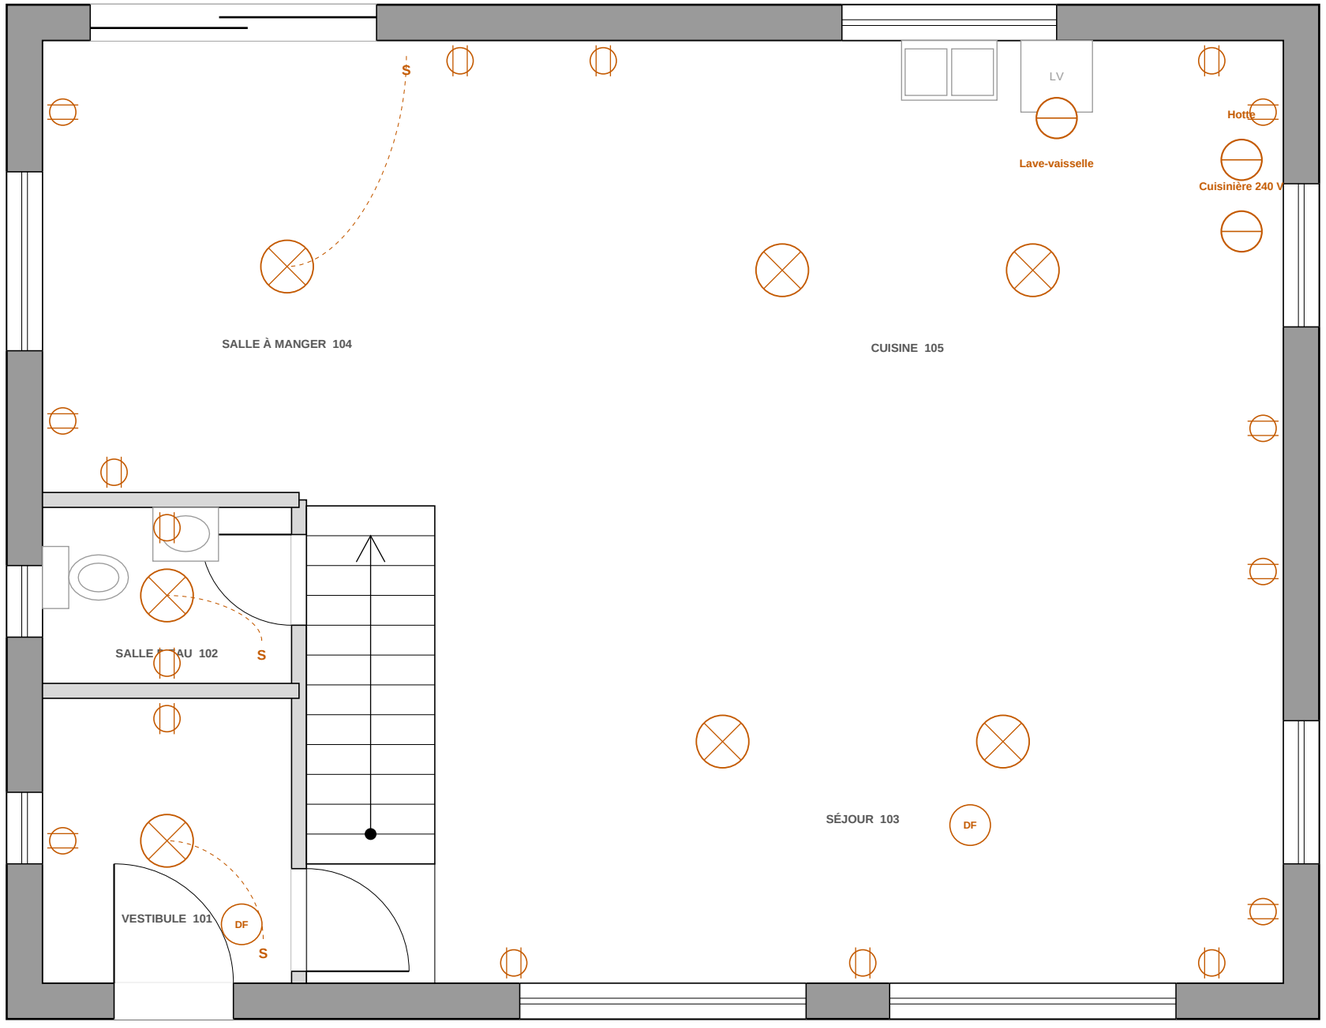


N

Pavillon de L'AVENIR
Centre de formation professionnelle

**PLAN D'EXERCICE**
**LECTURE DE PLANS**

PROJET

## MAISON UNIFAMILIALE
## DOSSIER 1

125, rue des Érables
Ville fictive (Québec)

### NOTES D'ÉLECTRICITÉ

Prises du comptoir : circuits de 20 A avec prises T, protection DDFT près de l'évier.

Éclairage encastré DEL au séjour et à la cuisine.

Aucun point le long d'un mur à plus de 1,8 m d'une prise.

### LÉGENDE

- Prise de courant double 15 A
- Luminaire au plafond
- S — Interrupteur unipolaire
- DF — Avertisseur de fumée relié
- Prise 240 V ou appareil dédié
- Panneau de distribution

### CIRCUITS (EXTRAIT)

| No | Usage | Charge | Disj. |
|---|---|---|---|
| 1 | Prises et éclairage — Vestibule | 15 A | 1 × 15 A |
| 2 | Prises et éclairage — Salle d'eau | 15 A | 1 × 15 A |
| 3 | Prises et éclairage — Séjour | 15 A | 1 × 15 A |
| 4 | Prises et éclairage — Salle à mang | 15 A | 1 × 15 A |
| 5 | Prises et éclairage — Cuisine | 15 A | 1 × 15 A |
| 6 | Cuisinière 240 V | 40 A 240 V | 2 × 40 A |
| 7 | Lave-vaisselle | 15 A 120 V | 1 × 15 A |
| 8 | Hotte | 15 A 120 V | 1 × 15 A |

TITRE DE LA FEUILLE

**ÉLECTRICITÉ**
**REZ-DE-CHAUSSÉE**

CONÇU PAR
**Jeremy, enseignant**


**DESSIN À DES FINS D'ENSEIGNEMENT — NE PAS UTILISER POUR LA CONSTRUCTION**

ÉCHELLE
**1:50**

DATE
Octobre 2026

FEUILLE
**E-102**
Dossier D1

1 **PLAN D'ÉLECTRICITÉ**
Échelle 1:50

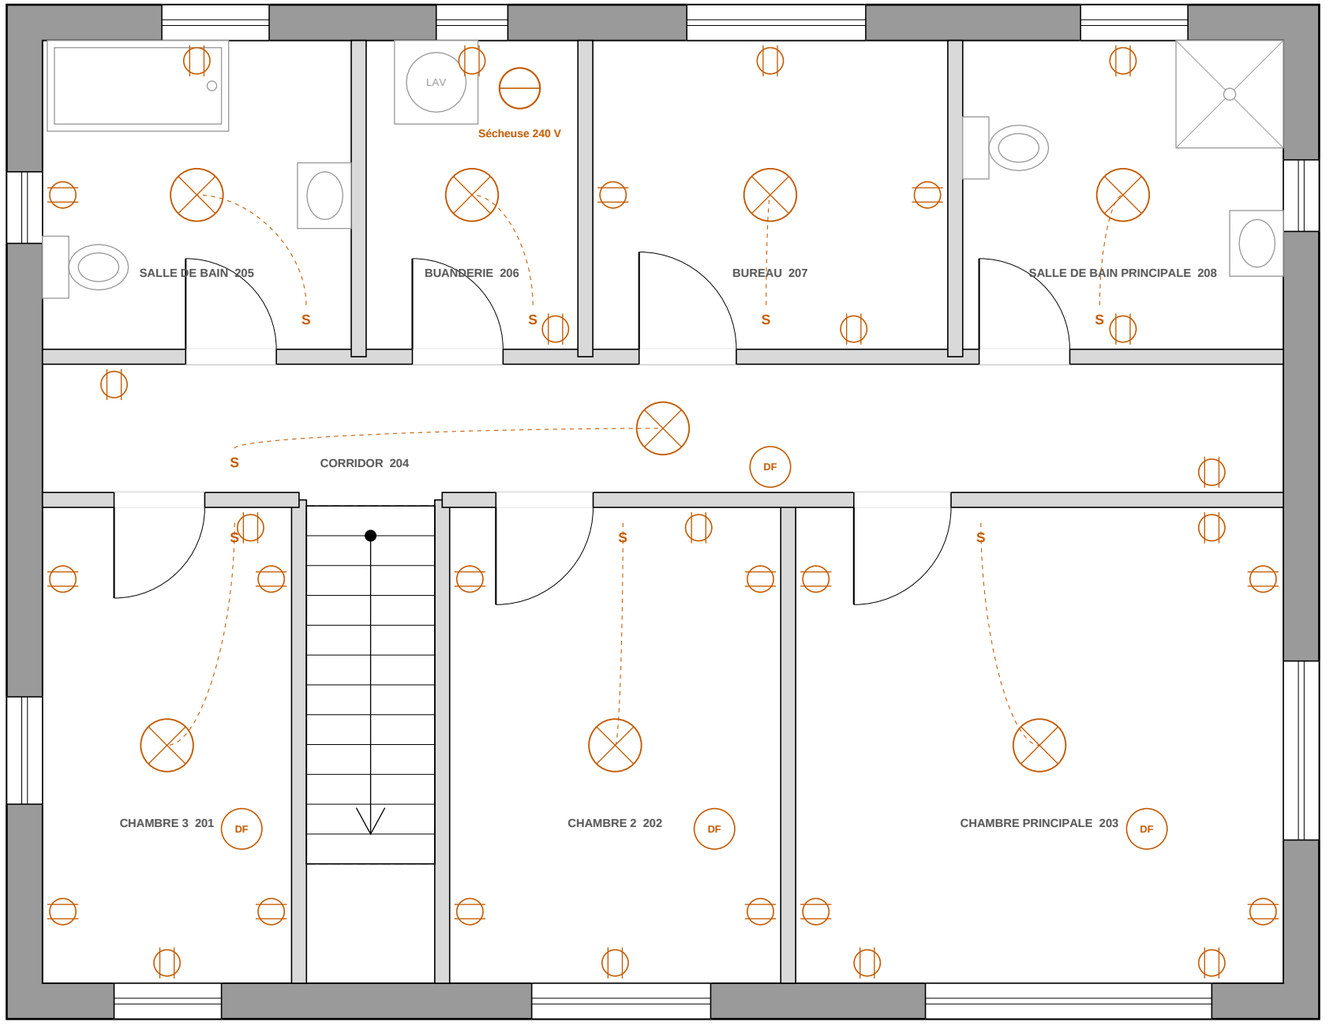


N

**1** **PLAN D'ÉLECTRICITÉ**
Échelle 1:50

Pavillon de L'AVENIR
Centre de formation professionnelle

**PLAN D'EXERCICE**
**LECTURE DE PLANS**

PROJET

## MAISON UNIFAMILIALE
## DOSSIER 1

125, rue des Érables
Ville fictive (Québec)

### NOTES D'ÉLECTRICITÉ

Chambres : prises protégées par disjoncteur anti-arcs (AFCI).

Avertisseurs de fumée et de CO dans le corridor et dans chaque chambre, reliés entre eux.

Ventilateurs des salles de bain sur minuterie (reliés au VRC).

### LÉGENDE

- Prise de courant double 15 A
- Luminaire au plafond
- S — Interrupteur unipolaire
- DF — Avertisseur de fumée relié
- Prise 240 V ou appareil dédié
- Panneau de distribution

### CIRCUITS (EXTRAIT)

| No | Usage | Charge | Disj. |
|---|---|---|---|
| 1 | Prises et éclairage — Chambre 3 | 15 A | 1 × 15 A |
| 2 | Prises et éclairage — Chambre 2 | 15 A | 1 × 15 A |
| 3 | Prises et éclairage — Chambre prin | 15 A | 1 × 15 A |
| 4 | Prises et éclairage — Corridor | 15 A | 1 × 15 A |
| 5 | Prises et éclairage — Salle de bai | 15 A | 1 × 15 A |
| 6 | Prises et éclairage — Buanderie | 15 A | 1 × 15 A |
| 7 | Prises et éclairage — Bureau | 15 A | 1 × 15 A |
| 8 | Prises et éclairage — Salle de bai | 15 A | 1 × 15 A |
| 9 | Sécheuse 240 V | 30 A 240 V | 2 × 30 A |

TITRE DE LA FEUILLE

**ÉLECTRICITÉ**
**ÉTAGE**

CONÇU PAR
**Jeremy, enseignant**


**DESSIN À DES FINS D'ENSEIGNEMENT — NE PAS UTILISER POUR LA CONSTRUCTION**

ÉCHELLE
**1:50**

DATE
Octobre 2026

FEUILLE
**E-103**
Dossier D1

N

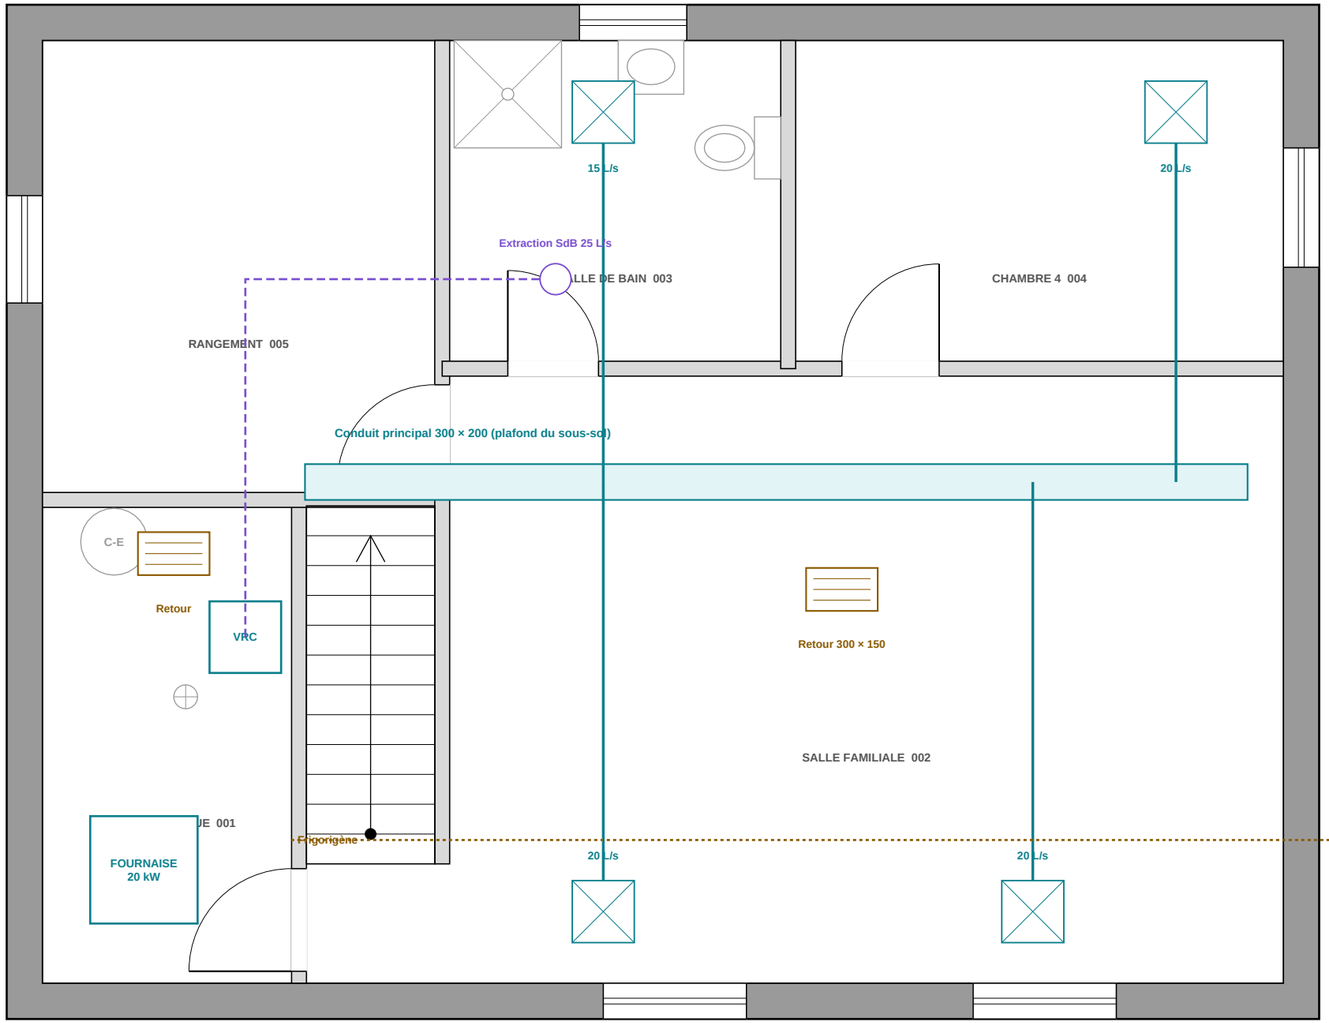


## 1 PLAN DE CHAUFFAGE ET VENTILATION

Échelle 1:50

Pavillon de L'AVENIR
Centre de formation professionnelle

**PLAN D'EXERCICE**
**LECTURE DE PLANS**

PROJET

# MAISON UNIFAMILIALE
# DOSSIER 1

125, rue des Érables
Ville fictive (Québec)

### NOTES CVCA

Fournaise électrique 20 kW et thermopompe centrale de 2 tonnes.

Conduits d'acier galvanisé dans le plafond du sous-sol, colonnes vers les étages (voir M-102, M-103).

VRC : extraction des salles de bain et de la cuisine, air neuf au retour de la fournaise.

Débits en litres par seconde (L/s).

### LÉGENDE

Conduit d'alimentation

Carré avec X : diffuseur d'alimentation (L/s)

Rectangle ligné : grille de retour

Conduit d'évacuation (VRC)

TITRE DE LA FEUILLE

## CHAUFFAGE ET VENTILATION SOUS-SOL

CONÇU PAR

**Jeremy, enseignant**

DESSIN À DES FINS D'ENSEIGNEMENT —
NE PAS UTILISER POUR LA CONSTRUCTION

ÉCHELLE

**1:50**


DATE

Octobre 2026

FEUILLE

**M-101**

Dossier D1

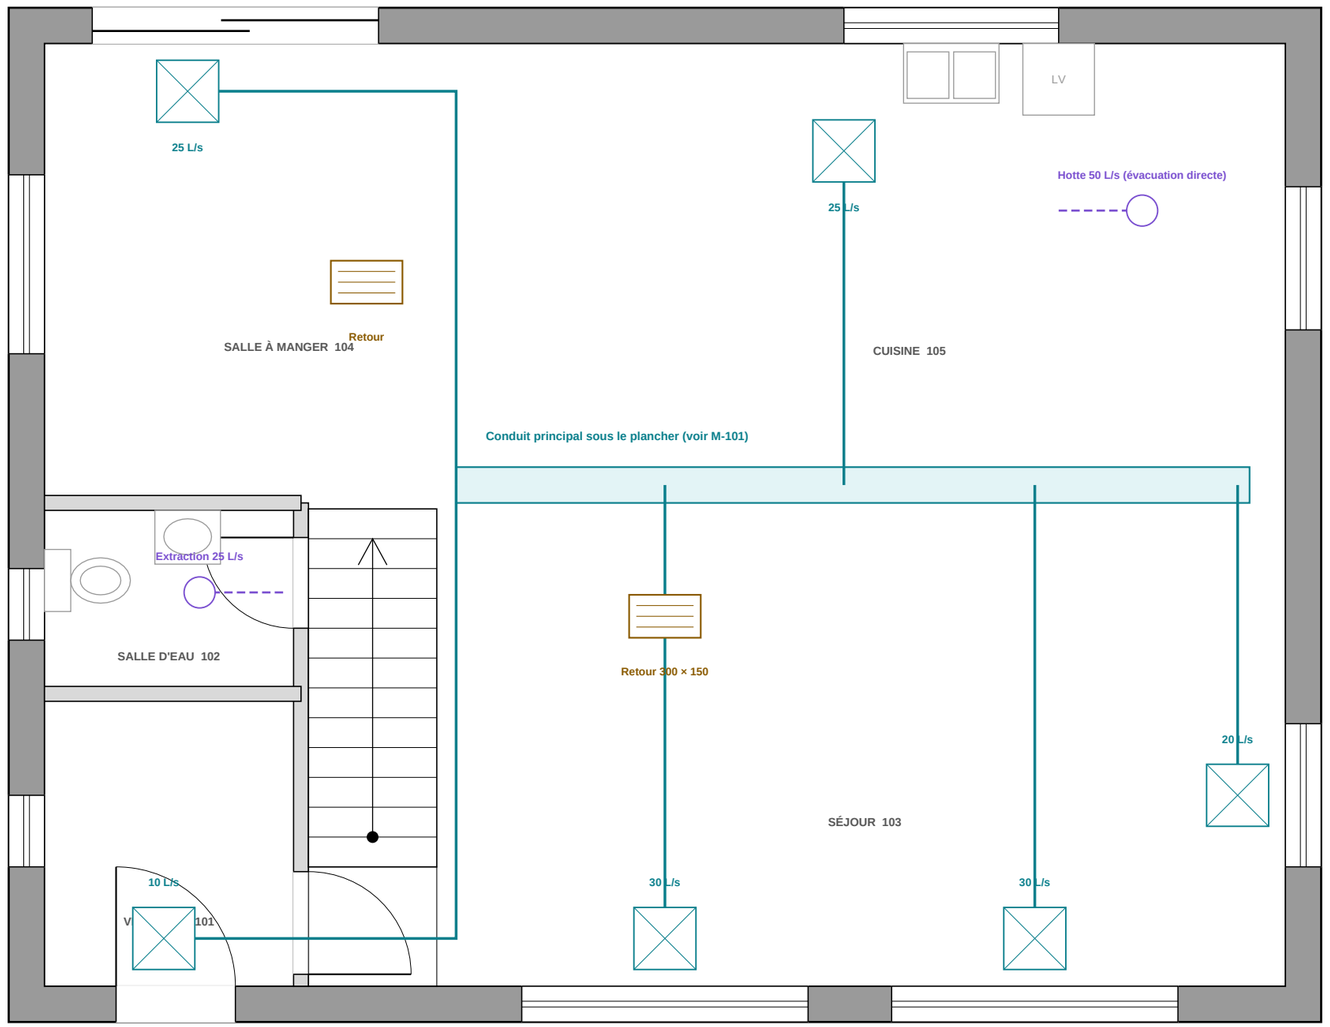


**1** **PLAN DE CHAUFFAGE ET VENTILATION**
Échelle 1:50

Pavillon de L'AVENIR
Centre de formation professionnelle

**PLAN D'EXERCICE**
**LECTURE DE PLANS**

PROJET

## MAISON UNIFAMILIALE
## DOSSIER 1

125, rue des Érables
Ville fictive (Québec)

### NOTES CVCA

Diffuseurs au plancher, sous les grandes fenêtres.

Retours au mur intérieur, ramenés au sous-sol.

Hotte de cuisinière évacuée directement à l'extérieur.

### LÉGENDE

Conduit d'alimentation

Carré avec X : diffuseur d'alimentation (L/s)

Rectangle ligné : grille de retour

Conduit d'évacuation (VRC)

TITRE DE LA FEUILLE

## CHAUFFAGE ET VENTILATION
## REZ-DE-CHAUSSÉE

CONÇU PAR
**Jeremy, enseignant**


**DESSIN À DES FINS D'ENSEIGNEMENT — NE PAS UTILISER POUR LA CONSTRUCTION**

ÉCHELLE
**1:50**

DATE
Octobre 2026

FEUILLE
**M-102**
Dossier D1

N

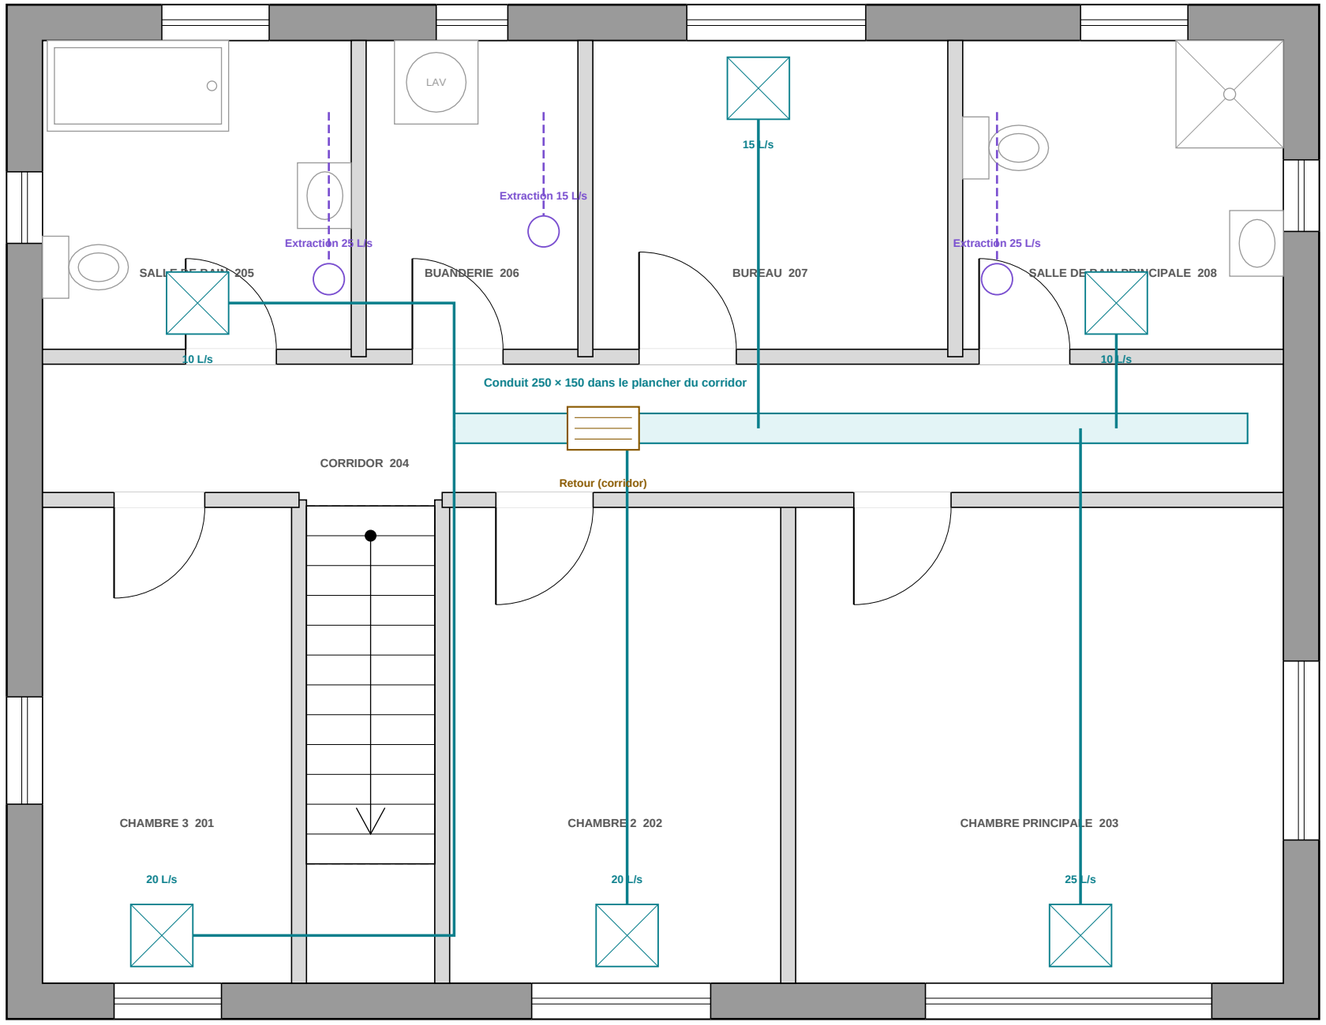


**1** **PLAN DE CHAUFFAGE ET VENTILATION**
Échelle 1:50

Pavillon de L'AVENIR
Centre de formation professionnelle

**PLAN D'EXERCICE**
**LECTURE DE PLANS**

PROJET

## MAISON UNIFAMILIALE
## DOSSIER 1

125, rue des Érables
Ville fictive (Québec)

### NOTES CVCA

Colonne d'alimentation montant du sous-sol dans le mur de l'escalier.

Un diffuseur sous chaque fenêtre de chambre.

VRC : extraction des deux salles de bain et de la buanderie.

### LÉGENDE

Conduit d'alimentation

Carré avec X : diffuseur d'alimentation (L/s)

Rectangle ligné : grille de retour

Conduit d'évacuation (VRC)

TITRE DE LA FEUILLE

**CHAUFFAGE ET VENTILATION**
**ÉTAGE**

CONÇU PAR

**Jeremy, enseignant**

**DESSIN À DES FINS D'ENSEIGNEMENT — NE PAS UTILISER POUR LA CONSTRUCTION**

ÉCHELLE

**1:50**

DATE

Octobre 2026

FEUILLE

**M-103**

Dossier D1