MAISON UNIFAMILIALE

DOSSIER 1
125, rue des Érables
Ville fictive (Québec)

Conçu par Jeremy, enseignant

Maison de plain-pied à ossature de bois, sur vide sanitaire, avec toit à deux versants. Trois locaux de vie, deux chambres, une salle de bain et une salle mécanique. Chauffage par air pulsé (fournaise électrique et thermopompe) et ventilation par VRC.

LISTE DES FEUILLES

Feuille	Titre
000	Page de garde et liste des feuilles
A-100	Plan d'implantation et de site
A-101	Plan du rez-de-chaussée
A-201	Élévations
A-301	Coupe transversale et nomenclatures
A-302	Coupe longitudinale, coupe de mur et matériaux
S-101	Plan des fondations et détail type
P-101	Plan de plomberie
P-102	Schéma isométrique et nomenclature des appareils
E-101	Plan d'électricité
M-101	Plan de chauffage, ventilation et climatisation

DONNÉES DU BÂTIMENT

Élément	Valeur
Usage	Habitation unifamiliale
Étages	1 (plain-pied)
Superficie brute	104,9 m²
Structure	Ossature de bois, fondation de béton
Toiture	Deux versants, pente 5 : 12
Chauffage	Air pulsé + thermopompe
Eau et égout	Réseaux municipaux
Lot	18 000 × 33 000

Pavillon de L'AVENIR
Centre de formation professionnelle

PLAN D'EXERCICE
LECTURE DE PLANS

PROJET

MAISON UNIFAMILIALE
DOSSIER 1

125, rue des Érables
Ville fictive (Québec)

UTILISATION EN CLASSE

Ce dossier sert à apprendre à lire des plans : repérer les feuilles, les échelles, les symboles, les cotes et les liens entre les disciplines.

Les renvois (bulles de coupe, types de fenêtres, numéros de portes) relient les feuilles entre elles.

Bâtiment fictif. Les valeurs sont plausibles mais non vérifiées pour la construction.

TITRE DE LA FEUILLE

PAGE DE GARDE
ET LISTE DES FEUILLES

CONÇU PAR
Jeremy, enseignant


DESSIN À DES FINS D'ENSEIGNEMENT — NE PAS UTILISER POUR LA CONSTRUCTION

ÉCHELLE
—

FEUILLE
000
Dossier D1

DATE
Octobre 2026

LOT 4 123 456 · SUPERFICIE 594,0 m²

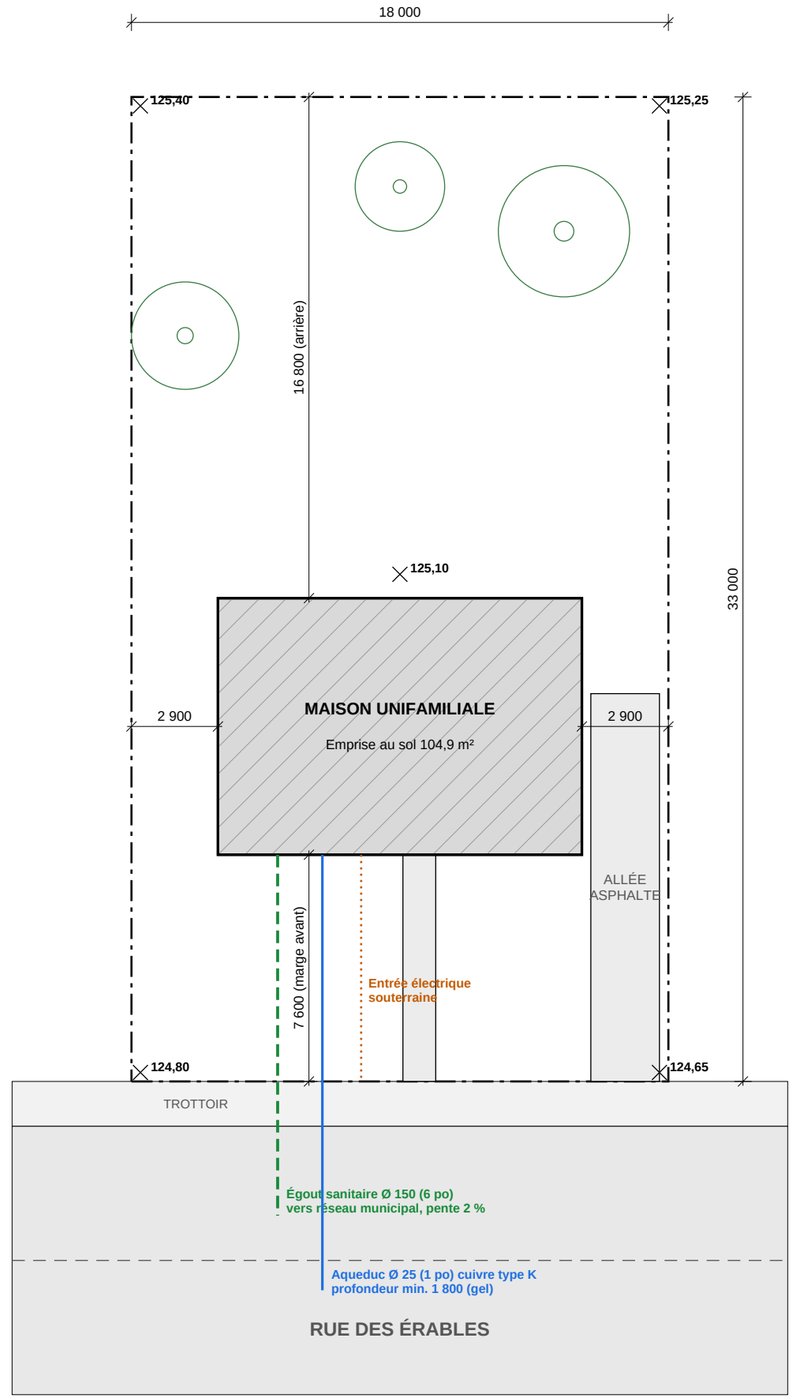

N

0 2 4 6 8 10 m

1 **PLAN D'IMPLANTATION**
Échelle 1:200

Pavillon de L'AVENIR
Centre de formation professionnelle

PLAN D'EXERCICE
LECTURE DE PLANS

PROJET

MAISON UNIFAMILIALE
DOSSIER 1

125, rue des Érables
Ville fictive (Québec)

NOTES D'IMPLANTATION

Implantation à confirmer par un arpenteur-géomètre.

Marge avant minimale : 7,5 m. Marges latérales : 2,0 m.

Niveaux du terrain en mètres (altitude géodésique).

Pente du terrain fini : 2 % minimum en s'éloignant du bâtiment.

LÉGENDE

— · — Limite de lot

Hachures : emprise du bâtiment

Croix : niveau du terrain (m, géodésique)

Bleu : aqueduc · Vert pointillé : égout sanitaire

Orange pointillé : entrée électrique

TITRE DE LA FEUILLE


PLAN D'IMPLANTATION ET DE SITE

CONÇU PAR
Jeremy, enseignant
DESSIN À DES FINS D'ENSEIGNEMENT — NE PAS UTILISER POUR LA CONSTRUCTION

ÉCHELLE
1:200

DATE
Octobre 2026

FEUILLE
A-100
Dossier D1

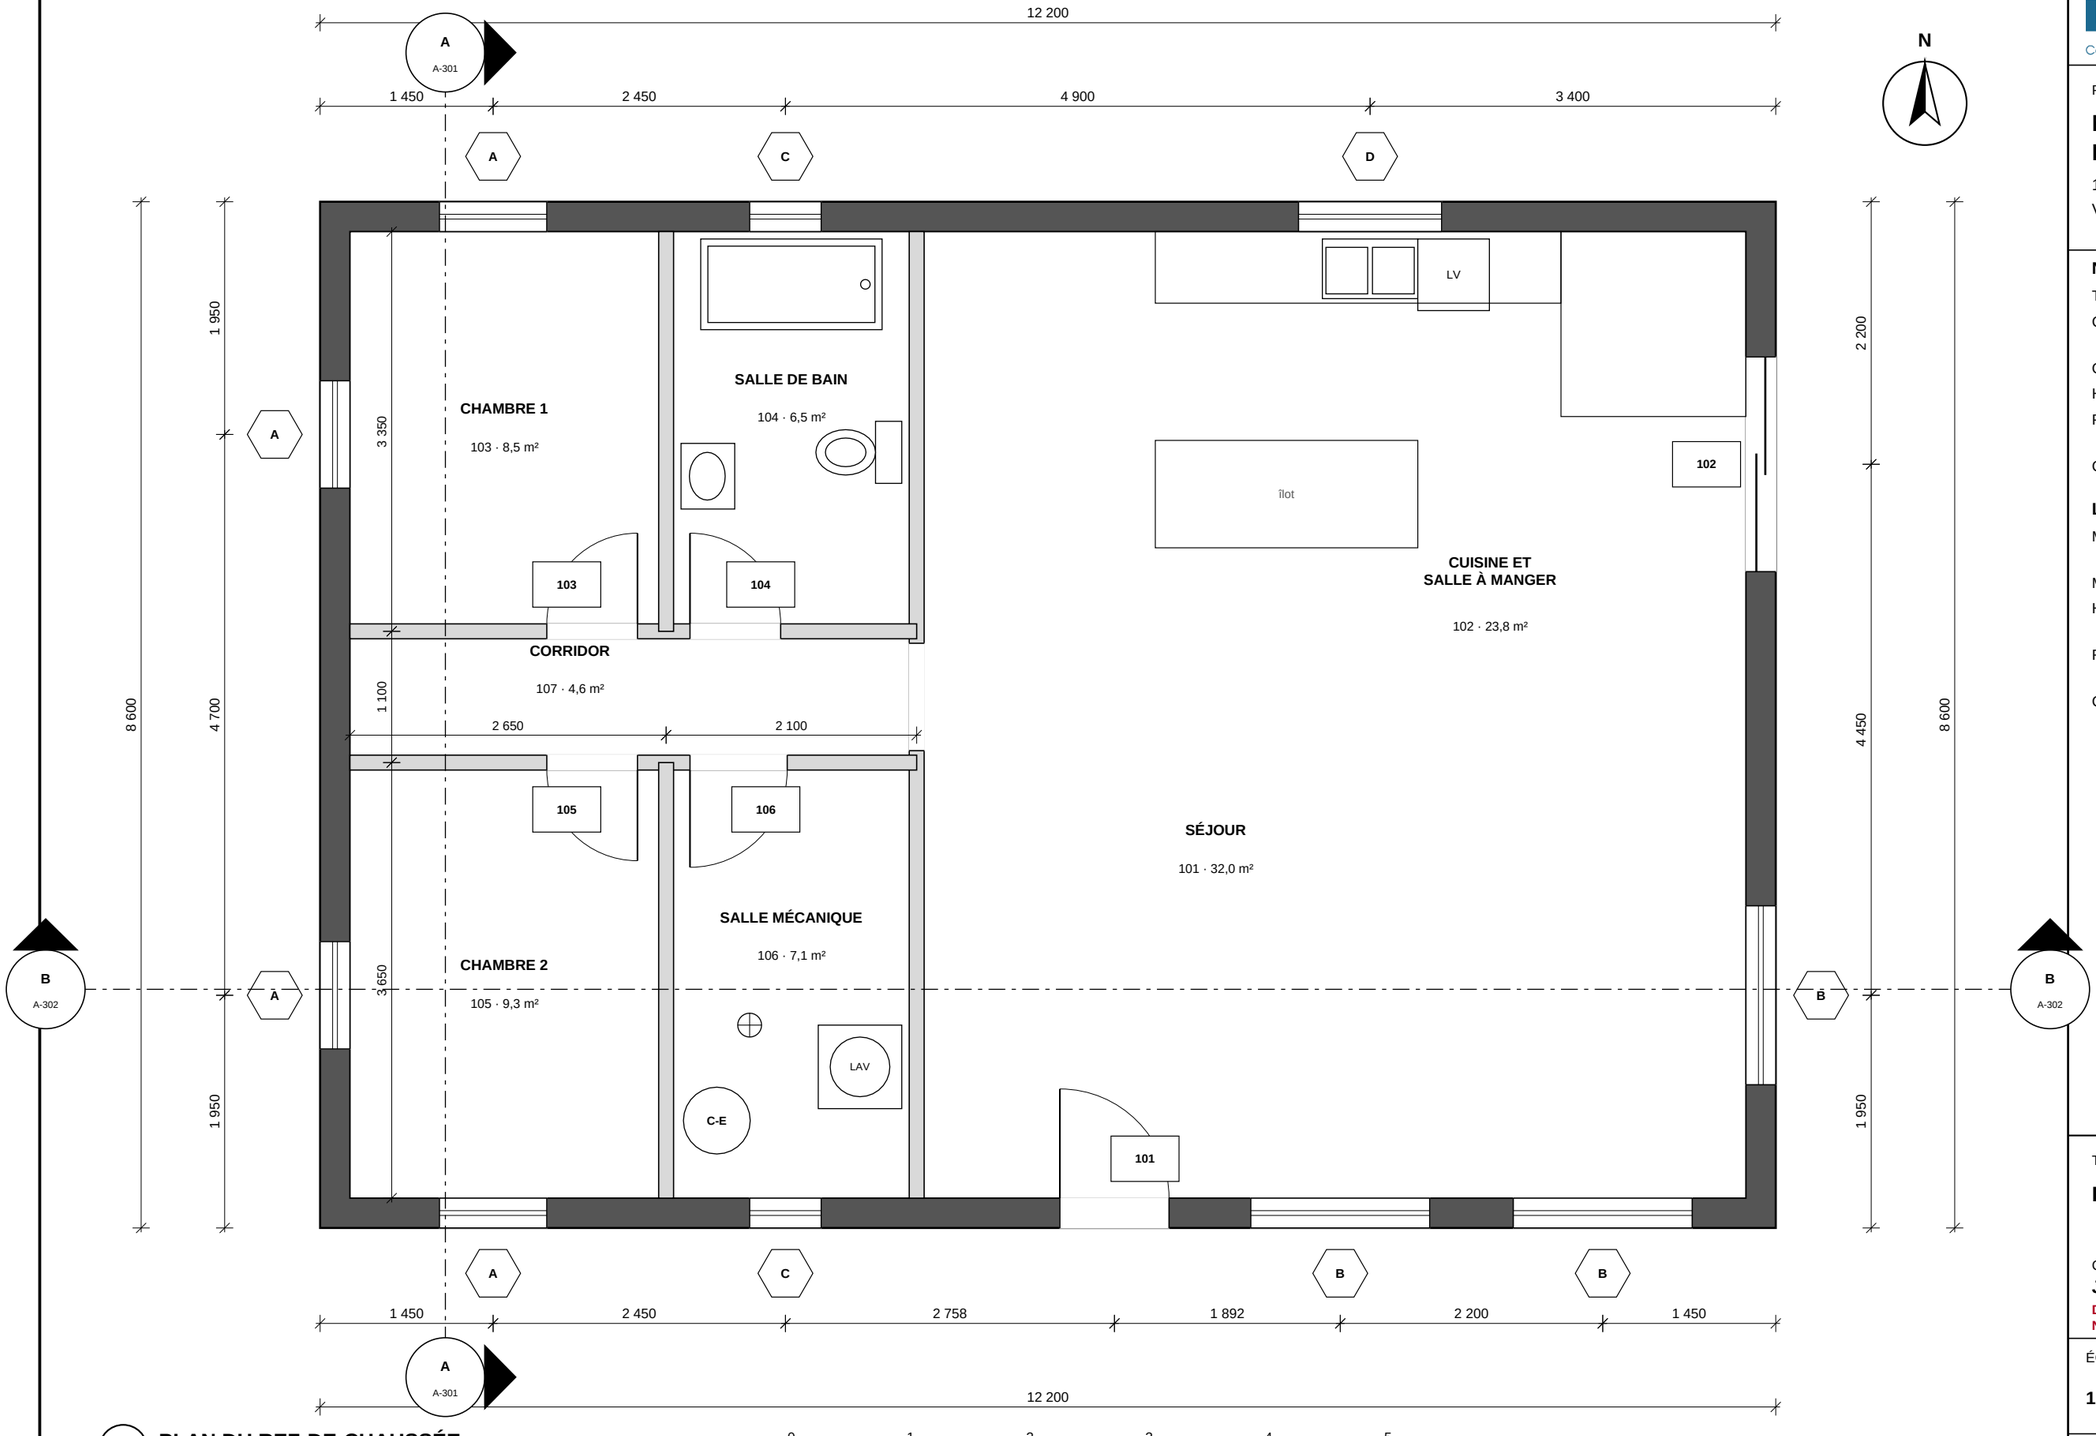

1 **PLAN DU REZ-DE-CHAUSSÉE**
Échelle 1:50

Pavillon de L'AVENIR
Centre de formation professionnelle

PLAN D'EXERCICE
LECTURE DE PLANS

PROJET

MAISON UNIFAMILIALE
DOSSIER 1

125, rue des Érables
Ville fictive (Québec)

NOTES GÉNÉRALES

Toutes les cotes sont en millimètres.

Cotes extérieures prises à la face extérieure du revêtement intermédiaire.

Ouvertures cotées à leur axe.

Hauteur libre sous plafond : 2 440 mm.

Portes intérieures : voir nomenclature, feuille A-301.

Comptoirs de cuisine : profondeur 600, hauteur 915.

LÉGENDE

Mur extérieur (poché foncé) : voir composition M1, feuille A-301

Mur intérieur (poché pâle) : voir composition M2

Hexagone : type de fenêtre (voir nomenclature, A-301)

Rectangle : numéro de porte (voir nomenclature, A-301)

Cotes en millimètres, aux faces extérieures du revêtement intermédiaire et aux axes des ouvertures

TITRE DE LA FEUILLE


PLAN DU REZ-DE-CHAUSSÉE

CONÇU PAR
Jeremy, enseignant
DESSIN À DES FINS D'ENSEIGNEMENT —
NE PAS UTILISER POUR LA CONSTRUCTION


ÉCHELLE
1:50

DATE
Octobre 2026


FEUILLE
A-101
Dossier D1

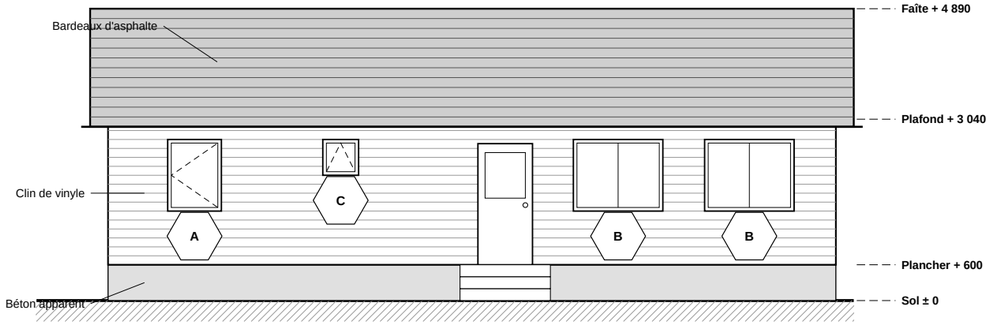


1 **ÉLÉVATION SUD (PRINCIPALE)**
Échelle 1:100

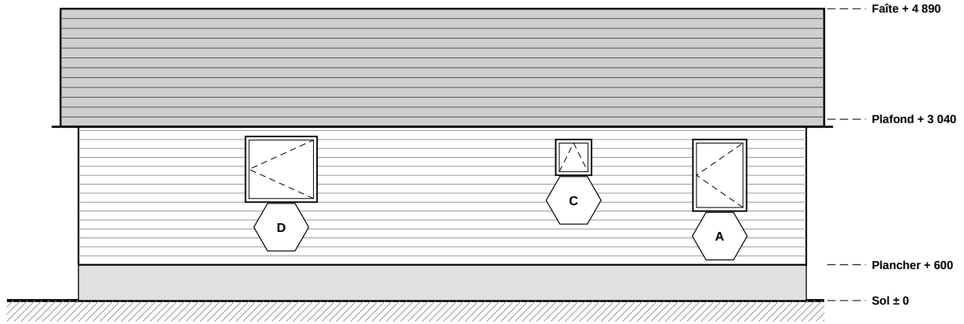

2 **ÉLÉVATION NORD**
Échelle 1:100

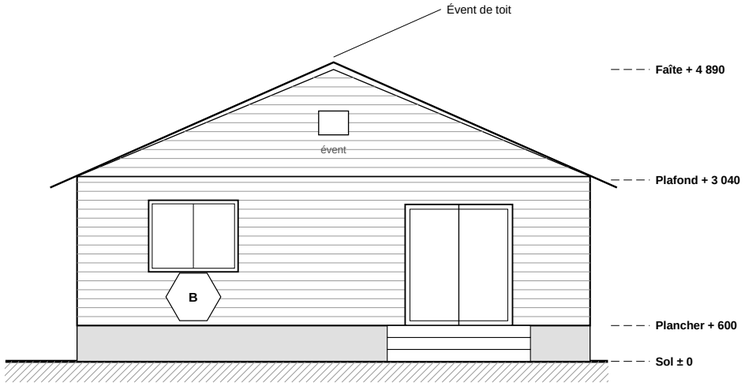

3 **ÉLÉVATION EST**
Échelle 1:100

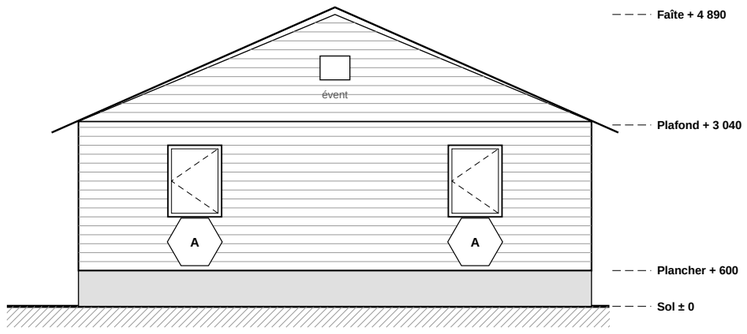

4 **ÉLÉVATION OUEST**
Échelle 1:100

Pavillon de L'AVENIR
Centre de formation professionnelle

PLAN D'EXERCICE
LECTURE DE PLANS

PROJET

MAISON UNIFAMILIALE
DOSSIER 1

125, rue des Érables
Ville fictive (Québec)

NOTES D'ÉLÉVATION

Revêtement : clin de vinyle horizontal, couleur gris pierre.

Toiture : bardeaux d'asphalte, pente 5 : 12.

Débord de toit : 450 mm, soffite ventilé en aluminium.

Fondation apparente : 600 mm au-dessus du sol fini.

Hexagones : types de fenêtres, voir A-301.

NIVEAUX

Sol : ± 0

Plancher : + 600

Plafond : + 3 040

Faîte : + 4 890

TITRE DE LA FEUILLE

ÉLÉVATIONS

CONÇU PAR

Jeremy, enseignant

DESSIN À DES FINS D'ENSEIGNEMENT — NE PAS UTILISER POUR LA CONSTRUCTION

ÉCHELLE

1:100


DATE

Octobre 2026

FEUILLE

A-201

Dossier D1

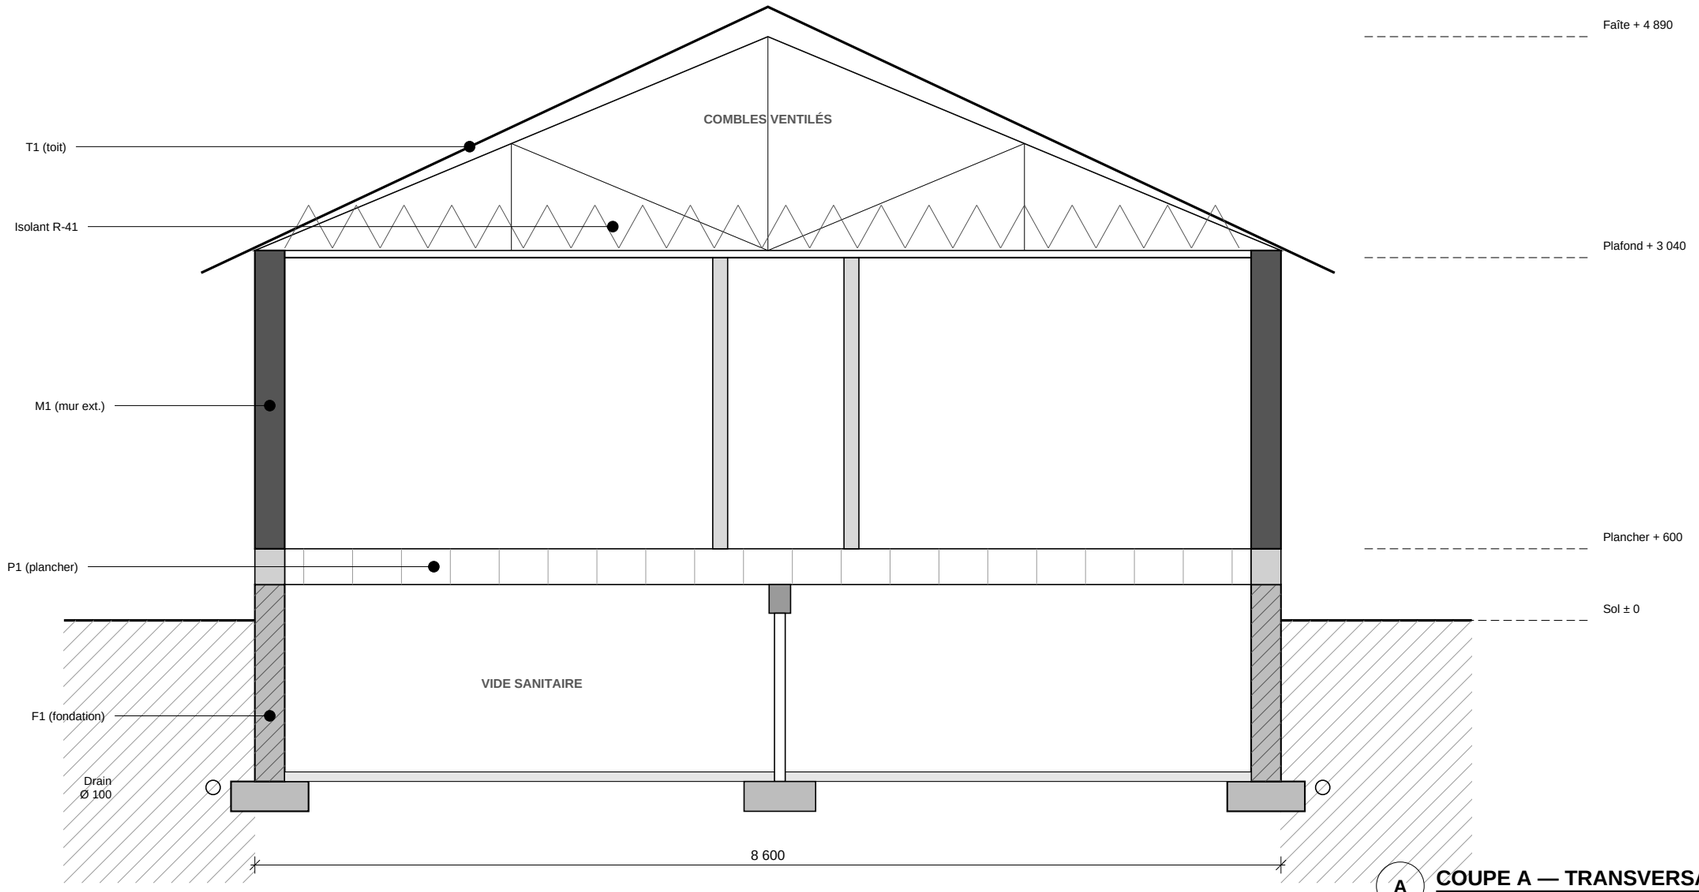

A **COUPE A — TRANSVERSALE**

Échelle 1:50

NOMENCLATURE DES PORTES

No	Dimensions (mm)	Type	Matériau	Quincaillerie
101	915 × 2 030	Battante	Acier isolé, vitrage 1/2	Serrure + pêne dormant
102	1 800 × 2 030	Coulissante	PVC, vitrage double	Loquet + barre de sécurité
103	760 × 2 030	Battante	Âme creuse, MDF peint	Passage
104	760 × 2 030	Battante	Âme creuse, MDF peint	Intimité (verrou)
105	760 × 2 030	Battante	Âme creuse, MDF peint	Passage
106	815 × 2 030	Battante	Âme creuse, MDF peint	Passage
—	900 × 2 030	Baie	Ouverture sans porte	—

NOMENCLATURE DES FENÊTRES

Type	Qté	Larg. × haut. (mm)	Allège	Ouverture	Vitrage
A	4	900 × 1 200	900	Battant, à manivelle	Double, faible émissivité, argon
B	3	1 500 × 1 200	900	Coulissante	Double, faible émissivité, argon
C	2	600 × 600	1 500	Auvent	Double, givré
D	1	1 200 × 1 100	1 050	Battant, à manivelle	Double, faible émissivité, argon

Pavillon de L'AVENIR
Centre de formation professionnelle

PLAN D'EXERCICE
LECTURE DE PLANS

PROJET

MAISON UNIFAMILIALE
DOSSIER 1

125, rue des Érables
Ville fictive (Québec)

COMPOSITIONS

T1 — Toit : bardeaux d'asphalte, membrane, contreplaqué 12,7, fermes 600 c/c, isolant soufflé R-41, pare-vapeur, gypse 12,7.

M1 — Mur extérieur : clin de vinyle, fourrures, panneau isolant 25, OSB 11, montants 38 × 140 à 400 c/c, laine R-24, pare-vapeur, gypse 12,7.

M2 — Mur intérieur : gypse 12,7 deux faces, montants 38 × 89 à 400 c/c (laine insonorisante autour de la salle de bain).

P1 — Plancher : revêtement, contreplaqué 15,9 collé-vissé, solives 38 × 235 à 400 c/c, isolant R-31 au rive.

F1 — Fondation : mur de béton 250, 25 MPa, semelle 650 × 250, drain français.

TITRE DE LA FEUILLE

COUPE TRANSVERSALE ET NOMENCLATURES

CONÇU PAR

Jeremy, enseignant

DESSIN À DES FINS D'ENSEIGNEMENT — NE PAS UTILISER POUR LA CONSTRUCTION

ÉCHELLE

1:50


DATE

Octobre 2026

FEUILLE

A-301

Dossier D1

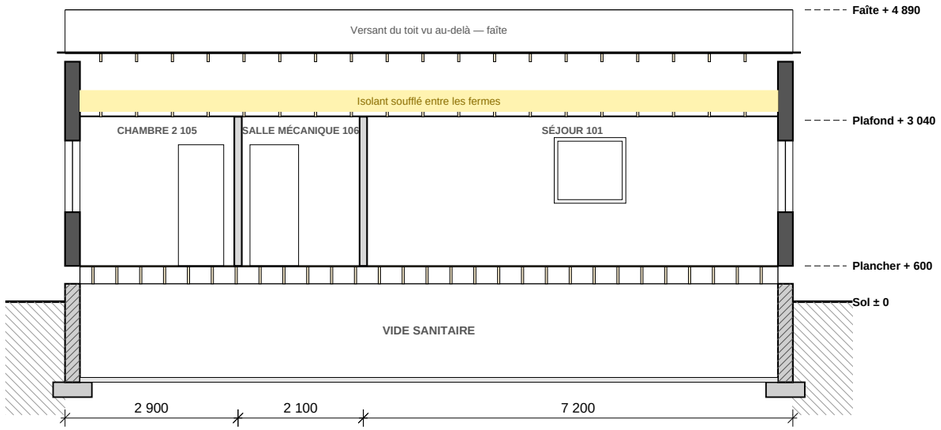


B **COUPE B — LONGITUDINALE**

Échelle 1:100

LÉGENDE DES MATÉRIAUX EN COUPE

- Béton coulé
- Sol naturel (terre)
- Pierre concassée, pierre nette
- Brique d'argile
- Bloc de béton
- Isolant rigide (panneau)
- Isolant en natte (laine)
- Bois de charpente coupé
- Contreplaqué ou OSB
- Plaque de plâtre (gypse)
- Acier
- Lame d'air, vide

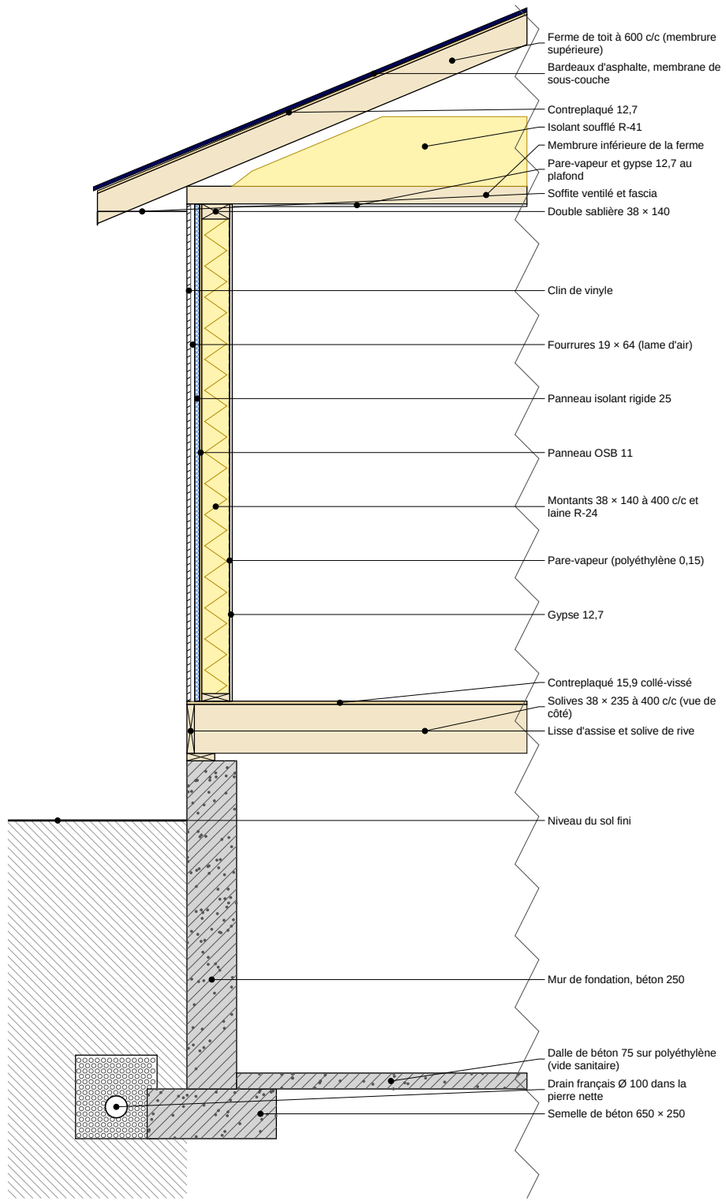

2 **COUPE DE MUR TYPE**

Échelle 1:30

Pavillon de L'AVENIR
Centre de formation professionnelle

PLAN D'EXERCICE
LECTURE DE PLANS

PROJET

MAISON UNIFAMILIALE
DOSSIER 1

125, rue des Érables
Ville fictive (Québec)

À OBSERVER

La coupe B est prise sur la ligne B du plan A-101, en regardant dans le sens des flèches.

Ce qui est coupé est dessiné en trait fort et hachuré ; ce qui est vu au-delà est en trait fin.

La coupe de mur montre l'ordre des couches, de l'extérieur vers l'intérieur.

Comparer les niveaux avec ceux des élévations (A-201) et de la coupe A (A-301).

COMPOSITIONS

T1 — Toit : bardeaux d'asphalte, membrane, contreplaqué 12,7, fermes 600 c/c, isolant soufflé R-41, pare-vapeur, gypse 12,7.

M1 — Mur extérieur : clin de vinyle, fourrures, panneau isolant 25, OSB 11, montants 38 × 140 à 400 c/c, laine R-24, pare-vapeur, gypse 12,7.

M2 — Mur intérieur : gypse 12,7 deux faces, montants 38 × 89 à 400 c/c (laine insonorisante autour de la salle de bain).

P1 — Plancher : revêtement, contreplaqué 15,9 collé-vissé, solives 38 × 235 à 400 c/c, isolant R-31 au rive.

F1 — Fondation : mur de béton 250, 25 MPa, semelle 650 × 250, drain français.

TITRE DE LA FEUILLE

COUPE LONGITUDINALE, COUPE DE MUR ET MATÉRIAUX

CONÇU PAR

Jeremy, enseignant

DESSIN À DES FINS D'ENSEIGNEMENT — NE PAS UTILISER POUR LA CONSTRUCTION

ÉCHELLE

1:100 et 1:30


FEUILLE

A-302

DATE

Octobre 2026

Dossier D1

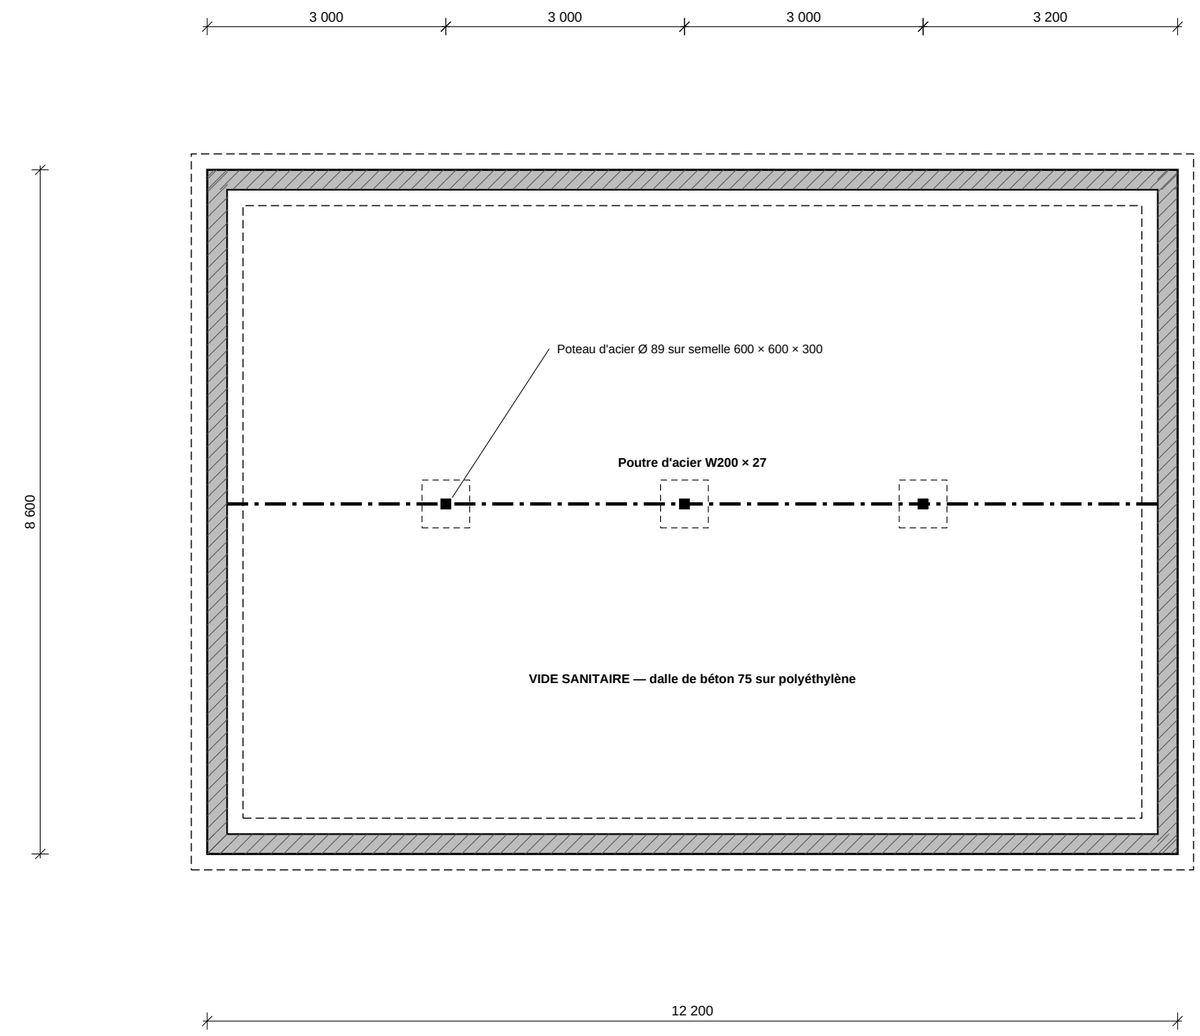

1 **PLAN DES FONDATIONS**
Échelle 1:75

2 **DÉTAIL TYPE — SEMELLE ET MUR**
Échelle 1:20

Pavillon de L'AVENIR
Centre de formation professionnelle

PLAN D'EXERCICE
LECTURE DE PLANS

PROJET

MAISON UNIFAMILIALE
DOSSIER 1

125, rue des Érables
Ville fictive (Québec)

NOTES DE STRUCTURE

Béton : 25 MPa à 28 jours, air entraîné 5 à 8 %.

Semelles sur sol non remanié, 1 600 mm minimum sous le niveau du sol fini (gel).

Capacité portante du sol présumée : 75 kPa. Faire valider par un ingénieur.

Armature : 2 barres 10M continues dans les semelles.

Solives de plancher 38 × 235 à 400 c/c, appuyées sur la poutre centrale.

LÉGENDE

Poché hachuré : mur de fondation en béton coulé

Tirets : semelle (sous le niveau du plancher)

Carré plein : poteau · carré en tirets : semelle isolée

— · — Poutre porteuse


TITRE DE LA FEUILLE

PLAN DES FONDATIONS ET DÉTAIL TYPE

CONÇU PAR
Jeremy, enseignant

DESSIN À DES FINS D'ENSEIGNEMENT — NE PAS UTILISER POUR LA CONSTRUCTION

ÉCHELLE	FEUILLE
1:75 et 1:20	**S-101**
DATE	Dossier D1
Octobre 2026	

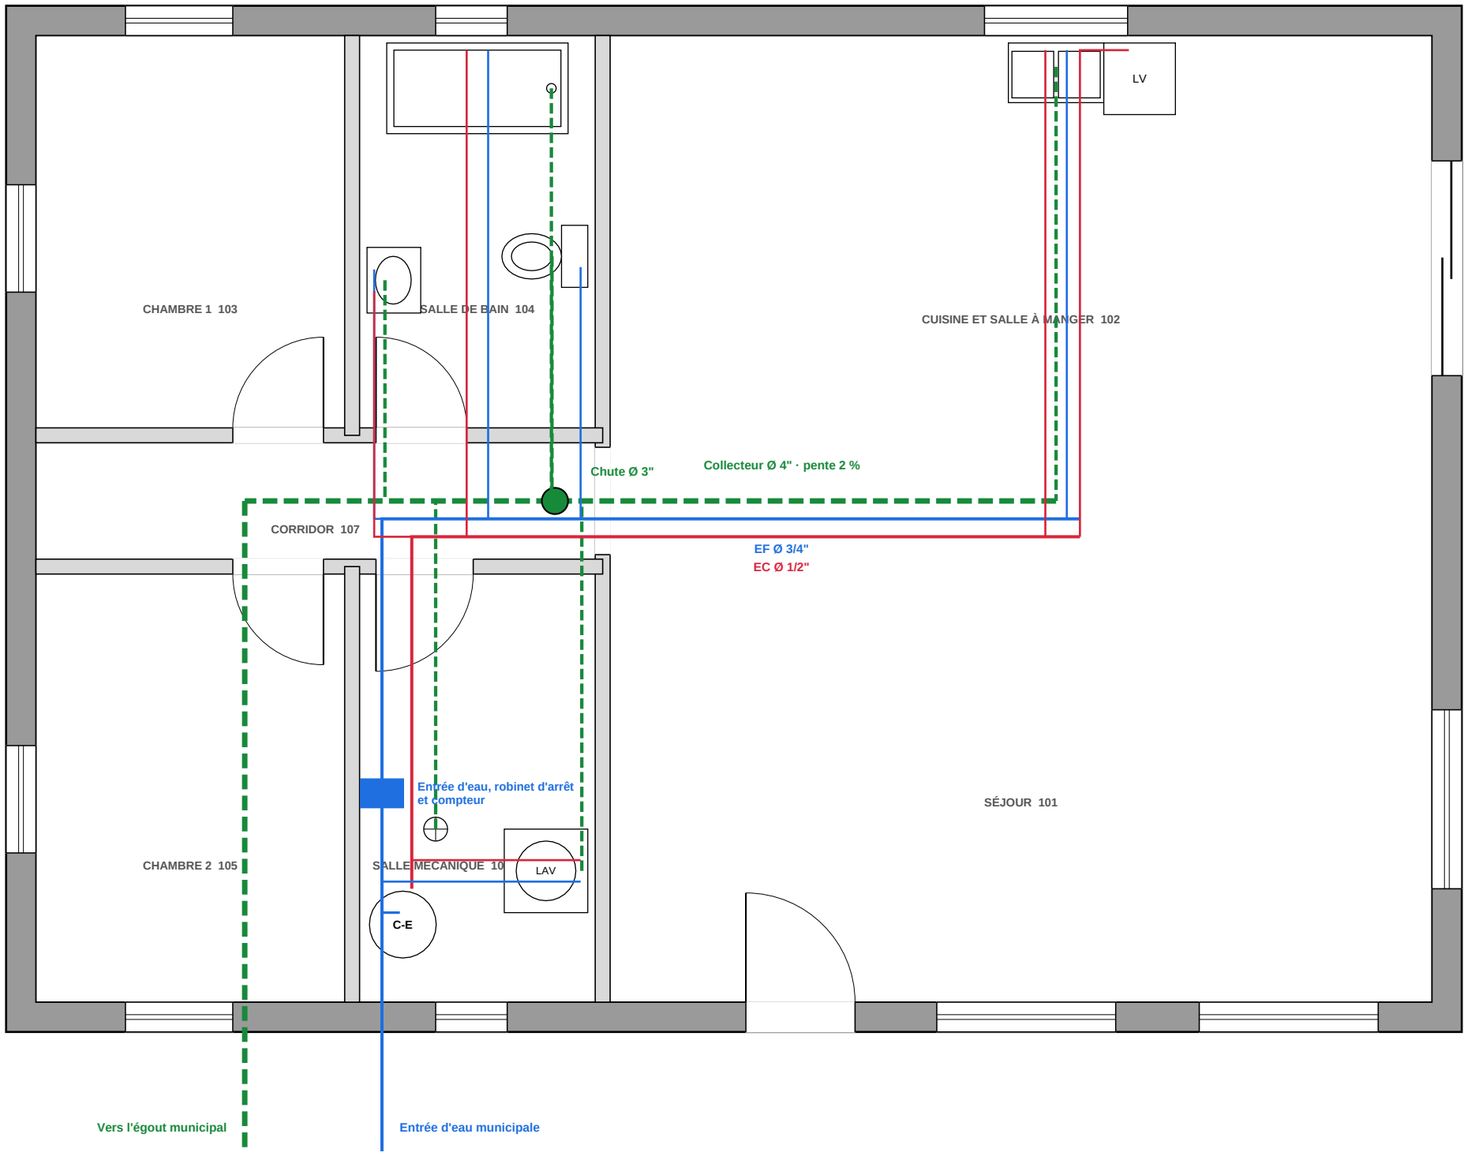

1 **PLAN DE PLOMBERIE**
Échelle 1:50

Pavillon de L'AVENIR
Centre de formation professionnelle

PLAN D'EXERCICE
LECTURE DE PLANS

PROJET

MAISON UNIFAMILIALE
DOSSIER 1

125, rue des Érables
Ville fictive (Québec)

NOTES DE PLOMBERIE

Tuyauterie d'eau : PEX ou cuivre type L.

Drainage et ventilation : ABS cédule 40.

Robinet d'arrêt sur chaque alimentation d'appareil.

Chauffe-eau : soupape T et P raccordée à 150 mm du sol.

Clapet antiretour sur le collecteur principal (voir isométrique).

LÉGENDE

- Eau froide (EF)
- Eau chaude (EC)
- Drainage sanitaire
- Ventilation (évent)
- Colonne de chute

TITRE DE LA FEUILLE

PLAN DE PLOMBERIE
REZ-DE-CHAUSSÉE


CONÇU PAR
Jeremy, enseignant

DESSIN À DES FINS D'ENSEIGNEMENT — NE PAS UTILISER POUR LA CONSTRUCTION

ÉCHELLE
1:50

DATE
Octobre 2026

FEUILLE
P-101
Dossier D1

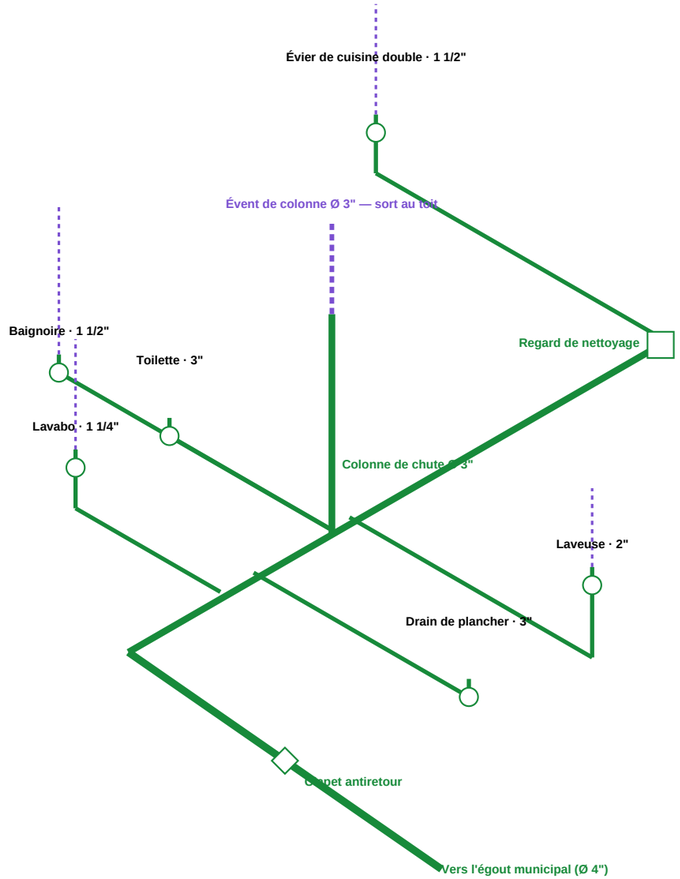

1 SCHÉMA ISOMÉTRIQUE — DRAINAGE ET VENTILATION

Échelle sans échelle

NOMENCLATURE DES APPAREILS SANITAIRES

Code	Appareil	Qté	EF	EC	Drain	Évent	Unités
BAIN	Baignoire	1	1/2"	1/2"	1 1/2"	1 1/4"	1,5
WC	Toilette (réservoir 6 L)	1	1/2"	—	3"	2"	4
LAV	Lavabo	1	1/2"	1/2"	1 1/4"	1 1/4"	1
EVD	Évier de cuisine double	1	1/2"	1/2"	1 1/2"	1 1/4"	1,5
LV	Lave-vaisselle	1	—	1/2"	(évier)	—	1
CE	Chauffe-eau électrique 270 L	1	3/4"	3/4"	—	—	0
LAVE	Laveuse (tuyau de rejet)	1	1/2"	1/2"	2"	1 1/2"	1,5
DP	Drain de plancher	1	—	—	3"	—	2
	TOTAL DES UNITÉS (charge hydraulique)						12,5

Pavillon de L'AVENIR
Centre de formation professionnelle

PLAN D'EXERCICE
LECTURE DE PLANS

PROJET

MAISON UNIFAMILIALE
DOSSIER 1

125, rue des Érables
Ville fictive (Québec)

À OBSERVER

Chaque appareil est protégé par un siphon, puis ventilé.

Les branchements ont une pente d'au moins 1 : 50 (2 %).

Le diamètre du drain augmente à mesure qu'on approche de l'égout.

La colonne se prolonge en évent jusqu'au-dessus du toit.

Les unités de charge sont indicatives : vérifier les valeurs du Code de plomberie en vigueur.

TITRE DE LA FEUILLE

SCHÉMA ISOMÉTRIQUE ET NOMENCLATURE DES APPAREILS

CONÇU PAR

Jeremy, enseignant

DESSIN À DES FINS D'ENSEIGNEMENT — NE PAS UTILISER POUR LA CONSTRUCTION

ÉCHELLE

Sans échelle


DATE

Octobre 2026

FEUILLE

P-102

Dossier D1

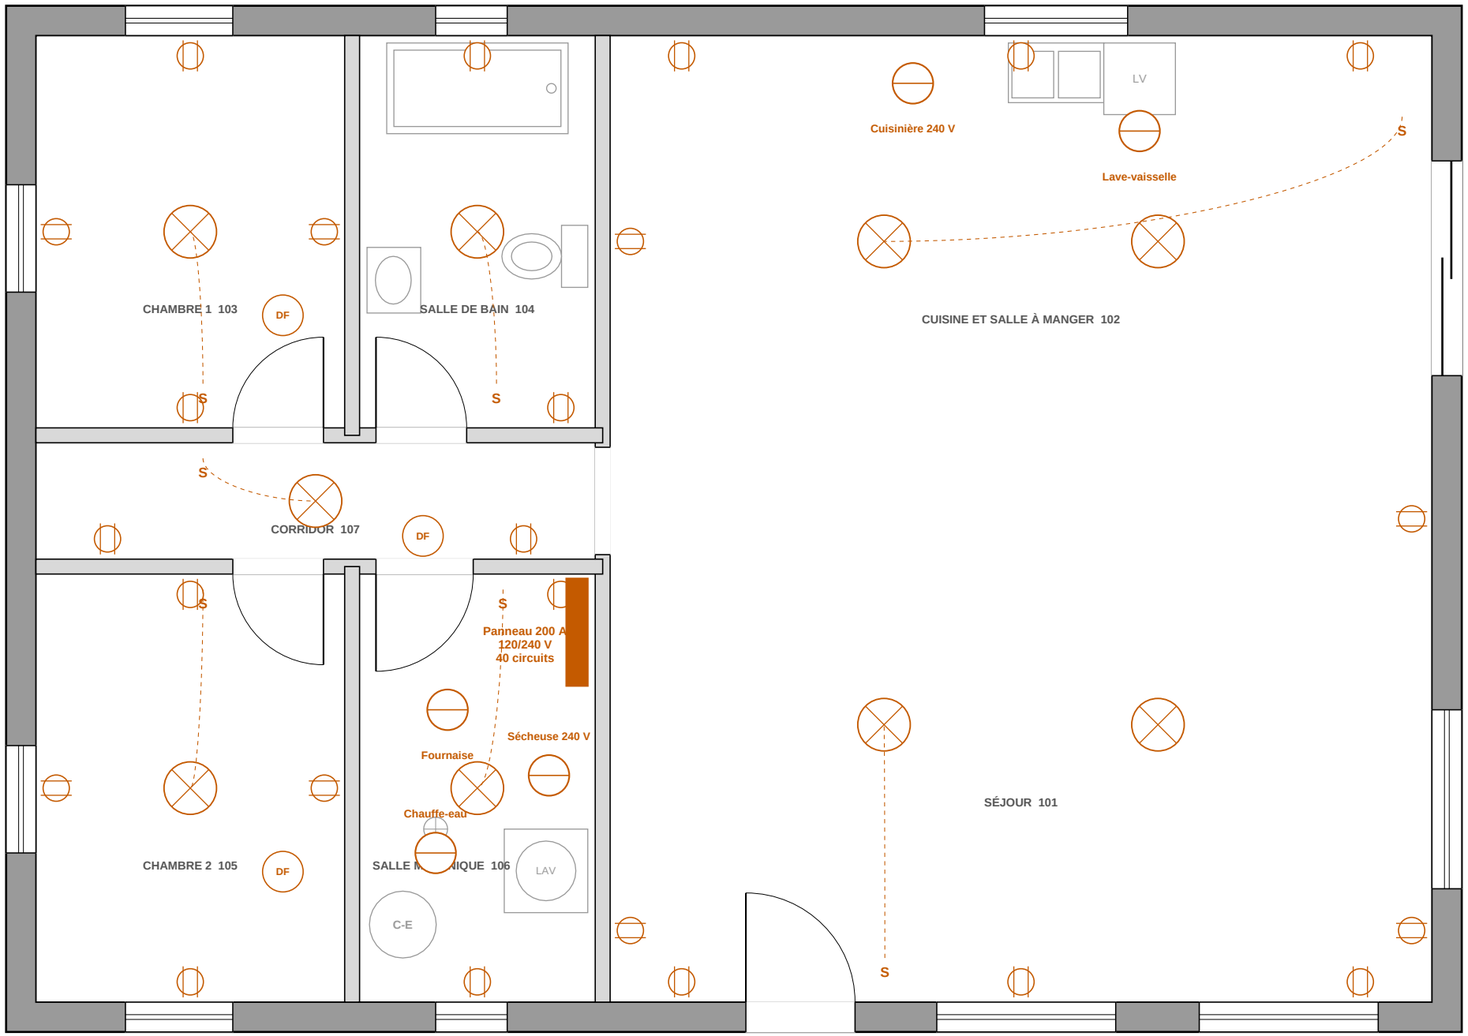

1 **PLAN D'ÉLECTRICITÉ**
Échelle 1:50

Pavillon de L'AVENIR
Centre de formation professionnelle

PLAN D'EXERCICE
LECTURE DE PLANS

PROJET

MAISON UNIFAMILIALE
DOSSIER 1

125, rue des Érables
Ville fictive (Québec)

NOTES D'ÉLECTRICITÉ

Installation selon le Code de construction du Québec, chapitre V — Électricité.

Prises de la cuisine : circuits de 20 A avec prises T.

Prises de la salle de bain et extérieures : protection DDFT.

Avertisseurs de fumée reliés entre eux et raccordés en permanence.

Aucun point le long d'un mur à plus de 1,8 m d'une prise.

LÉGENDE

- Prise de courant double 15 A
- Luminaire au plafond
- S — Interrupteur unipolaire
- DF — Avertisseur de fumée relié
- Prise 240 V ou appareil dédié
- Panneau de distribution

CIRCUITS (EXTRAIT)

No	Usage	Charge	Disj.
1	Prises et éclairage — Séjour	15 A	1 × 15 A
2	Prises et éclairage — Cuisine et s	15 A	1 × 15 A
3	Prises et éclairage — Chambre 1	15 A	1 × 15 A
4	Prises et éclairage — Salle de bai	15 A	1 × 15 A
5	Prises et éclairage — Chambre 2	15 A	1 × 15 A
6	Prises et éclairage — Salle mécani	15 A	1 × 15 A
7	Prises et éclairage — Corridor	15 A	1 × 15 A
8	Cuisinière 240 V	40 A 240 V	2 × 40 A
9	Sécheuse 240 V	30 A 240 V	2 × 30 A
10	Chauffe-eau	30 A 240 V	2 × 30 A
11	Lave-vaisselle	15 A 120 V	1 × 15 A
12	Fournaise	100 A 240 V	2 × 100 A

TITRE DE LA FEUILLE

PLAN D'ÉLECTRICITÉ


CONÇU PAR
Jeremy, enseignant

DESSIN À DES FINS D'ENSEIGNEMENT — NE PAS UTILISER POUR LA CONSTRUCTION

ÉCHELLE
1:50

DATE
Octobre 2026

FEUILLE
E-101
Dossier D1

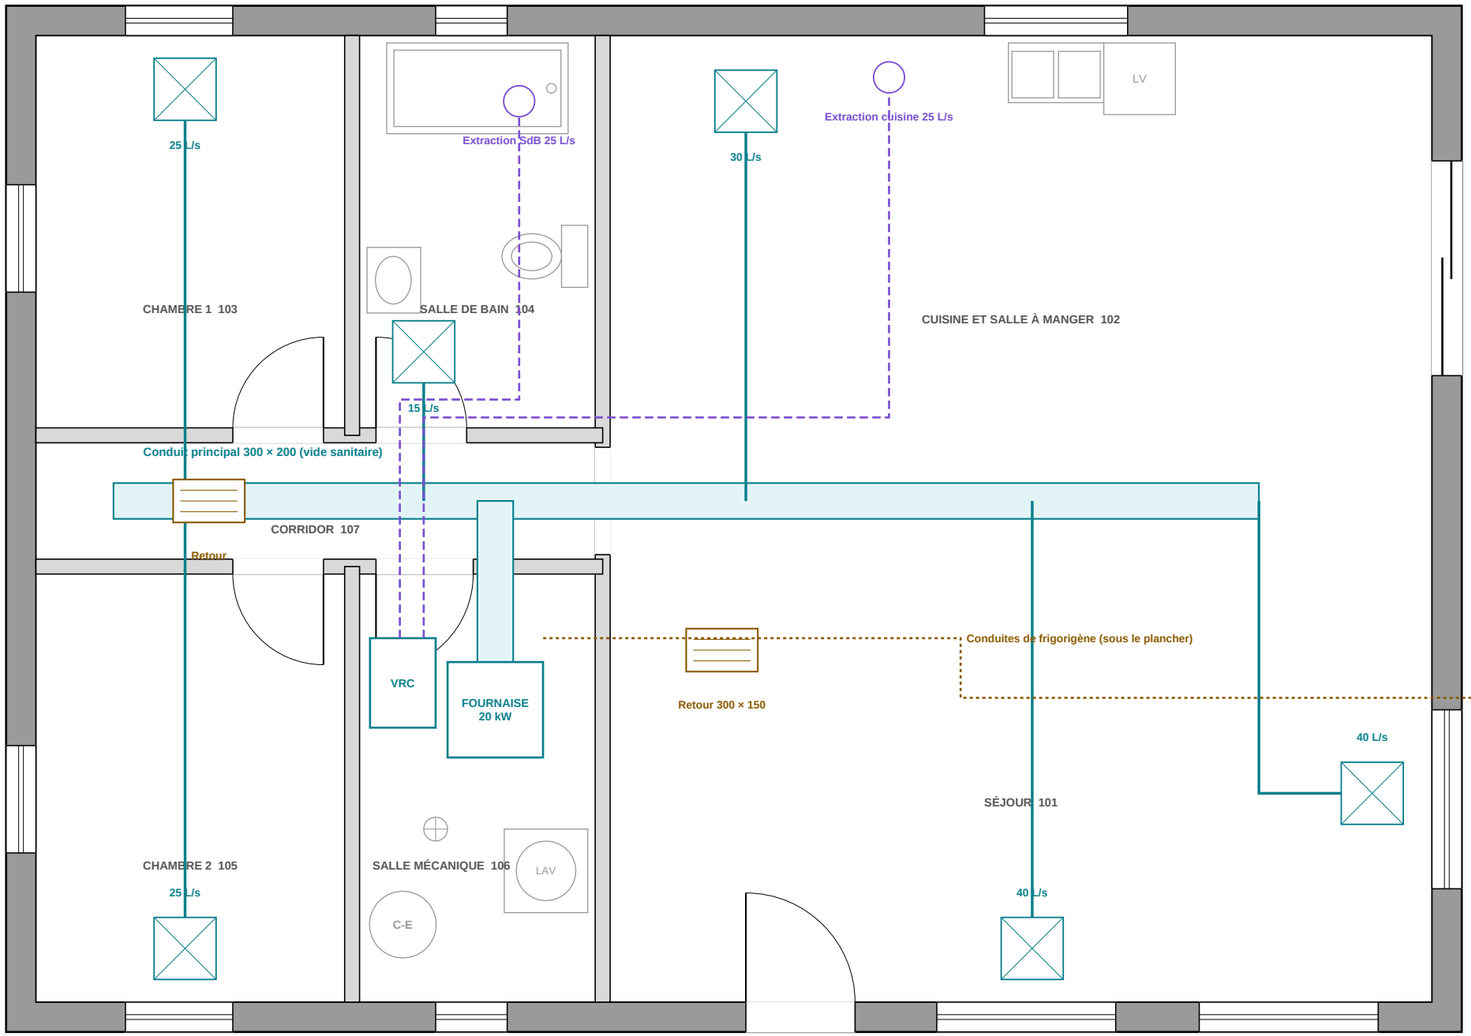

1 **PLAN DE CHAUFFAGE ET VENTILATION**
Échelle 1:50

Pavillon de L'AVENIR
Centre de formation professionnelle

PLAN D'EXERCICE
LECTURE DE PLANS

PROJET

MAISON UNIFAMILIALE
DOSSIER 1

125, rue des Érables
Ville fictive (Québec)

NOTES CVCA

Fournaise électrique 20 kW et thermopompe centrale de 2 tonnes.

Conduits en acier galvanisé isolé dans le vide sanitaire.

VRC : évacuation de la salle de bain et de la cuisine, alimentation par le retour de la fournaise.

Débits en litres par seconde (L/s).

LÉGENDE

Conduit d'alimentation

Carré avec X : diffuseur d'alimentation (L/s)

Rectangle ligné : grille de retour

Conduit d'évacuation (VRC)

TITRE DE LA FEUILLE

PLAN DE CHAUFFAGE, VENTILATION ET CLIMATISATION

CONÇU PAR
Jeremy, enseignant

DESSIN À DES FINS D'ENSEIGNEMENT — NE PAS UTILISER POUR LA CONSTRUCTION

ÉCHELLE
1:50

DATE
Octobre 2026

FEUILLE
M-101
Dossier D1