MAISON UNIFAMILIALE

DOSSIER 1
125, rue des Érables
Ville fictive (Québec)

Conçu par Jeremy, enseignant

Grande maison unifamiliale de haut standing, deux étages et sous-sol aménagé (environ 14,5 × 10,4 m) : deux toits monopentes décalés à grands débords (900 mm) séparés par une bande vitrée, pierre naturelle à l'entrée, zinc prépatiné et cèdre brûlé, grandes fenêtres au sud.
Rez-de-chaussée à aire ouverte, quatre chambres, trois salles de bain ou salles d'eau.
Chauffage par air pulsé (fournaise électrique et thermopompe), ventilation par VRC.

LISTE DES FEUILLES

Feuille	Titre
000	Page de garde et liste des feuilles
A-100	Plan d'implantation et de site
A-101	Plan du sous-sol
A-102	Plan du rez-de-chaussée
A-103	Plan de l'étage
A-201	Élévations
A-301	Coupe transversale et nomenclatures
A-302	Coupe longitudinale, coupe de mur et matériaux
S-101	Plan des fondations et détail type
P-101	Plomberie sous-sol
P-102	Plomberie rez-de-chaussée
P-103	Plomberie étage
P-104	Schéma isométrique et nomenclature des appareils
E-101	Électricité sous-sol
E-102	Électricité rez-de-chaussée
E-103	Électricité étage
M-101	Chauffage et ventilation sous-sol
M-102	Chauffage et ventilation rez-de-chaussée
M-103	Chauffage et ventilation étage

DONNÉES DU BÂTIMENT

Élément	Valeur
Usage	Habitation unifamiliale
Étages	2 + sous-sol aménagé
Emprise au sol	150,8 m²
Superficie habitable	409 m² (3 niveaux)
Structure	Ossature de bois, solives en I, fondation de béton
Toiture	Deux monopentes décalés, membrane élastomère, débords 900
Chauffage	Air pulsé + thermopompe, VRC
Eau et égout	Réseaux municipaux
Lot	26 000 × 38 000

Pavillon de L'AVENIR
Centre de formation professionnelle

PLAN D'EXERCICE
LECTURE DE PLANS

PROJET

MAISON UNIFAMILIALE
DOSSIER 1

125, rue des Érables
Ville fictive (Québec)

UTILISATION EN CLASSE

Ce dossier sert à apprendre à lire des plans : repérer les feuilles, les échelles, les symboles, les cotes et les liens entre les disciplines.

Une maison à trois niveaux : chaque niveau a son plan (A), sa plomberie (P), son électricité (E) et son chauffage (M).

Les renvois (bulles de coupe, types de fenêtres, numéros de portes) relient les feuilles entre elles.

Bâtiment fictif. Les valeurs sont plausibles mais non vérifiées pour la construction.

TITRE DE LA FEUILLE

PAGE DE GARDE
ET LISTE DES FEUILLES

CONÇU PAR

Jeremy, enseignant

DESSIN À DES FINS D'ENSEIGNEMENT — NE PAS UTILISER POUR LA CONSTRUCTION

ÉCHELLE

—

DATE

Octobre 2026


FEUILLE

000

Dossier D1

N

LOT 4 123 456 · SUPERFICIE 988,0 m²

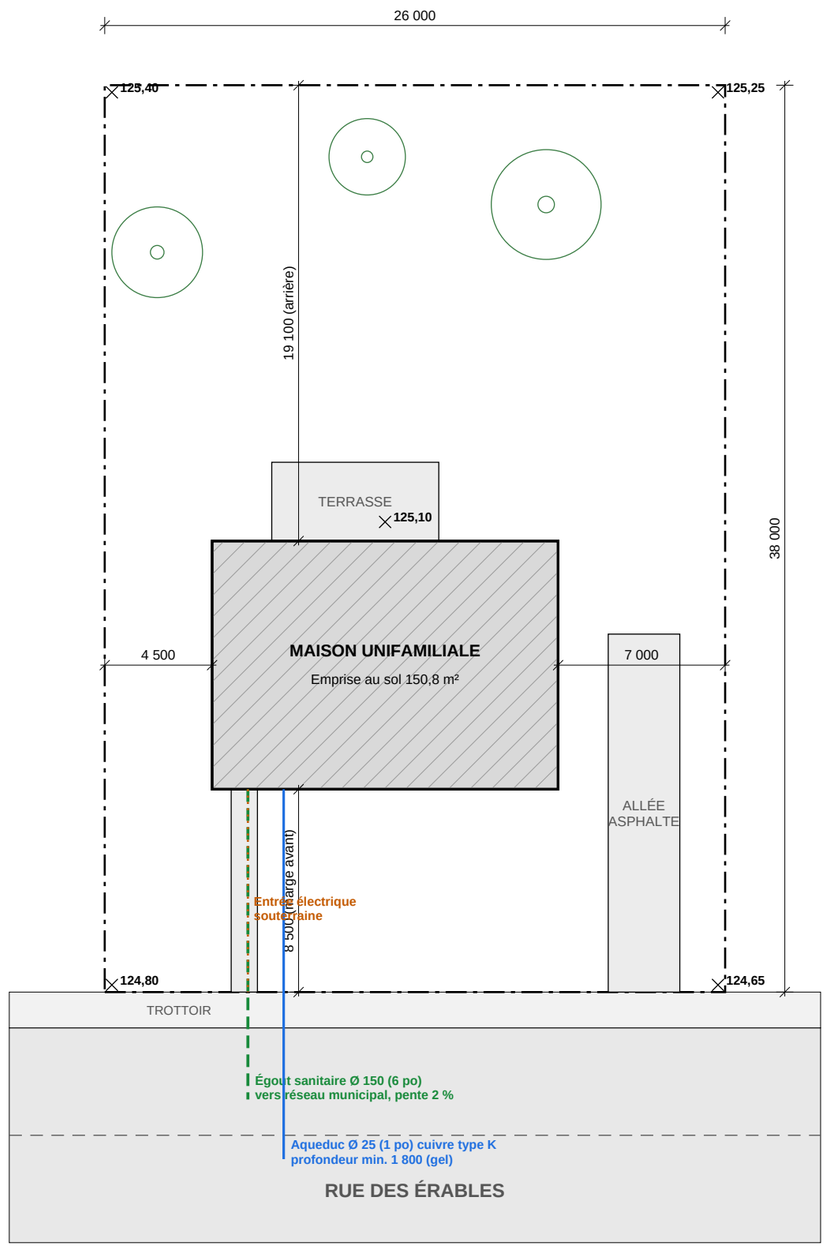

0 2 4 6 8 10 m

1 PLAN D'IMPLANTATION
Échelle 1:250

Pavillon de L'AVENIR
Centre de formation professionnelle

PLAN D'EXERCICE
LECTURE DE PLANS

PROJET

MAISON UNIFAMILIALE
DOSSIER 1

125, rue des Érables
Ville fictive (Québec)

NOTES D'IMPLANTATION

Implantation à confirmer par un arpenteur-géomètre.

Marge avant minimale : 7,5 m. Marges latérales : 2,0 m.

Niveaux du terrain en mètres (altitude géodésique).

Pente du terrain fini : 2 % minimum en s'éloignant du bâtiment.

LÉGENDE

— · — Limite de lot

Hachures : emprise du bâtiment

Croix : niveau du terrain (m, géodésique)

Bleu : aqueduc · Vert pointillé : égout sanitaire

Orange pointillé : entrée électrique

TITRE DE LA FEUILLE


PLAN D'IMPLANTATION ET DE SITE

CONÇU PAR
Jeremy, enseignant
DESSIN À DES FINS D'ENSEIGNEMENT — NE PAS UTILISER POUR LA CONSTRUCTION

ÉCHELLE
1:250

DATE
Octobre 2026

FEUILLE
A-100
Dossier D1

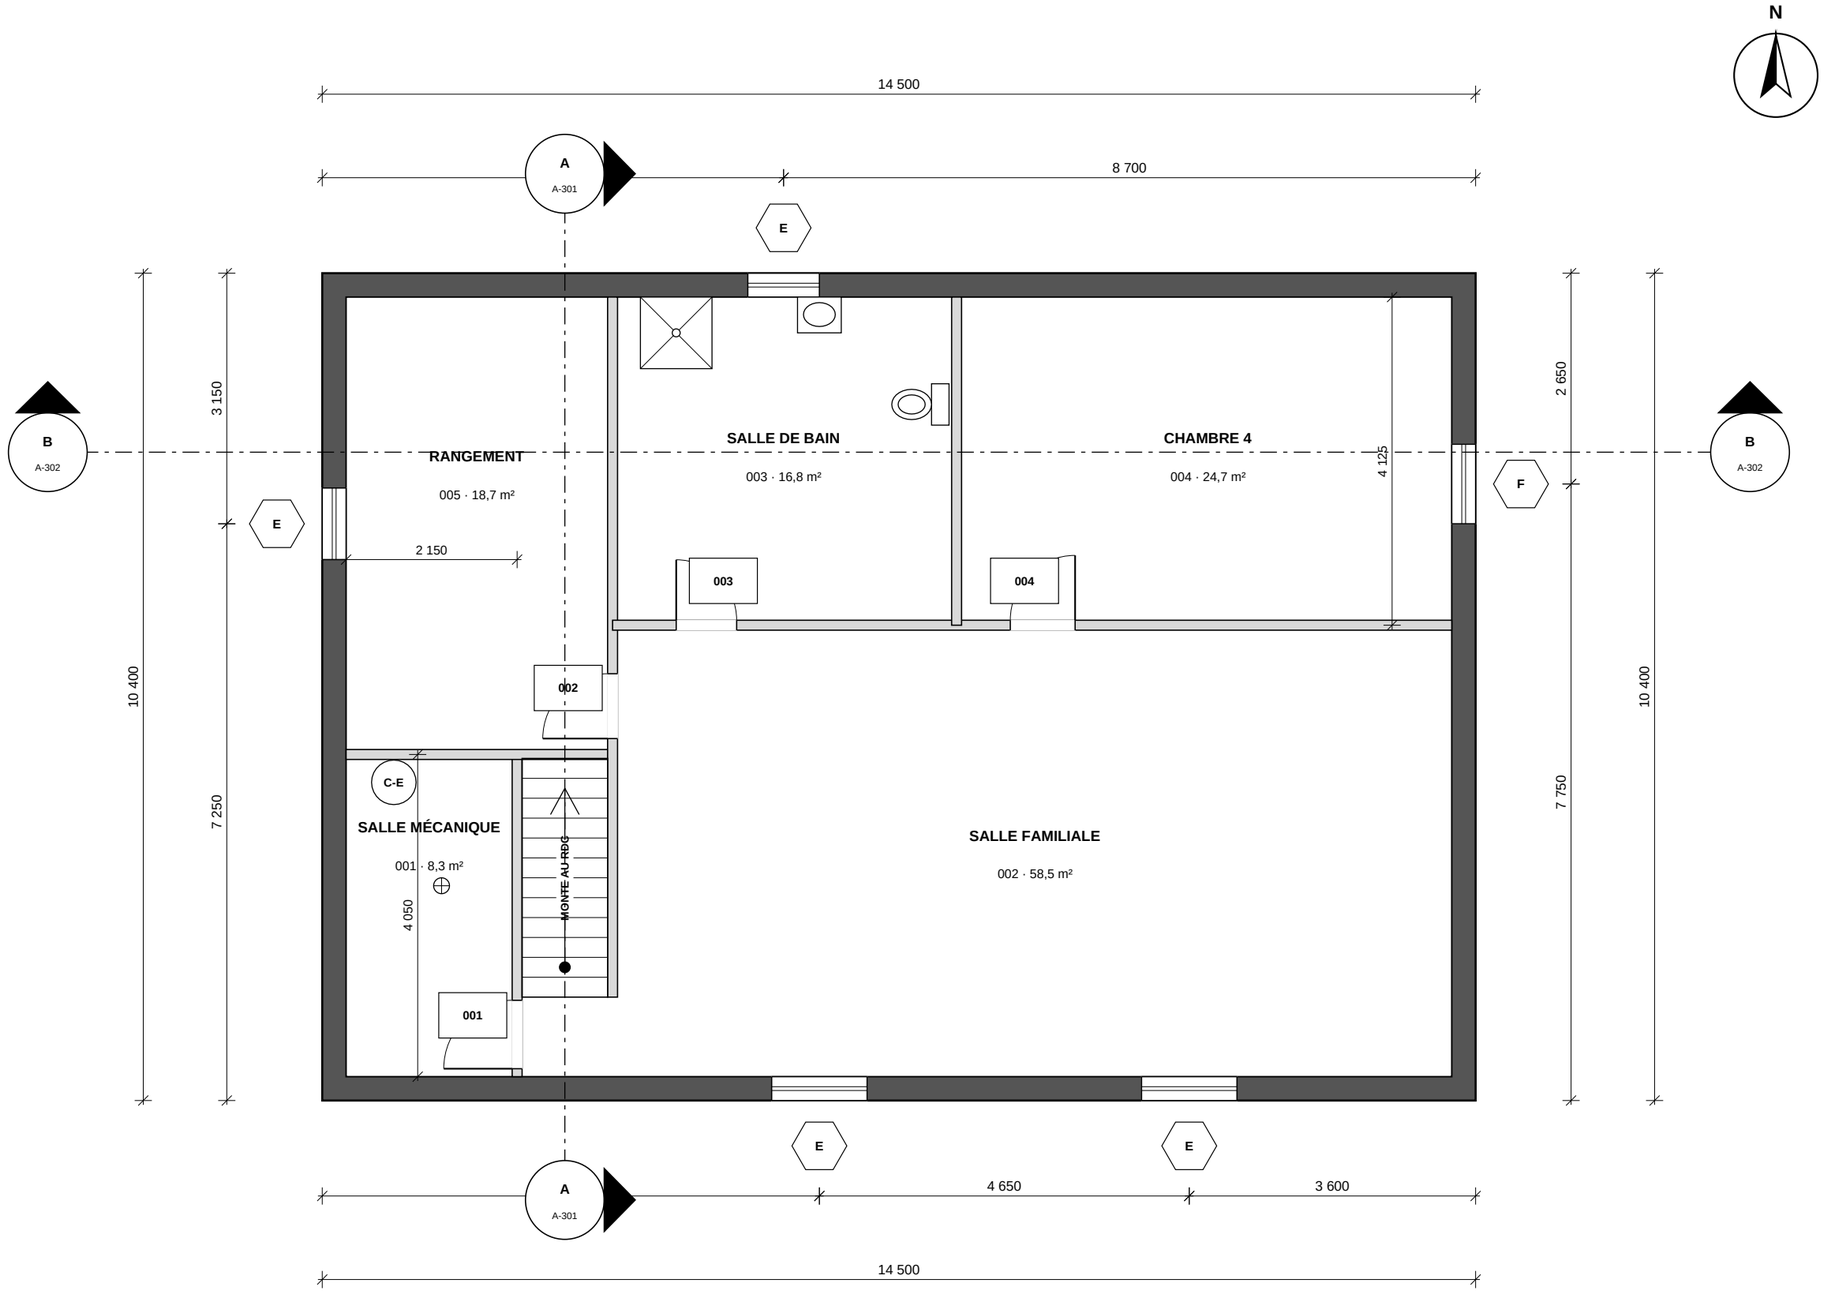

1 PLAN DU SOUS-SOL
Échelle 1:75

0 2 4 6 8 10 m

Pavillon de L'AVENIR
Centre de formation professionnelle

PLAN D'EXERCICE
LECTURE DE PLANS

PROJET

MAISON UNIFAMILIALE
DOSSIER 1

125, rue des Érables
Ville fictive (Québec)

NOTES GÉNÉRALES

Toutes les cotes sont en millimètres.

Hauteur libre sous les solives : 2 380 mm.

Mur de fondation : béton 250 isolé à l'extérieur (voir A-302).

Fenêtre F : issue de secours de la chambre, margelle de 1 000 de profondeur.

Poutre d'acier et poteaux : voir S-101.

LÉGENDE

Mur extérieur (poché foncé) : voir composition M1, feuille A-301

Mur intérieur (poché pâle) : voir composition M2

Hexagone : type de fenêtre (voir nomenclature, A-301)

Rectangle : numéro de porte (voir nomenclature, A-301)

Cotes en millimètres, aux faces extérieures du revêtement intermédiaire et aux axes des ouvertures

TITRE DE LA FEUILLE

PLAN DU SOUS-SOL

CONÇU PAR


Jeremy, enseignant

DESSIN À DES FINS D'ENSEIGNEMENT — NE PAS UTILISER POUR LA CONSTRUCTION

ÉCHELLE
1:75

DATE
Octobre 2026

FEUILLE
A-101
Dossier D1

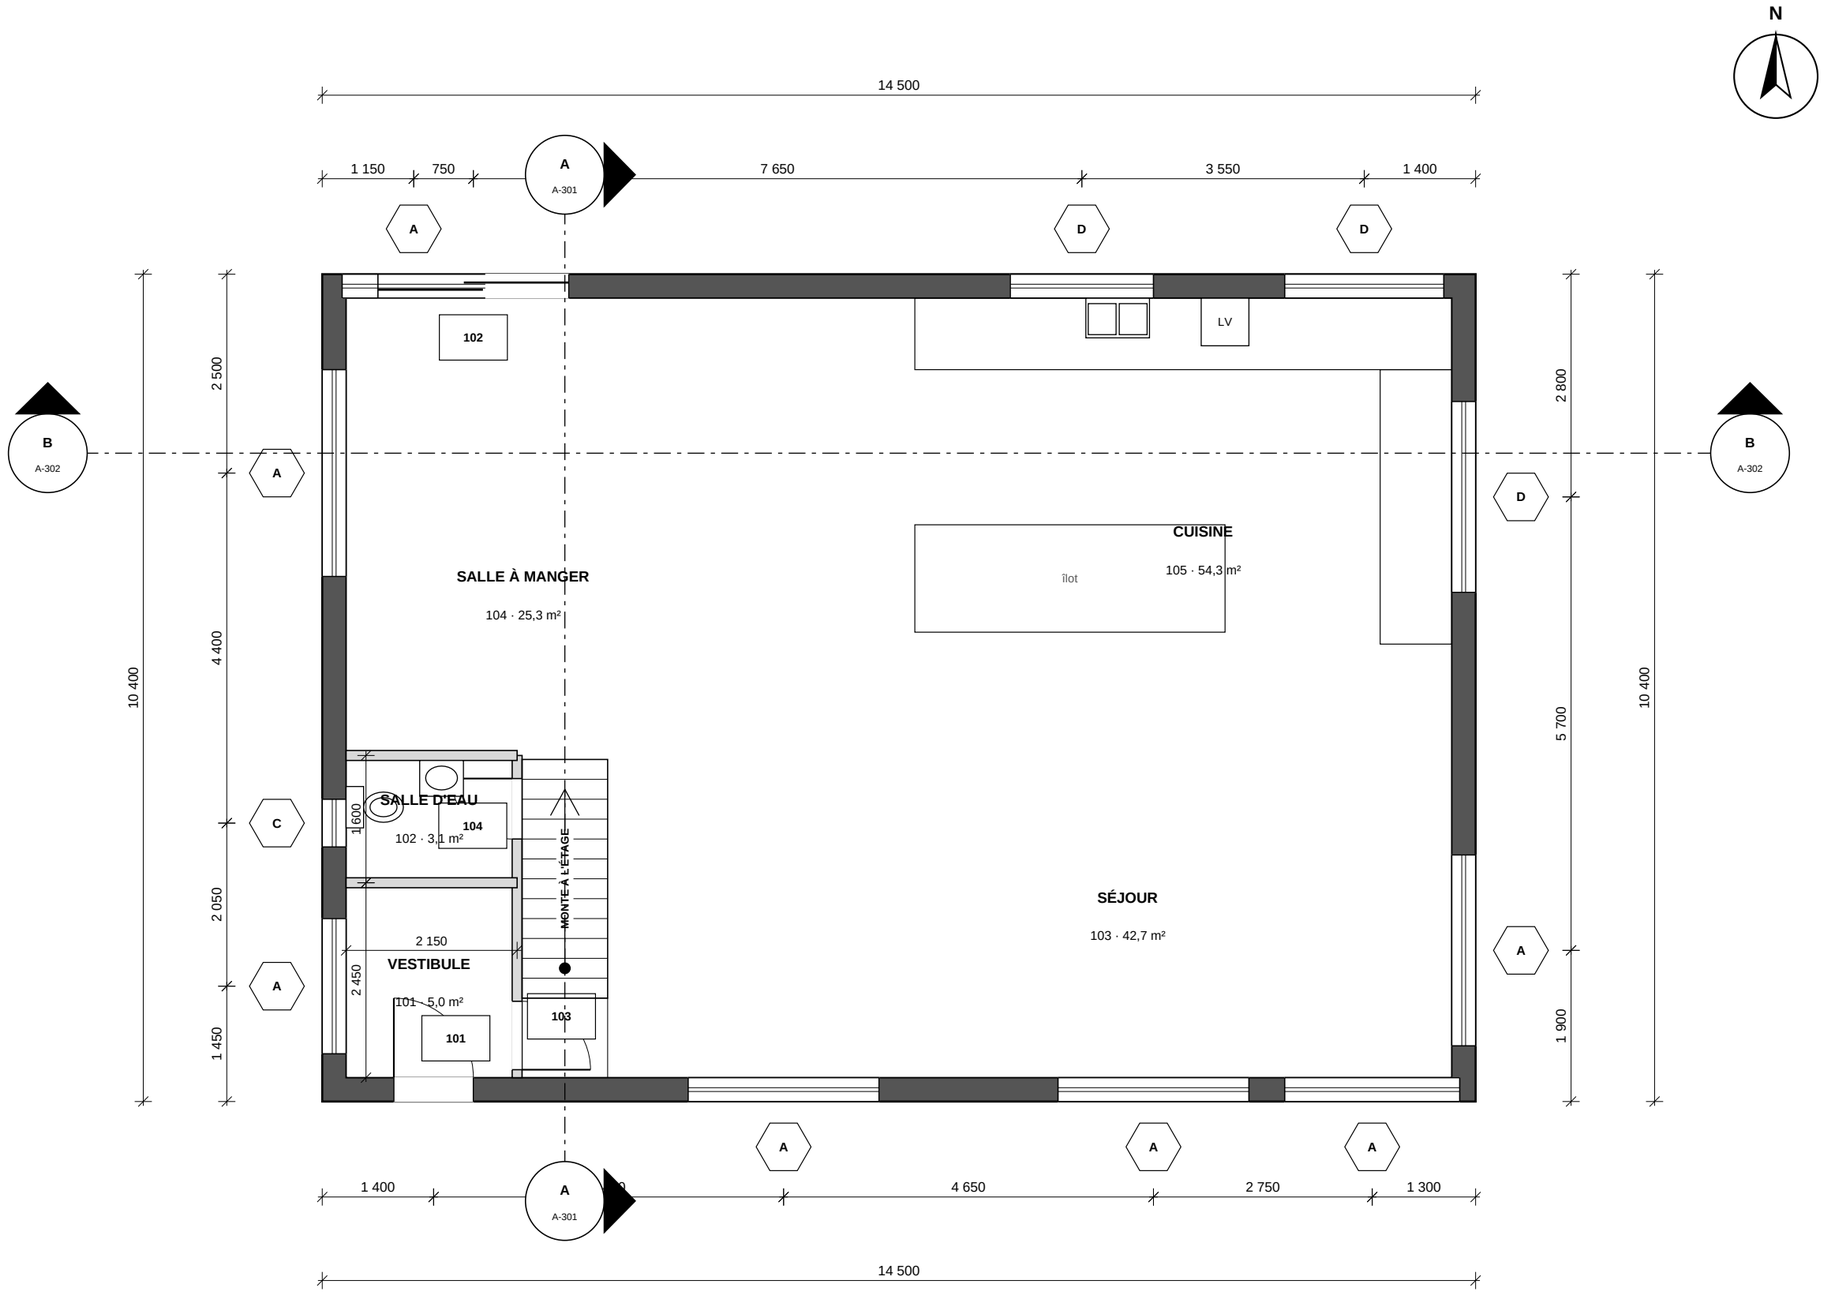

1 **PLAN DU REZ-DE-CHAUSSÉE**
Échelle 1:75

Pavillon de L'AVENIR
Centre de formation professionnelle

PLAN D'EXERCICE
LECTURE DE PLANS

PROJET

MAISON UNIFAMILIALE
DOSSIER 1

125, rue des Érables
Ville fictive (Québec)

NOTES GÉNÉRALES

Toutes les cotes sont en millimètres.

Cotes extérieures prises à la face extérieure du panneau OSB.

Hauteur libre sous plafond : 2 740 mm.

Escalier : volée de 12 contremarches, palier au sud. L'escalier du sous-sol est juste en dessous (même sens).

Garde-corps de verre de 900 le long de la cage, côté séjour.

Comptoirs : profondeur 600, hauteur 915; îlot de 900.

LÉGENDE

Mur extérieur (poché foncé) : voir composition M1, feuille A-301

Mur intérieur (poché pâle) : voir composition M2

Hexagone : type de fenêtre (voir nomenclature, A-301)

Rectangle : numéro de porte (voir nomenclature, A-301)

Cotes en millimètres, aux faces extérieures du revêtement intermédiaire et aux axes des ouvertures

TITRE DE LA FEUILLE

PLAN DU REZ-DE-CHAUSSÉE

CONÇU PAR

Jeremy, enseignant

DESSIN À DES FINS D'ENSEIGNEMENT — NE PAS UTILISER POUR LA CONSTRUCTION

ÉCHELLE

1:75


DATE

Octobre 2026

FEUILLE

A-102

Dossier D1

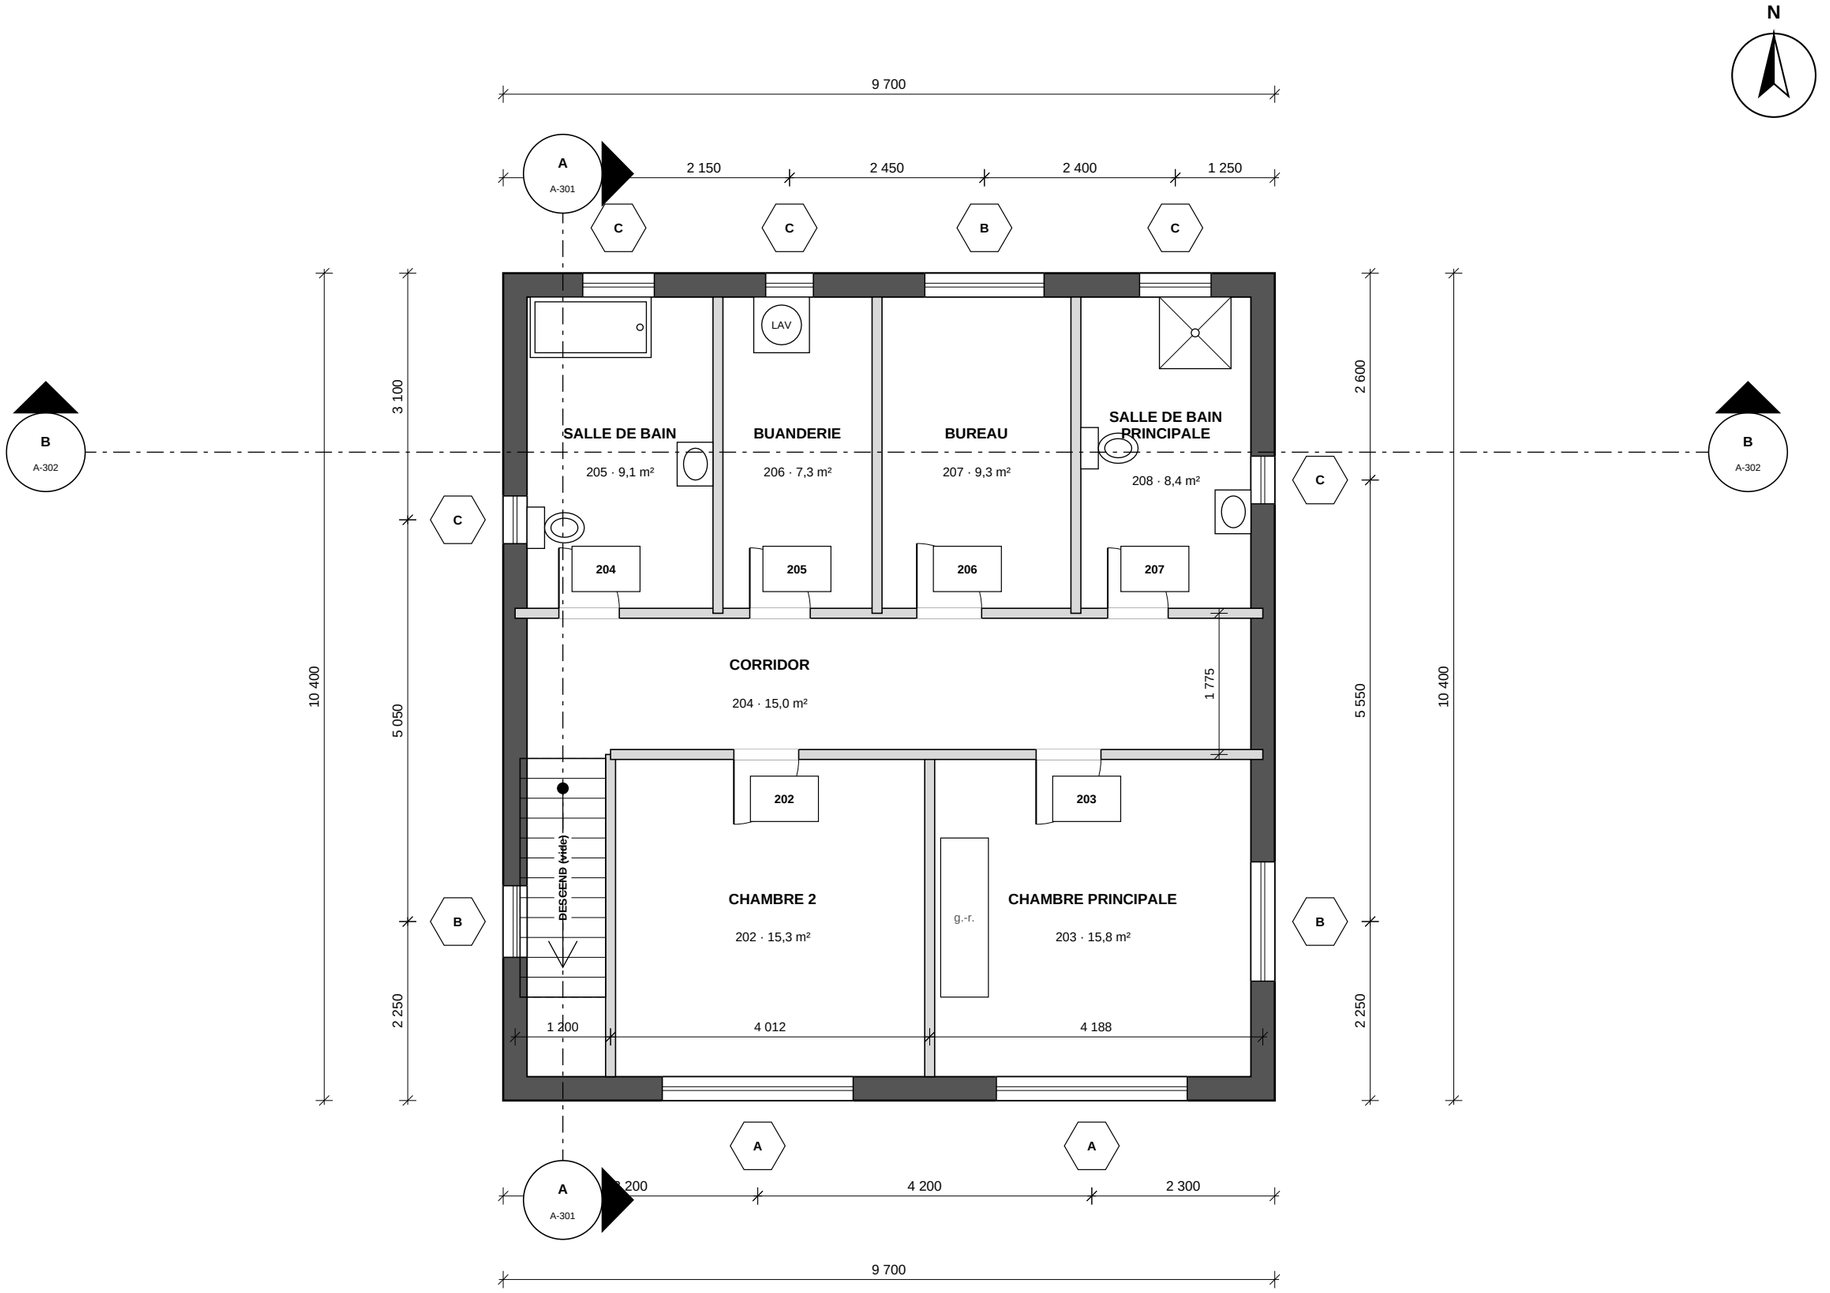

1 **PLAN DE L'ÉTAGE**
Échelle 1:75

Pavillon de L'AVENIR
Centre de formation professionnelle

PLAN D'EXERCICE
LECTURE DE PLANS

PROJET

MAISON UNIFAMILIALE
DOSSIER 1

125, rue des Érables
Ville fictive (Québec)

NOTES GÉNÉRALES

Toutes les cotes sont en millimètres.

Hauteur libre sous plafond : 2 610 mm.

Cage d'escalier ouverte : garde-corps de 900 au pourtour du vide.

L'étage ne couvre que le volume central; les ailes de chaque côté n'ont que le rez-de-chaussée.

Buanderie : drain de plancher et bac de récupération sous la laveuse.

LÉGENDE

Mur extérieur (poché foncé) : voir composition M1, feuille A-301

Mur intérieur (poché pâle) : voir composition M2

Hexagone : type de fenêtre (voir nomenclature, A-301)

Rectangle : numéro de porte (voir nomenclature, A-301)

Cotes en millimètres, aux faces extérieures du revêtement intermédiaire et aux axes des ouvertures

TITRE DE LA FEUILLE

PLAN DE L'ÉTAGE

CONÇU PAR

Jeremy, enseignant

DESSIN À DES FINS D'ENSEIGNEMENT — NE PAS UTILISER POUR LA CONSTRUCTION

ÉCHELLE

1:75


DATE

Octobre 2026


FEUILLE

A-103


Dossier D1

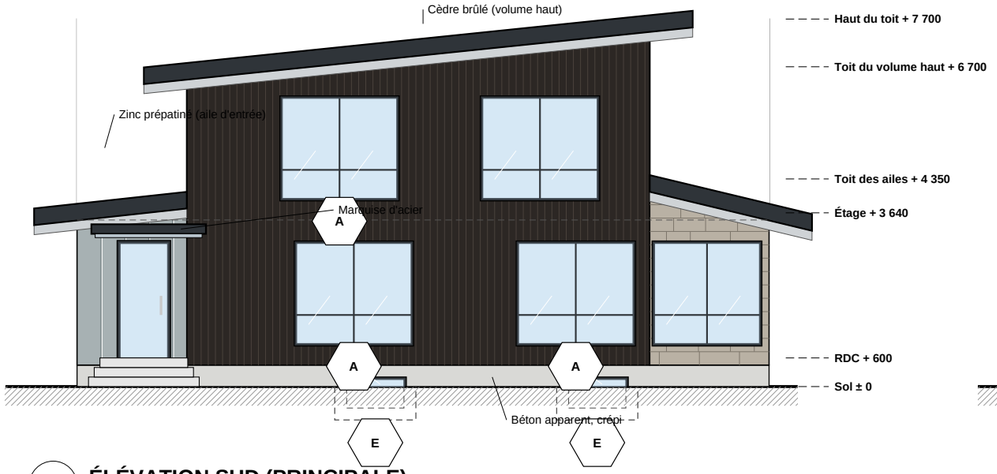


1 **ÉLÉVATION SUD (PRINCIPALE)**
Échelle 1:125

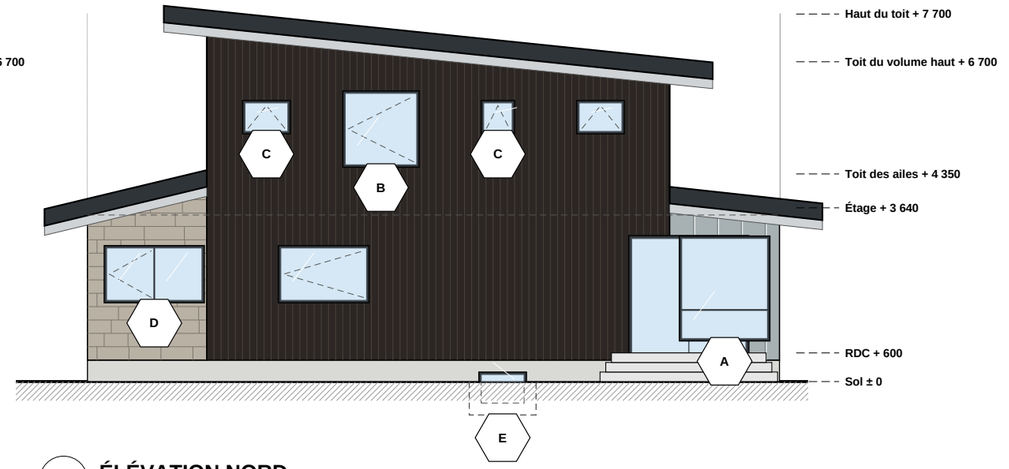

2 **ÉLÉVATION NORD**
Échelle 1:125

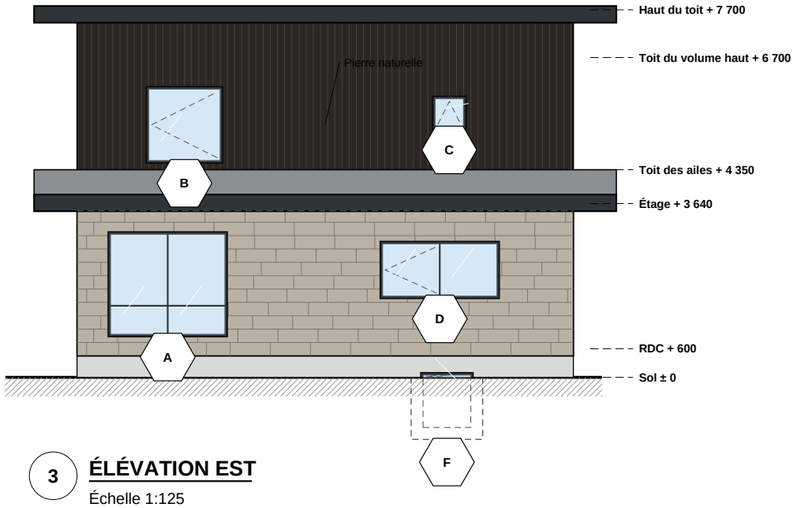

3 **ÉLÉVATION EST**
Échelle 1:125

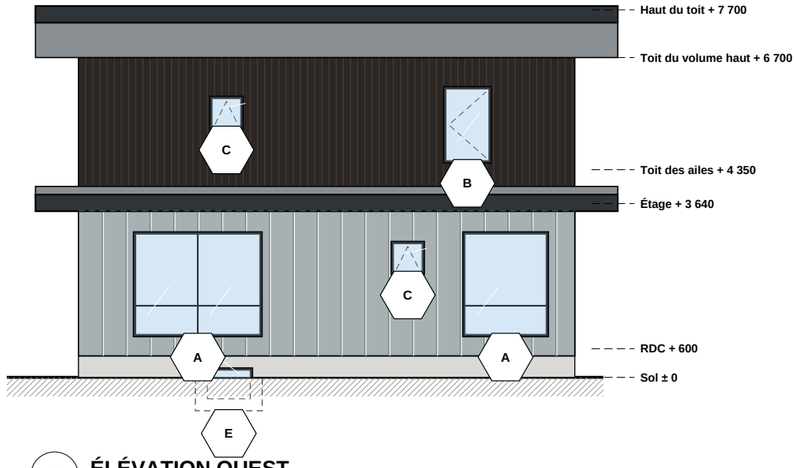

4 **ÉLÉVATION OUEST**
Échelle 1:125

Pavillon de L'AVENIR
Centre de formation professionnelle

PLAN D'EXERCICE
LECTURE DE PLANS

PROJET

MAISON UNIFAMILIALE
DOSSIER 1

125, rue des Érables
Ville fictive (Québec)

NOTES D'ÉLÉVATION

Revêtements : pierre naturelle (entrée et mur est), zinc prépatiné à joints debout (versant bas), cèdre brûlé (volume haut).

Marquise d'acier en porte-à-faux au-dessus de l'entrée.

Deux toits monopentes décalés (pente d'environ 4 %) : débords de 900, bandeau d'aluminium noir; bande vitrée haute entre les deux versants (vue sur l'élévation ouest).

Fenêtres à cadre noir, verre triple. Hexagones : types de fenêtres, voir A-301.

Fenêtres du sous-sol : margelles galvanisées (en tirets).

NIVEAUX

Sol : ± 0

Sous-sol : – 2 100

RDC : + 600

Étage : + 3 640

Toit des ailes : + 4 350

Toit du volume haut : + 6 700

Haut du toit : + 7 700

TITRE DE LA FEUILLE

ÉLÉVATIONS

CONÇU PAR

Jeremy, enseignant

DESSIN À DES FINS D'ENSEIGNEMENT — NE PAS UTILISER POUR LA CONSTRUCTION

ÉCHELLE

1:125


DATE

Octobre 2026

FEUILLE

A-201

Dossier D1

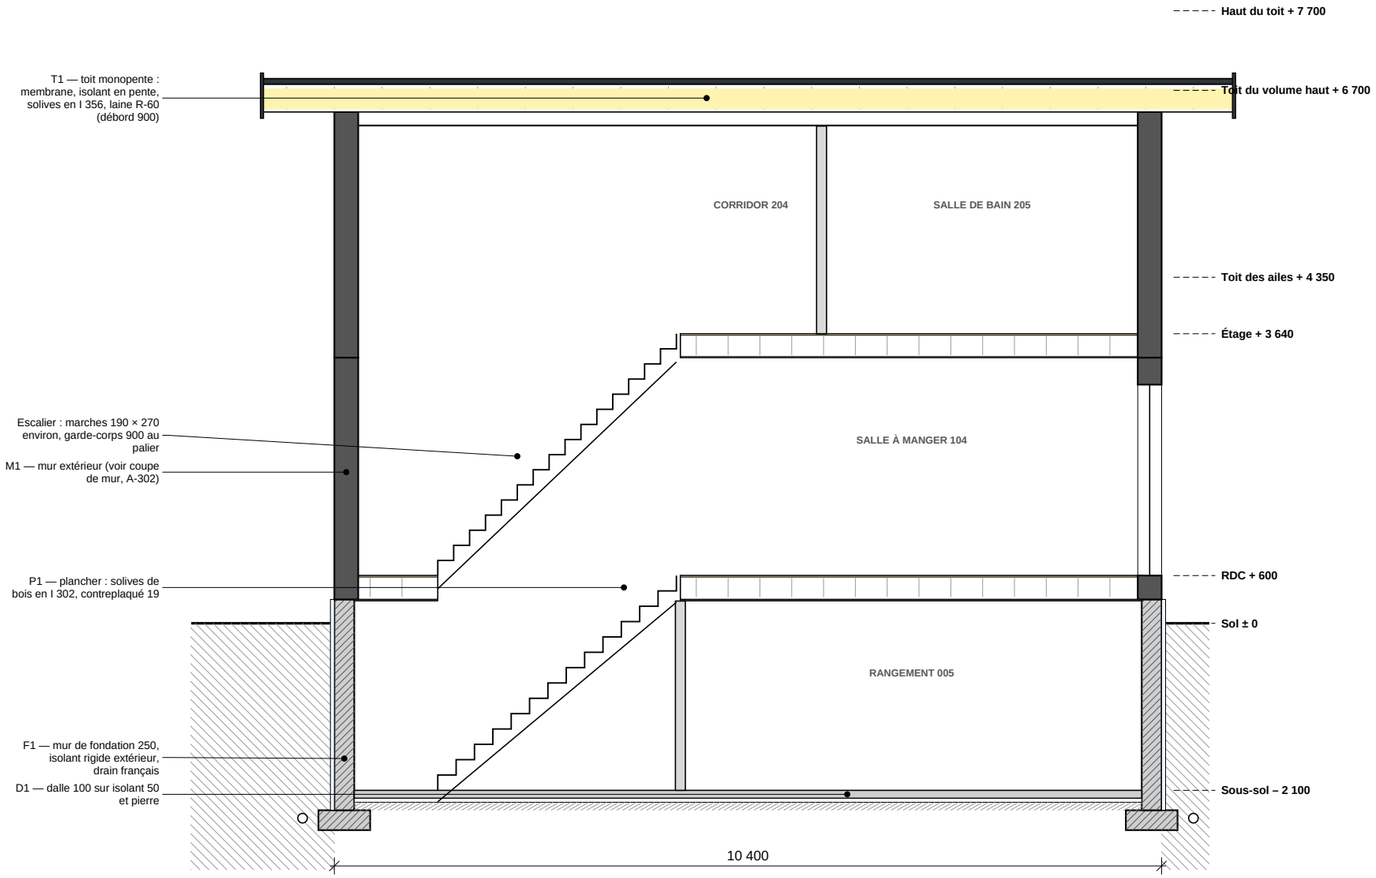

A — COUPE A — TRANSVERSALE (vers l'est)

Échelle 1:75

NOMENCLATURE DES PORTES

No	Dimensions (mm)	Type	Matériau	Quincaillerie
001	860 × 2 030	Battante	Âme pleine, MDF peint	Passage
002	815 × 2 030	Battante	Âme pleine, MDF peint	Passage
003	760 × 2 030	Battante	Âme pleine, MDF peint	Intimité (verrou)
004	815 × 2 030	Battante	Âme pleine, MDF peint	Passage
101	1 000 × 2 400	Battante	Acier isolé, vitrage pleine hauteur	Serrure + pêne dormant
102	2 400 × 2 400	Coulissante	PVC, vitrage triple	Loquet + barre de sécurité
103	860 × 2 030	Battante	Âme pleine, MDF peint	Passage
104	760 × 2 030	Battante	Âme pleine, MDF peint	Intimité (verrou)
202	815 × 2 030	Battante	Âme pleine, MDF peint	Passage
203	815 × 2 030	Battante	Âme pleine, MDF peint	Passage
204	760 × 2 030	Battante	Âme pleine, MDF peint	Intimité (verrou)
205	760 × 2 030	Battante	Âme pleine, MDF peint	Passage
206	815 × 2 030	Battante	Âme pleine, MDF peint	Passage
207	760 × 2 030	Battante	Âme pleine, MDF peint	Intimité (verrou)

NOMENCLATURE DES FENÊTRES

Type	Qté	Larg. × haut. (mm)	Allège	Ouverture	Vitrage
A	9	Variable (A-201) × 2 100	300	Fixe et battant (pleine hauteur)	Triple, faible émissivité, argon
B	3	900 / 1 500 × 1 500	900	Battant, à manivelle	Triple, faible émissivité, argon
C	6	600 / 900 × 600	1 600	Auvent	Triple, givré
D	3	1 800 / 2 000 / 2 400 × 1 100	1 100	Battant, à manivelle	Triple, faible émissivité
E	4	900 / 1 200 × 600	1 650	Coulissante (sous-sol)	Double, faible émissivité
F	1	1 000 × 1 100	1 050	Battant — issue (margelle)	Double, faible émissivité

Pavillon de L'AVENIR
Centre de formation professionnelle

PLAN D'EXERCICE
LECTURE DE PLANS

PROJET

MAISON UNIFAMILIALE
DOSSIER 1

125, rue des Érables
Ville fictive (Québec)

COMPOSITIONS

T1 — Toit monopente (débord 900) : membrane élastomère 2 plis, isolant rigide en pente, contreplaqué 19, solives en I 356, laine soufflée R-60, pare-vapeur, gypse 12,7.

M1 — Mur extérieur : zinc à joints debout (ou pierre, ou cèdre brûlé), fourrures 19, isolant rigide 50, OSB 11, montants 38 × 140 à 400 c/c, laine R-24, pare-vapeur, gypse 12,7.

M2 — Cloison : gypse 12,7 deux faces, montants 38 × 89 à 400 c/c (laine insonorisante autour des salles de bain).

P1 — Plancher : contreplaqué 19 collé-vissé, solives en I 302 à 400 c/c.

D1 — Dalle du sous-sol : béton 100, isolant rigide 50, pierre 200.

F1 — Fondation : mur de béton 250, isolant rigide 50 extérieur, semelle 650 × 250, drain français.

À OBSERVER

L'allège se mesure à partir du plancher du niveau où se trouve la fenêtre.

Fenêtres E et F : sous-sol (voir les margelles sur A-201).

TITRE DE LA FEUILLE

COUPE TRANSVERSALE ET NOMENCLATURES

CONÇU PAR

Jeremy, enseignant

DESSIN À DES FINS D'ENSEIGNEMENT — NE PAS UTILISER POUR LA CONSTRUCTION

ÉCHELLE

1:75


DATE

Octobre 2026

FEUILLE

A-301

Dossier D1

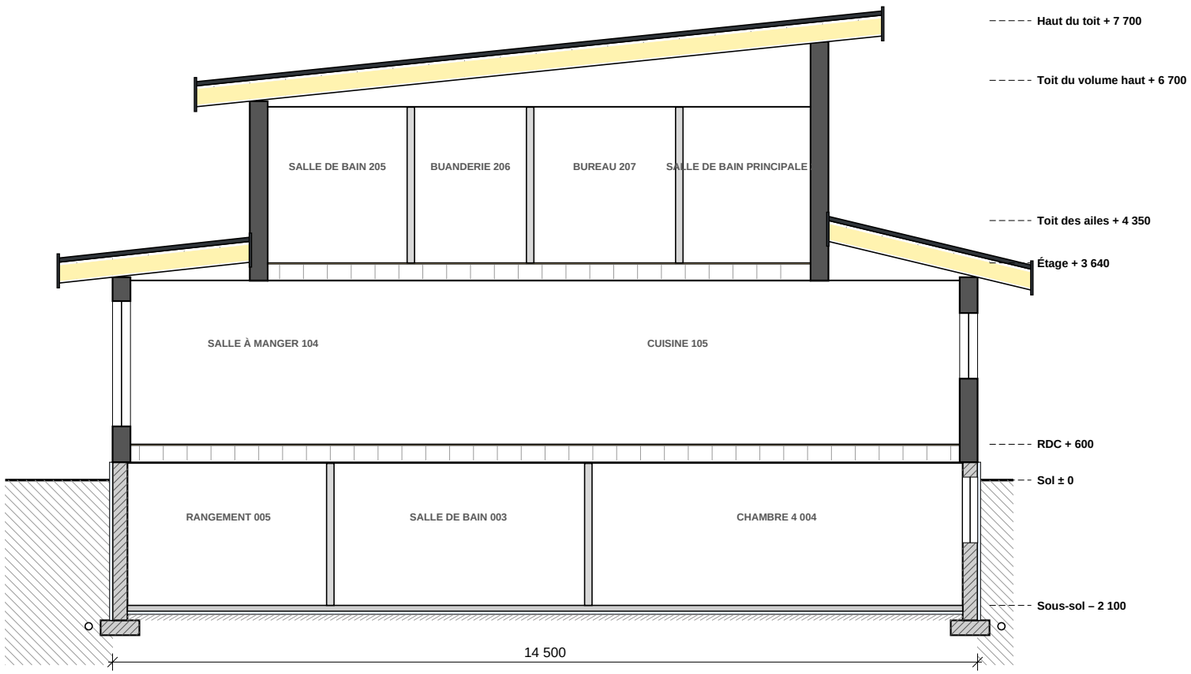


B — COUPE B — LONGITUDINALE (vers le nord)

Échelle 1:100

LÉGENDE DES MATÉRIAUX EN COUPE

- Béton coulé
- Sol naturel (terre)
- Pierre concassée, pierre nette
- Brique d'argile
- Bloc de béton
- Isolant rigide (panneau)
- Isolant en natte (laine)
- Bois de charpente coupé
- Contreplaqué ou OSB
- Plaque de plâtre (gypse)
- Acier
- Lame d'air, vide

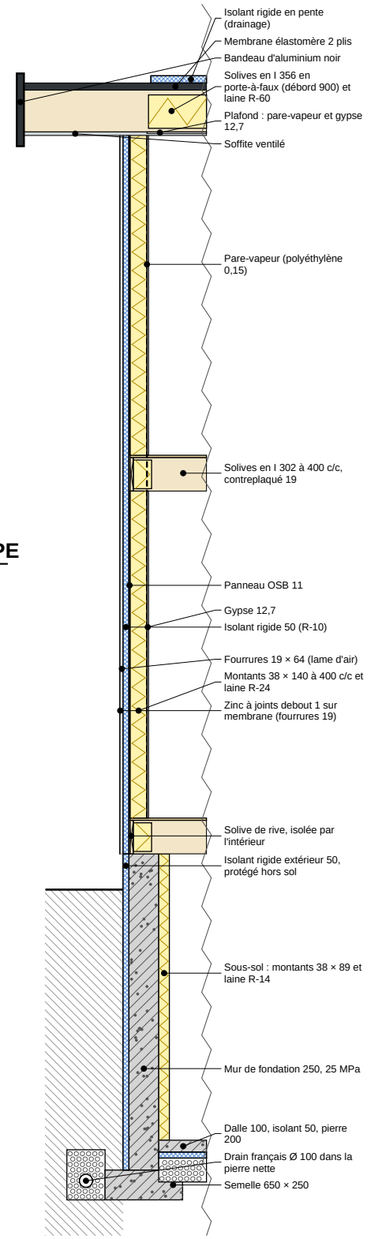

2 — COUPE DE MUR TYPE

Échelle 1:50

Pavillon de L'AVENIR
Centre de formation professionnelle

PLAN D'EXERCICE
LECTURE DE PLANS

PROJET

MAISON UNIFAMILIALE
DOSSIER 1

125, rue des Érables
Ville fictive (Québec)

À OBSERVER

La coupe B est prise sur la ligne B des plans A-101 à A-103, en regardant vers le nord.

Repérer les trois niveaux : sous-sol, rez-de-chaussée, étage. Comparer avec A-201 et A-301.

Coupe de mur : de la semelle jusqu'au parapet, de l'extérieur vers l'intérieur.

COMPOSITIONS

T1 — Toit monopente (débord 900) : membrane élastomère 2 plis, isolant rigide en pente, contreplaqué 19, solives en I 356, laine soufflée R-60, pare-vapeur, gypse 12,7.

M1 — Mur extérieur : zinc à joints debout (ou pierre, ou cèdre brûlé), fourrures 19, isolant rigide 50, OSB 11, montants 38 × 140 à 400 c/c, laine R-24, pare-vapeur, gypse 12,7.

M2 — Cloison : gypse 12,7 deux faces, montants 38 × 89 à 400 c/c (laine insonorisante autour des salles de bain).

P1 — Plancher : contreplaqué 19 collé-vissé, solives en I 302 à 400 c/c.

D1 — Dalle du sous-sol : béton 100, isolant rigide 50, pierre 200.

F1 — Fondation : mur de béton 250, isolant rigide 50 extérieur, semelle 650 × 250, drain français.

TITRE DE LA FEUILLE

COUPE LONGITUDINALE, COUPE DE MUR ET MATÉRIAUX

CONÇU PAR

Jeremy, enseignant

DESSIN À DES FINS D'ENSEIGNEMENT — NE PAS UTILISER POUR LA CONSTRUCTION

ÉCHELLE

1:100 et 1:50


DATE

Octobre 2026


FEUILLE

A-302

Dossier D1

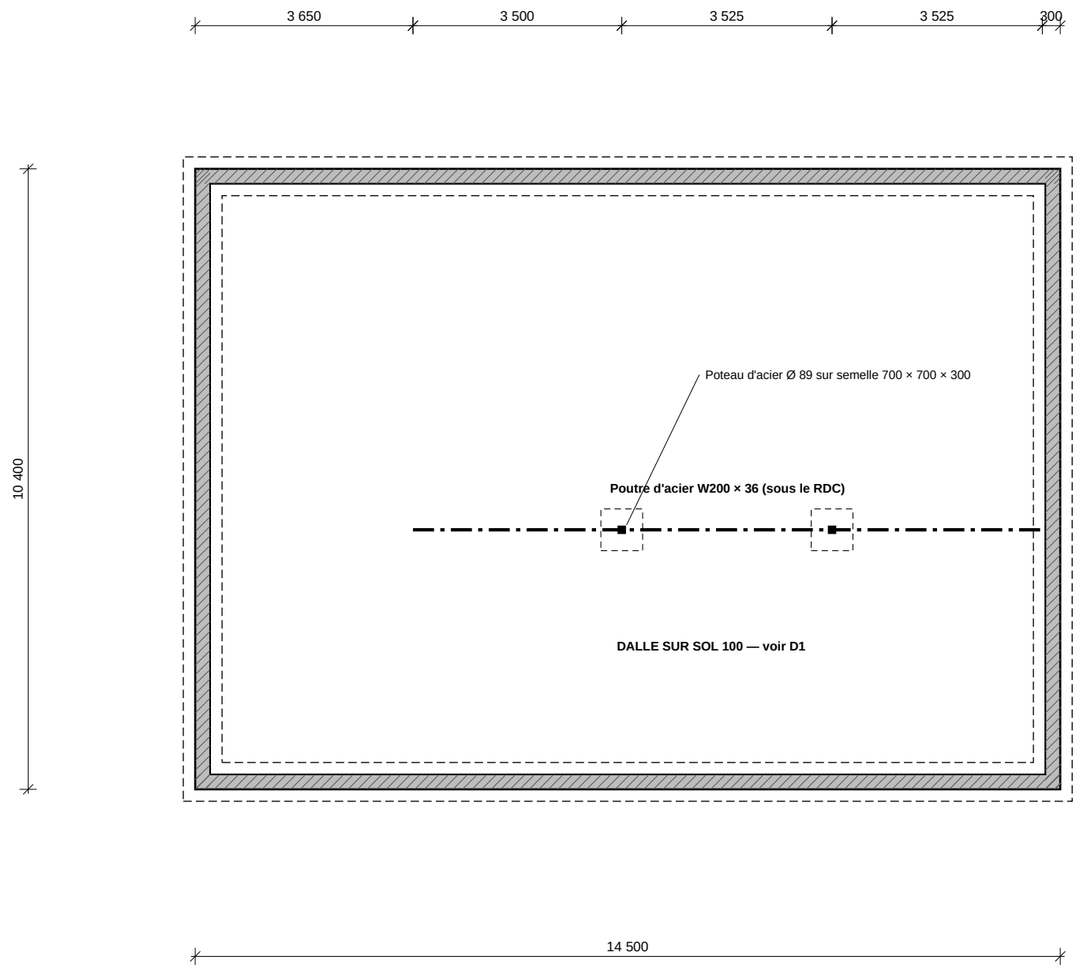

1 **PLAN DES FONDATIONS**
Échelle 1:100

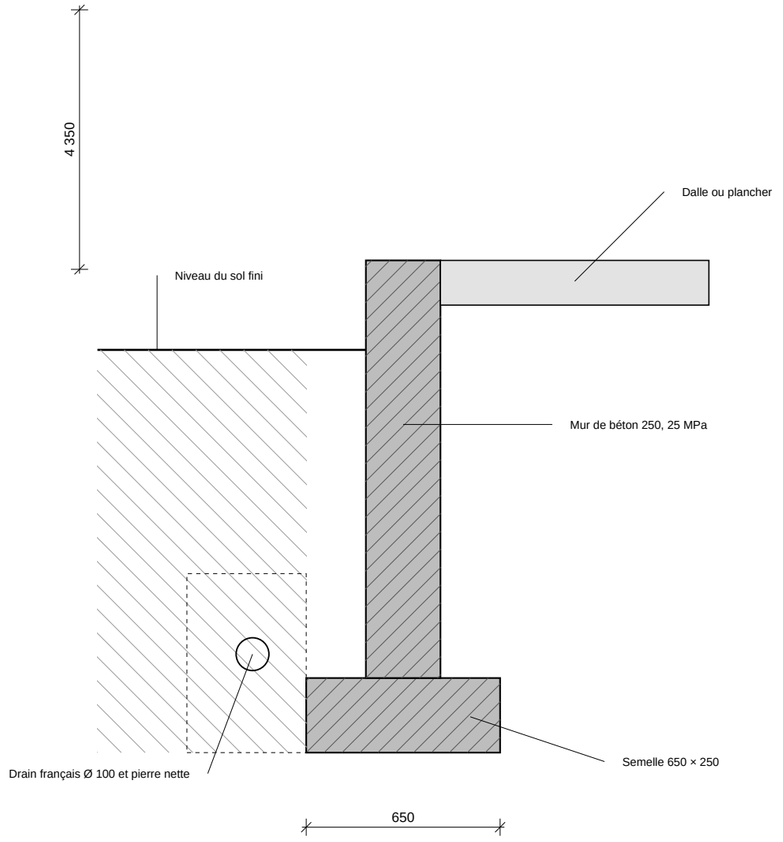

2 **DÉTAIL TYPE — SEMELLE ET MUR**
Échelle 1:20

Pavillon de L'AVENIR
Centre de formation professionnelle

PLAN D'EXERCICE
LECTURE DE PLANS

PROJET

MAISON UNIFAMILIALE
DOSSIER 1

125, rue des Érables
Ville fictive (Québec)

NOTES DE STRUCTURE

Béton : 25 MPa à 28 jours, air entraîné 5 à 8 %.

Semelles à 1 600 mm minimum sous le sol fini (gel); ici le dessous est à 2 600.

Murs de fondation 250 armés, isolant rigide 50 à l'extérieur, membrane d'étanchéité, drain français.

Capacité portante présumée : 75 kPa. Faire valider par un ingénieur.

Solives du RDC appuyées sur la poutre d'acier.

LÉGENDE

Poché hachuré : mur de fondation en béton coulé

Tirets : semelle (sous le niveau du plancher)

Carré plein : poteau · carré en tirets : semelle isolée

— · — Poutre porteuse

TITRE DE LA FEUILLE


PLAN DES FONDATIONS ET DÉTAIL TYPE

CONÇU PAR
Jeremy, enseignant
DESSIN À DES FINS D'ENSEIGNEMENT — NE PAS UTILISER POUR LA CONSTRUCTION

ÉCHELLE
1:100 et 1:20

DATE
Octobre 2026

FEUILLE
S-101
Dossier D1

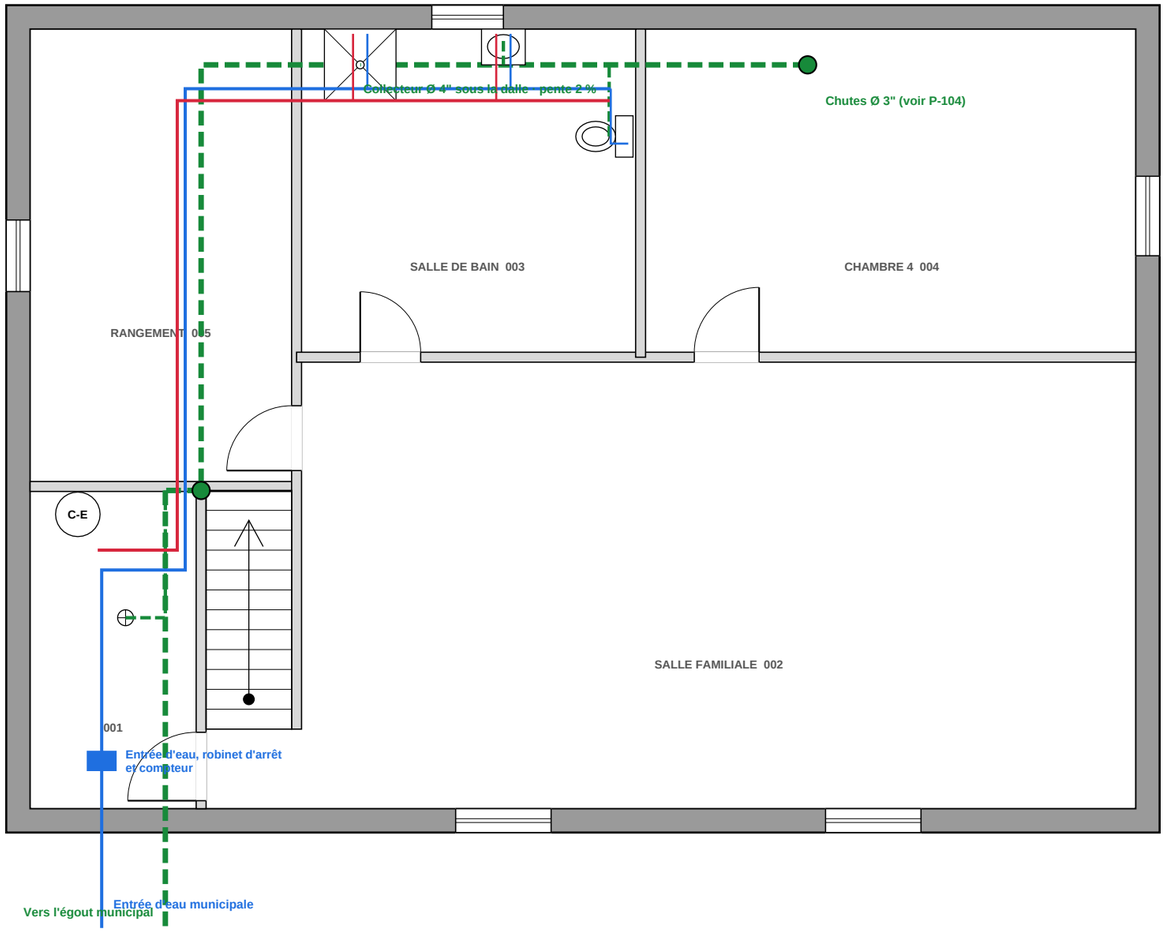

N

0 2 4 6 8 10 m

1 PLAN DE PLOMBERIE
Échelle 1:75

Pavillon de L'AVENIR
Centre de formation professionnelle

PLAN D'EXERCICE
LECTURE DE PLANS

PROJET

MAISON UNIFAMILIALE
DOSSIER 1

125, rue des Érables
Ville fictive (Québec)

NOTES DE PLOMBERIE

Collecteur principal sous la dalle : ABS cédule 40, pente 2 %.

Clapet antiretour sur le collecteur, accessible (regard).

Chauffe-eau électrique 270 L : soupape T et P raccordée à 150 mm du sol.

Drain de plancher de la salle mécanique avec amorceur de siphon.

Les colonnes de chute montent jusqu'au toit (voir P-104).

LÉGENDE

- Eau froide (EF)
- Eau chaude (EC)
- Drainage sanitaire
- Ventilation (évent)
- Colonne de chute

TITRE DE LA FEUILLE

PLOMBERIE
SOUS-SOL

CONÇU PAR
Jeremy, enseignant


DESSIN À DES FINS D'ENSEIGNEMENT — NE PAS UTILISER POUR LA CONSTRUCTION

ÉCHELLE
1:75

DATE
Octobre 2026

FEUILLE
P-101
Dossier D1

N

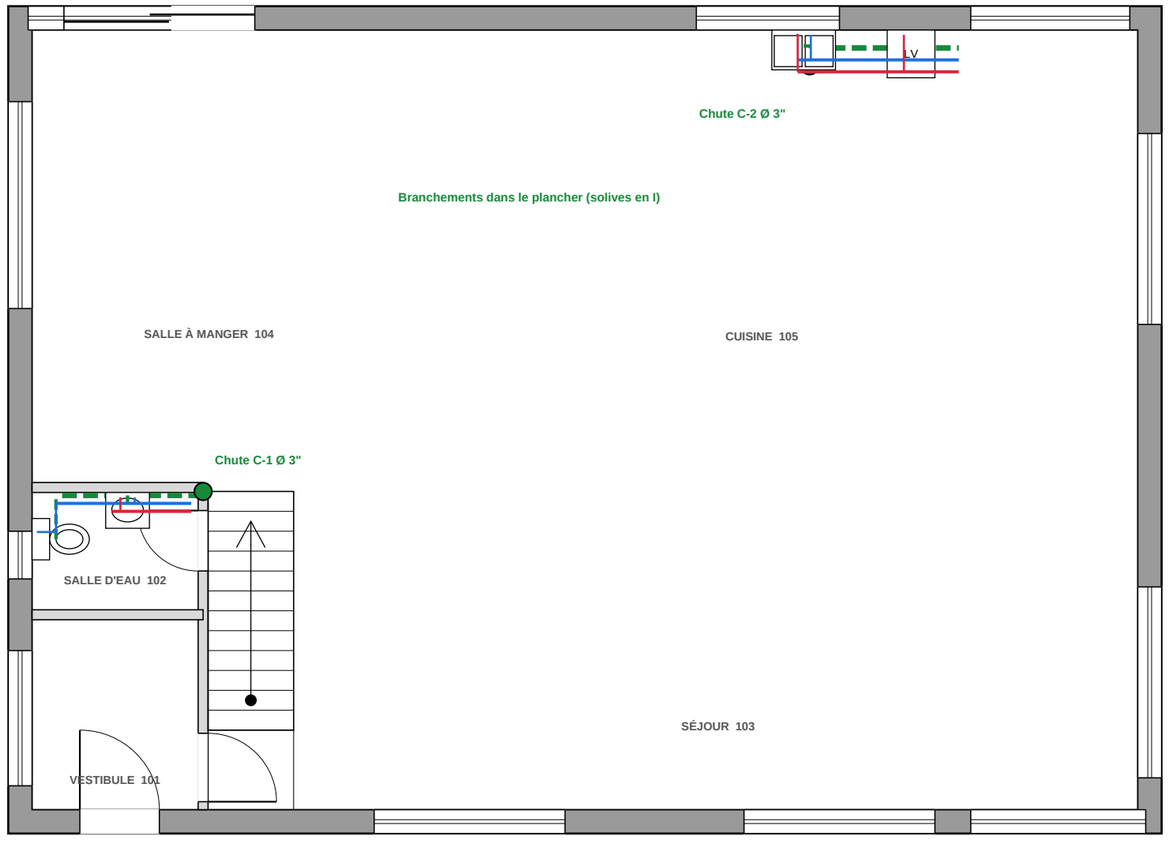

0 2 4 6 8 10 m

1 PLAN DE PLOMBERIE
Échelle 1:75

Pavillon de L'AVENIR
Centre de formation professionnelle

PLAN D'EXERCICE
LECTURE DE PLANS

PROJET

MAISON UNIFAMILIALE
DOSSIER 1

125, rue des Érables
Ville fictive (Québec)

NOTES DE PLOMBERIE

Branchements dans l'épaisseur du plancher, vers les chutes C-1 et C-2.

Lave-vaisselle raccordé au siphon de l'évier (boucle anti-retour).

Eau : PEX, robinet d'arrêt sur chaque alimentation d'appareil.

LÉGENDE

- Eau froide (EF)
- Eau chaude (EC)
- Drainage sanitaire
- Ventilation (évent)
- Colonne de chute

TITRE DE LA FEUILLE

PLOMBERIE
REZ-DE-CHAUSSÉE

CONÇU PAR
Jeremy, enseignant


DESSIN À DES FINS D'ENSEIGNEMENT — NE PAS UTILISER POUR LA CONSTRUCTION

ÉCHELLE
1:75

DATE
Octobre 2026

FEUILLE
P-102
Dossier D1

N

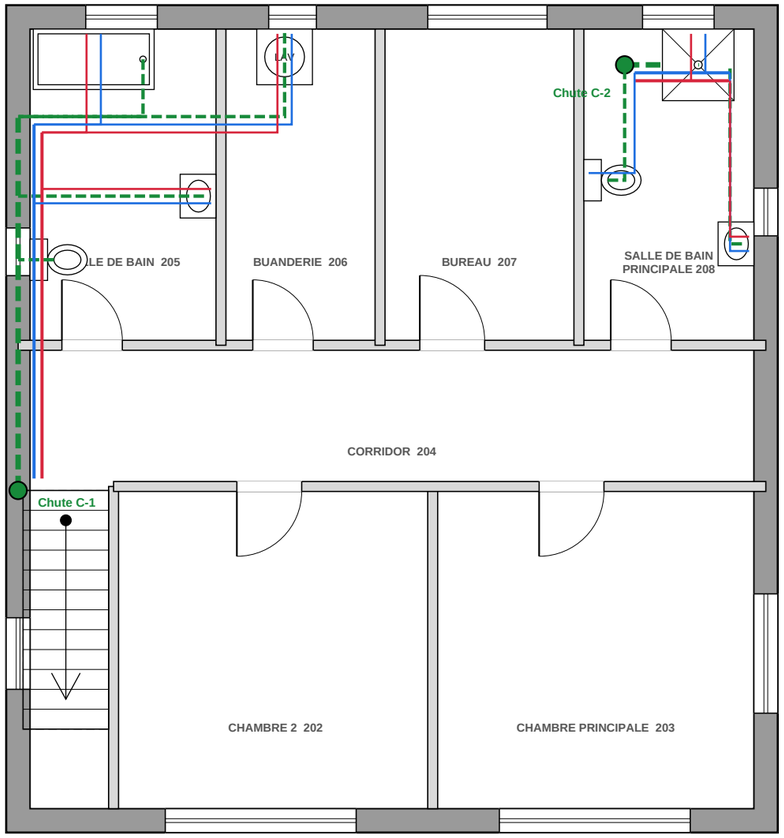

1 **PLAN DE PLOMBERIE**
Échelle 1:75

0 2 4 6 8 10 m

Pavillon de L'AVENIR
Centre de formation professionnelle

PLAN D'EXERCICE
LECTURE DE PLANS

PROJET

MAISON UNIFAMILIALE
DOSSIER 1

125, rue des Érables
Ville fictive (Québec)

NOTES DE PLOMBERIE

Branchements dans le plancher de l'étage (solives en I percées selon le fabricant).

Laveuse : boîte de raccordement encastrée et bac de récupération.

Douche : drain linéaire, membrane d'étanchéité sous la céramique.

LÉGENDE

- Eau froide (EF)
- Eau chaude (EC)
- Drainage sanitaire
- Ventilation (évent)
- Colonne de chute

TITRE DE LA FEUILLE

PLOMBERIE
ÉTAGE


CONÇU PAR
Jeremy, enseignant

DESSIN À DES FINS D'ENSEIGNEMENT —
NE PAS UTILISER POUR LA CONSTRUCTION

ÉCHELLE
1:75

DATE
Octobre 2026

FEUILLE
P-103
Dossier D1

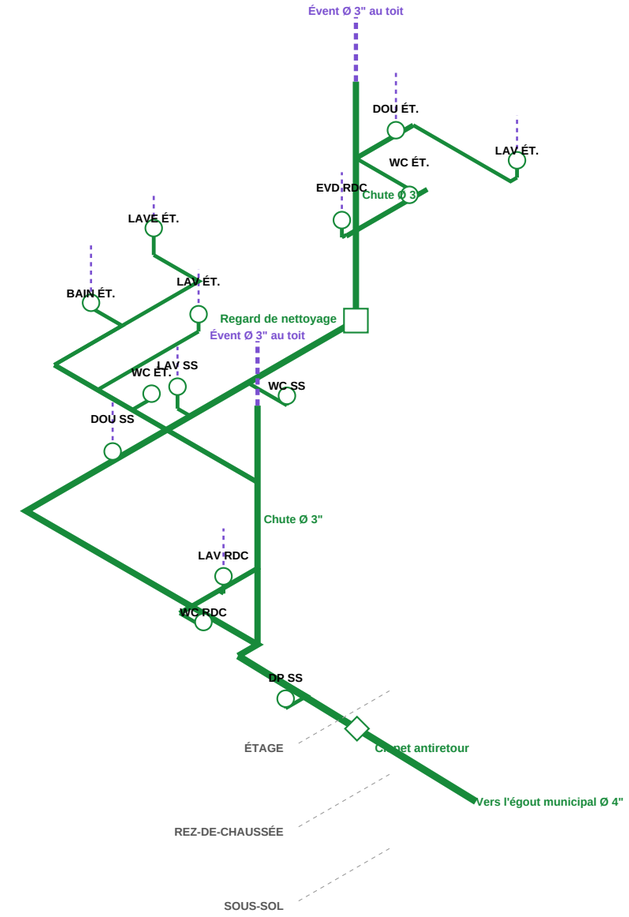

1 SCHÉMA ISOMÉTRIQUE — DRAINAGE ET VENTILATION (3 NIVEAUX)

Échelle sans échelle

NOMENCLATURE DES APPAREILS SANITAIRES

Code	Appareil	Qté	EF	EC	Drain	Évent	Unités
CE	Chauffe-eau électrique 270 L	1	3/4"	3/4"	—	—	0
DP	Drain de plancher	1	—	—	3"	—	2
DOU	Douche	2	1/2"	1/2"	2"	1 1/2"	3,0
WC	Toilette (réservoir 6 L)	4	1/2"	—	3"	2"	16
LAV	Lavabo	4	1/2"	1/2"	1 1/4"	1 1/4"	4
EVD	Évier de cuisine double	1	1/2"	1/2"	1 1/2"	1 1/4"	1,5
LV	Lave-vaisselle	1	—	1/2"	(évier)	—	1
BAIN	Baignoire	1	1/2"	1/2"	1 1/2"	1 1/4"	1,5
LAVE	Laveuse (tuyau de rejet)	1	1/2"	1/2"	2"	1 1/2"	1,5
	TOTAL DES UNITÉS (charge hydraulique)						30,5

Pavillon de L'AVENIR
Centre de formation professionnelle

PLAN D'EXERCICE
LECTURE DE PLANS

PROJET

MAISON UNIFAMILIALE
DOSSIER 1

125, rue des Érables
Ville fictive (Québec)

À OBSERVER

Les deux colonnes de chute traversent les trois niveaux et se prolongent en évent au-dessus du toit.

Aux étages, les branchements passent dans l'épaisseur du plancher (solives en I).

Au sous-sol, le collecteur est sous la dalle; il sort vers la rue sous la semelle.

Chaque appareil a son siphon et son évent. Pente minimale 1 : 50 (2 %).

TITRE DE LA FEUILLE

SCHÉMA ISOMÉTRIQUE ET NOMENCLATURE DES APPAREILS

CONÇU PAR

Jeremy, enseignant

DESSIN À DES FINS D'ENSEIGNEMENT — NE PAS UTILISER POUR LA CONSTRUCTION

ÉCHELLE

Sans échelle


DATE

Octobre 2026

FEUILLE

P-104

Dossier D1

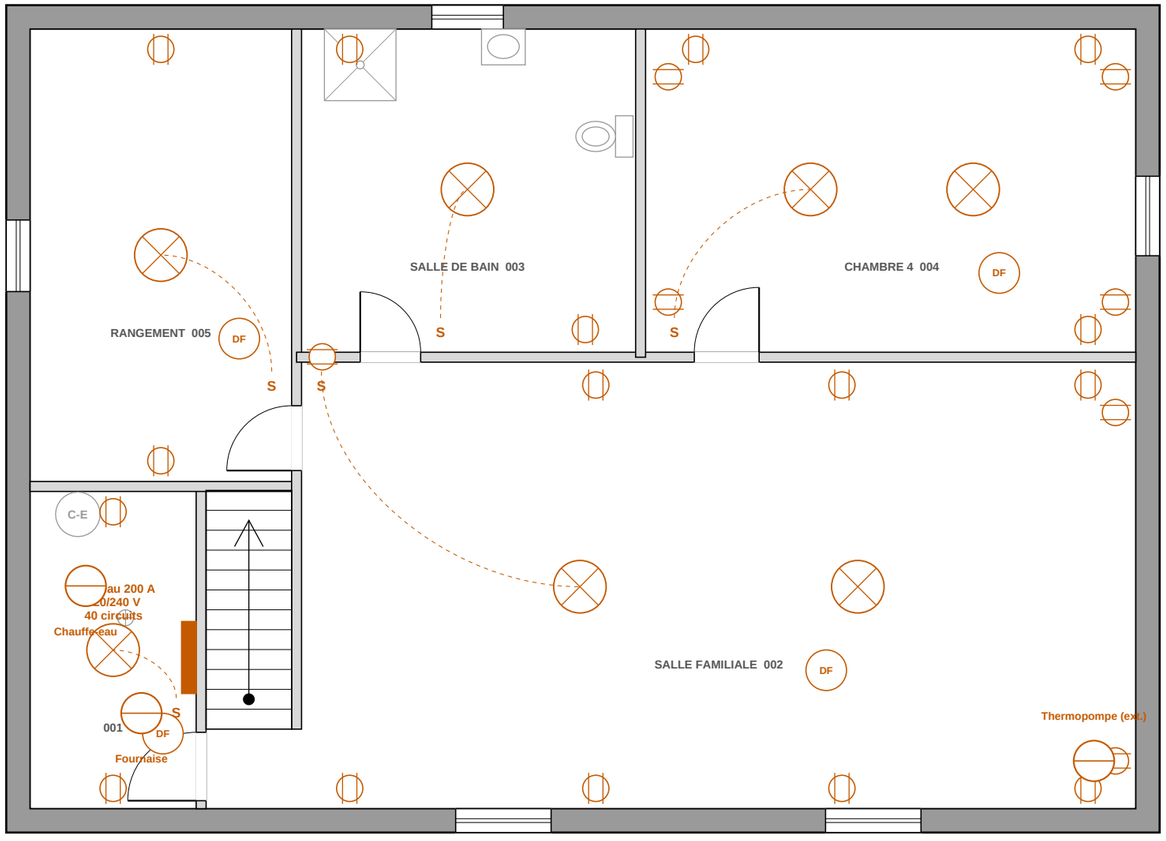

1 **PLAN D'ÉLECTRICITÉ**
Échelle 1:75

Pavillon de L'AVENIR
Centre de formation professionnelle

PLAN D'EXERCICE
LECTURE DE PLANS

PROJET

MAISON UNIFAMILIALE
DOSSIER 1

125, rue des Érables
Ville fictive (Québec)

NOTES D'ÉLECTRICITÉ

Installation selon le Code de construction du Québec, chapitre V — Électricité.

Entrée électrique souterraine jusqu'au panneau de la salle mécanique.

Avertisseurs de fumée et de CO reliés entre eux à chaque niveau.

Prises de la salle de bain : protection DDFT.

LÉGENDE

- Prise de courant double 15 A
- Luminaire au plafond
- S — Interrupteur unipolaire
- DF — Avertisseur de fumée relié
- Prise 240 V ou appareil dédié
- Panneau de distribution

CIRCUITS (EXTRAIT)

No	Usage	Charge	Disj.
1	Prises et éclairage — Salle mécani	15 A	1 × 15 A
2	Prises et éclairage — Salle famili	15 A	1 × 15 A
3	Prises et éclairage — Salle de bai	15 A	1 × 15 A
4	Prises et éclairage — Chambre 4	15 A	1 × 15 A
5	Prises et éclairage — Rangement	15 A	1 × 15 A
6	Chauffe-eau	30 A 240 V	2 × 30 A
7	Fournaise	100 A 240 V	2 × 100 A
8	Thermopompe (ext.)	30 A 240 V	2 × 30 A

TITRE DE LA FEUILLE

ÉLECTRICITÉ
SOUS-SOL


CONÇU PAR
Jeremy, enseignant

DESSIN À DES FINS D'ENSEIGNEMENT — NE PAS UTILISER POUR LA CONSTRUCTION

ÉCHELLE
1:75

DATE
Octobre 2026

FEUILLE
E-101
Dossier D1

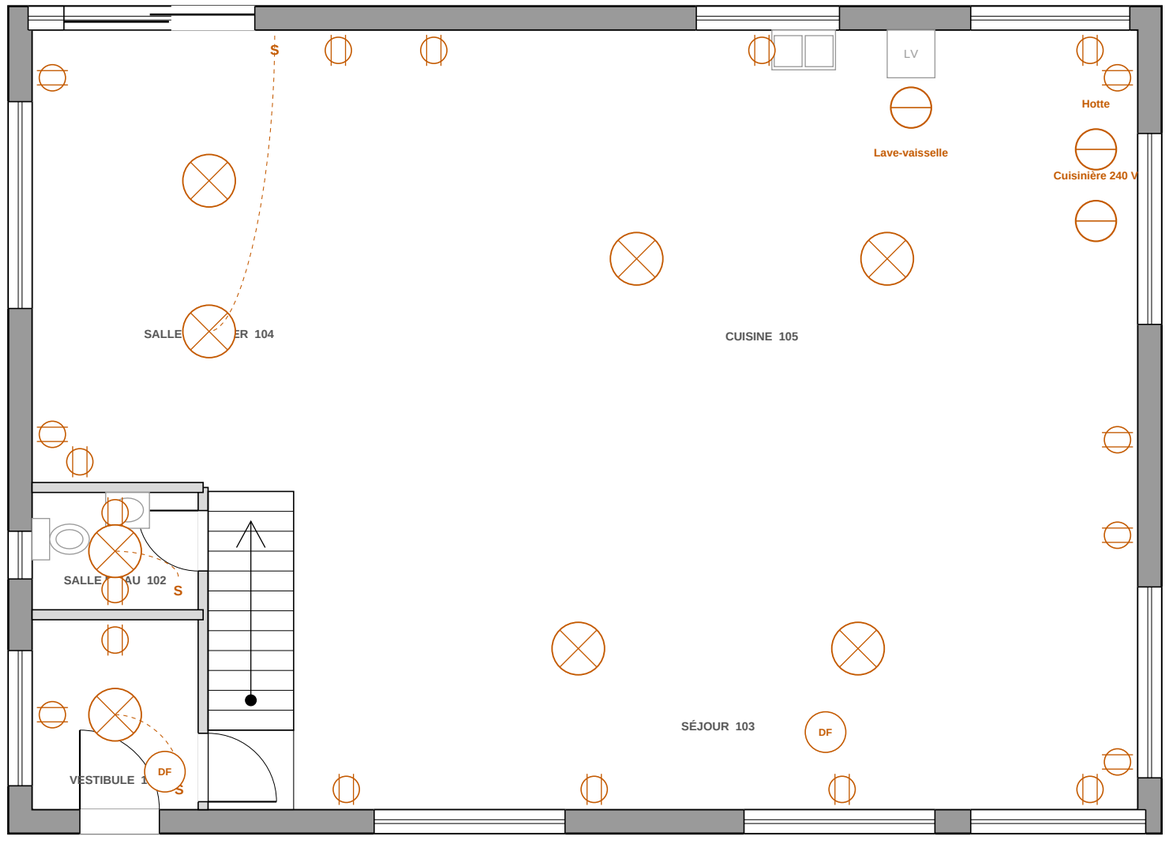

1 **PLAN D'ÉLECTRICITÉ**
Échelle 1:75

N

Pavillon de L'AVENIR
Centre de formation professionnelle

PLAN D'EXERCICE
LECTURE DE PLANS

PROJET

MAISON UNIFAMILIALE
DOSSIER 1

125, rue des Érables
Ville fictive (Québec)

NOTES D'ÉLECTRICITÉ

Prises du comptoir : circuits de 20 A avec prises T, protection DDFT près de l'évier.

Éclairage encastré DEL au séjour et à la cuisine.

Aucun point le long d'un mur à plus de 1,8 m d'une prise.

LÉGENDE

- Prise de courant double 15 A
- Luminaire au plafond
- S — Interrupteur unipolaire
- DF — Avertisseur de fumée relié
- Prise 240 V ou appareil dédié
- Panneau de distribution

CIRCUITS (EXTRAIT)

No	Usage	Charge	Disj.
1	Prises et éclairage — Vestibule	15 A	1 × 15 A
2	Prises et éclairage — Salle d'eau	15 A	1 × 15 A
3	Prises et éclairage — Séjour	15 A	1 × 15 A
4	Prises et éclairage — Salle à mang	15 A	1 × 15 A
5	Prises et éclairage — Cuisine	15 A	1 × 15 A
6	Cuisinière 240 V	40 A 240 V	2 × 40 A
7	Lave-vaisselle	15 A 120 V	1 × 15 A
8	Hotte	15 A 120 V	1 × 15 A

TITRE DE LA FEUILLE

ÉLECTRICITÉ
REZ-DE-CHAUSSÉE


CONÇU PAR
Jeremy, enseignant

DESSIN À DES FINS D'ENSEIGNEMENT — NE PAS UTILISER POUR LA CONSTRUCTION

ÉCHELLE
1:75

DATE
Octobre 2026

FEUILLE
E-102
Dossier D1

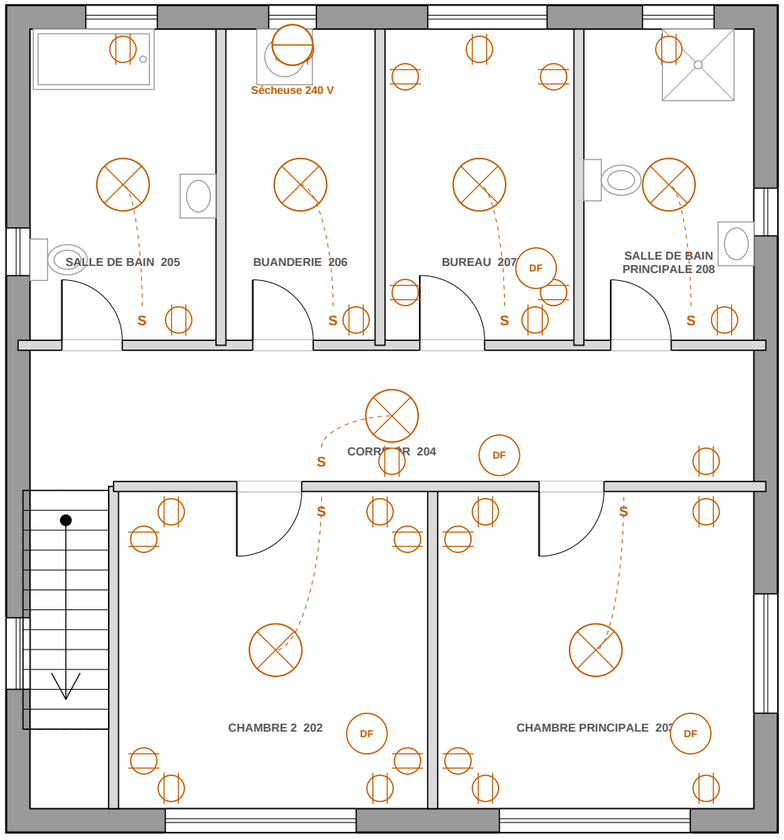

1 **PLAN D'ÉLECTRICITÉ**
Échelle 1:75

N

Pavillon de L'AVENIR
Centre de formation professionnelle

PLAN D'EXERCICE
LECTURE DE PLANS

PROJET

MAISON UNIFAMILIALE
DOSSIER 1

125, rue des Érables
Ville fictive (Québec)

NOTES D'ÉLECTRICITÉ

Chambres : prises protégées par disjoncteur anti-arcs (AFCI).

Avertisseurs de fumée et de CO dans le corridor et dans chaque chambre, reliés entre eux.

Ventilateurs des salles de bain sur minuterie (reliés au VRC).

LÉGENDE

- Prise de courant double 15 A
- Luminaire au plafond
- S — Interrupteur unipolaire
- DF — Avertisseur de fumée relié
- Prise 240 V ou appareil dédié
- Panneau de distribution

CIRCUITS (EXTRAIT)

No	Usage	Charge	Disj.
1	Prises et éclairage — Chambre 2	15 A	1 × 15 A
2	Prises et éclairage — Chambre prin	15 A	1 × 15 A
3	Prises et éclairage — Corridor	15 A	1 × 15 A
4	Prises et éclairage — Salle de bai	15 A	1 × 15 A
5	Prises et éclairage — Buanderie	15 A	1 × 15 A
6	Prises et éclairage — Bureau	15 A	1 × 15 A
7	Prises et éclairage — Salle de bai	15 A	1 × 15 A
8	Sécheuse 240 V	30 A 240 V	2 × 30 A

TITRE DE LA FEUILLE

ÉLECTRICITÉ
ÉTAGE

CONÇU PAR
Jeremy, enseignant


DESSIN À DES FINS D'ENSEIGNEMENT — NE PAS UTILISER POUR LA CONSTRUCTION

ÉCHELLE
1:75

DATE
Octobre 2026

FEUILLE
E-103
Dossier D1

N

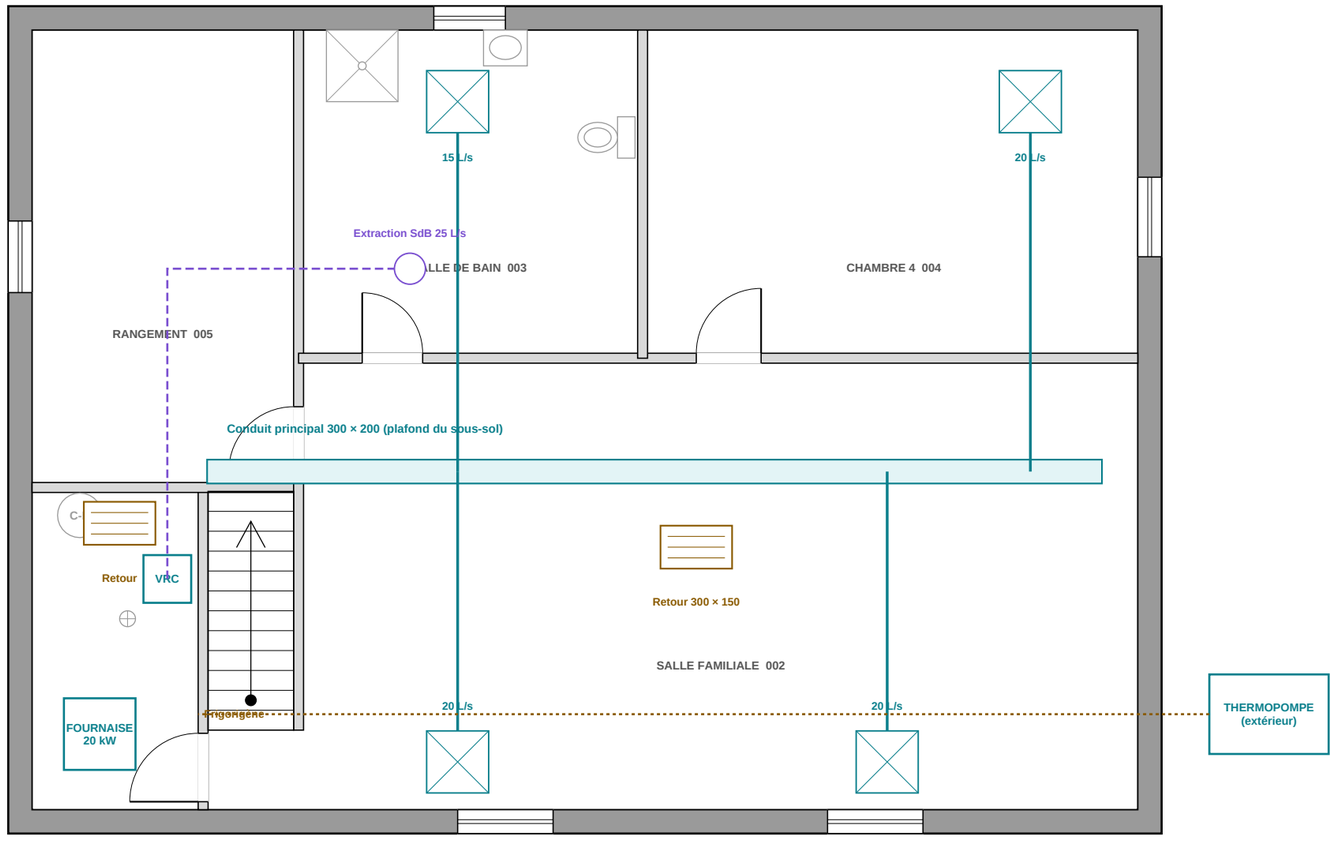

1 **PLAN DE CHAUFFAGE ET VENTILATION**
Échelle 1:75

Pavillon de L'AVENIR
Centre de formation professionnelle

PLAN D'EXERCICE
LECTURE DE PLANS

PROJET

MAISON UNIFAMILIALE
DOSSIER 1

125, rue des Érables
Ville fictive (Québec)

NOTES CVCA

Fournaise électrique 20 kW et thermopompe centrale de 2 tonnes.

Conduits d'acier galvanisé dans le plafond du sous-sol, colonnes vers les étages (voir M-102, M-103).

VRC : extraction des salles de bain et de la cuisine, air neuf au retour de la fournaise.

Débits en litres par seconde (L/s).

LÉGENDE

Conduit d'alimentation

Carré avec X : diffuseur d'alimentation (L/s)

Rectangle ligné : grille de retour

Conduit d'évacuation (VRC)

TITRE DE LA FEUILLE

CHAUFFAGE ET VENTILATION SOUS-SOL

CONÇU PAR

Jeremy, enseignant

DESSIN À DES FINS D'ENSEIGNEMENT — NE PAS UTILISER POUR LA CONSTRUCTION

ÉCHELLE

1:75


DATE

Octobre 2026

FEUILLE

M-101

Dossier D1

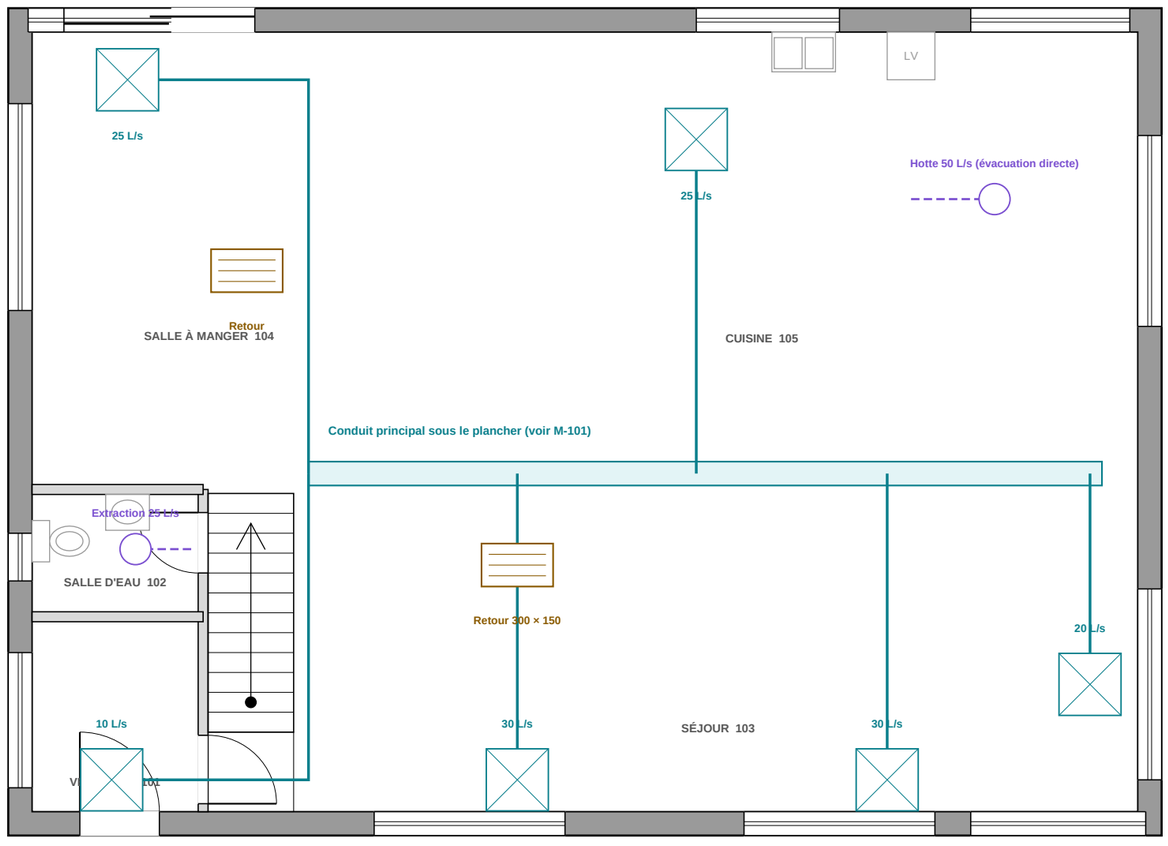

1 **PLAN DE CHAUFFAGE ET VENTILATION**
Échelle 1:75

N

Pavillon de L'AVENIR
Centre de formation professionnelle

PLAN D'EXERCICE
LECTURE DE PLANS

PROJET

MAISON UNIFAMILIALE
DOSSIER 1

125, rue des Érables
Ville fictive (Québec)

NOTES CVCA

Diffuseurs au plancher, sous les grandes fenêtres.

Retours au mur intérieur, ramenés au sous-sol.

Hotte de cuisinière évacuée directement à l'extérieur.

LÉGENDE

Conduit d'alimentation
Carré avec X : diffuseur d'alimentation (L/s)
Rectangle ligné : grille de retour
Conduit d'évacuation (VRC)

TITRE DE LA FEUILLE

CHAUFFAGE ET VENTILATION
REZ-DE-CHAUSSÉE

CONÇU PAR
Jeremy, enseignant


DESSIN À DES FINS D'ENSEIGNEMENT — NE PAS UTILISER POUR LA CONSTRUCTION

ÉCHELLE
1:75

DATE
Octobre 2026

FEUILLE
M-102
Dossier D1

N

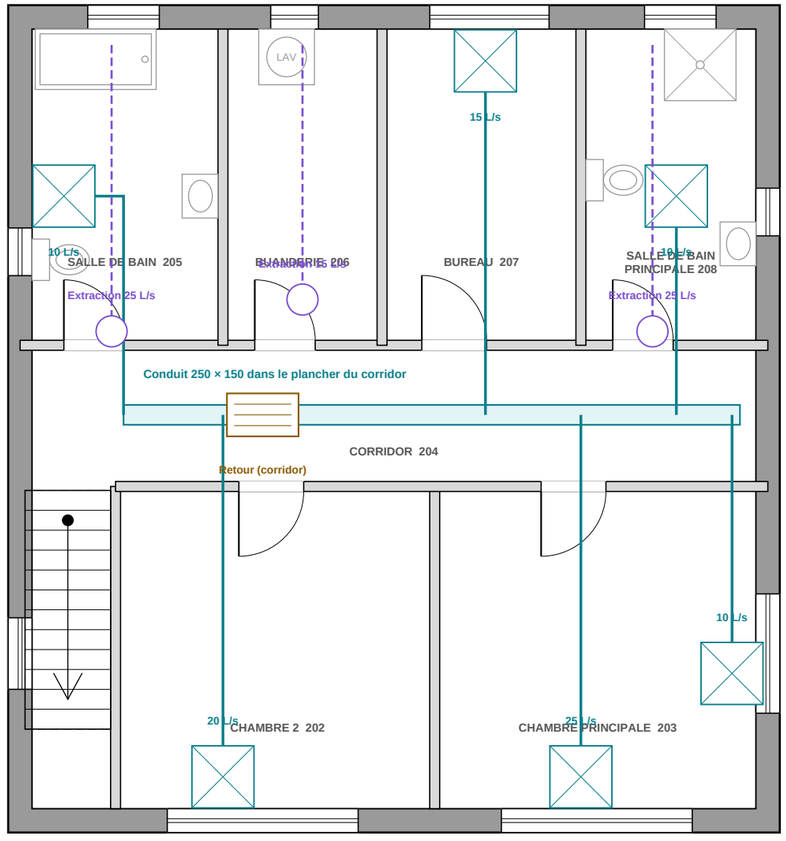

1 **PLAN DE CHAUFFAGE ET VENTILATION**
Échelle 1:75

Pavillon de L'AVENIR
Centre de formation professionnelle

PLAN D'EXERCICE
LECTURE DE PLANS

PROJET

MAISON UNIFAMILIALE
DOSSIER 1

125, rue des Érables
Ville fictive (Québec)

NOTES CVCA

Colonne d'alimentation montant du sous-sol dans le mur de l'escalier.

Un diffuseur sous chaque fenêtre de chambre.

VRC : extraction des deux salles de bain et de la buanderie.

LÉGENDE

Conduit d'alimentation

Carré avec X : diffuseur d'alimentation (L/s)

Rectangle ligné : grille de retour

Conduit d'évacuation (VRC)

TITRE DE LA FEUILLE

CHAUFFAGE ET VENTILATION ÉTAGE

CONÇU PAR
Jeremy, enseignant

DESSIN À DES FINS D'ENSEIGNEMENT — NE PAS UTILISER POUR LA CONSTRUCTION

ÉCHELLE
1:75

DATE
Octobre 2026

FEUILLE
M-103
Dossier D1